



1 BC-01 GABINETE SOB GRANITO
ESCALA 1:40

4 mod. - 0 pontos - 0 gar - 24 pontos - perfil gabi de alumínio graf

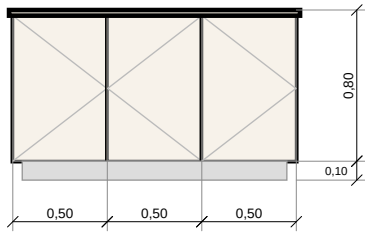


4 BC-03 GABINETE SOB GRANITO
ESCALA 1:40

3 mod. - 0 pontos - 0 gar - 18 pontos - perfil gabi de alumínio graf

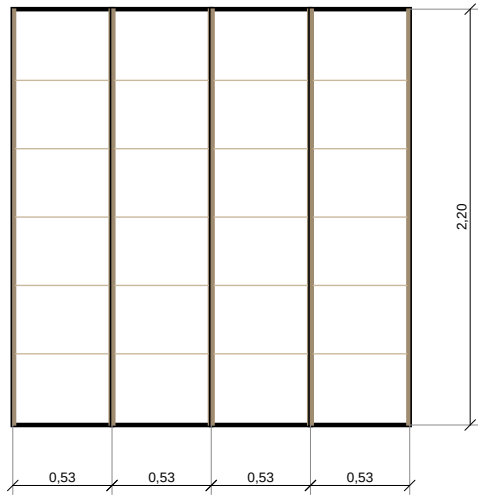


7 AR-06 PRATELEIRAS
ESCALA 1:40

4 mod. - 0 pontos - 0 gar - 40 pontos - perfil gabi de alumínio graf

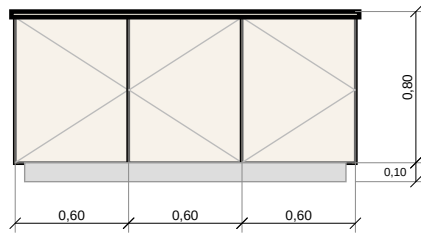


2 BC-02 GABINETE SOB GRANITO
ESCALA 1:40

3 mod. - 0 pontos - 0 gar - 18 pontos - perfil gabi de alumínio graf

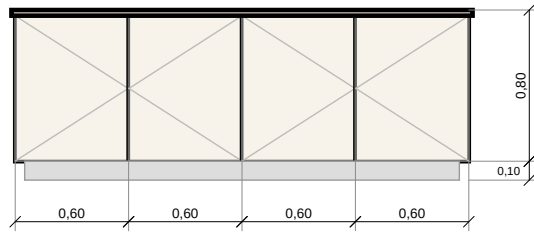


5 BC-06 GABINETE SOB GRANITO
ESCALA 1:40

4 mod. - 0 pontos - 0 gar - 24 pontos - perfil gabi de alumínio graf

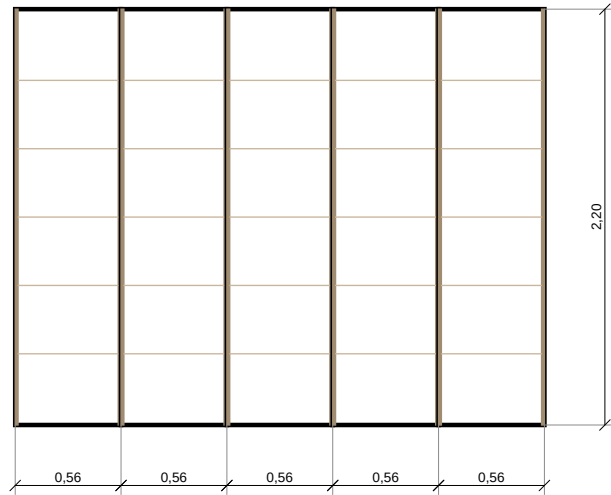


8 AR-03 PRATELEIRAS
ESCALA 1:40

5 mod. - 0 pontos - 0 gar - 50 pontos - perfil gabi de alumínio graf

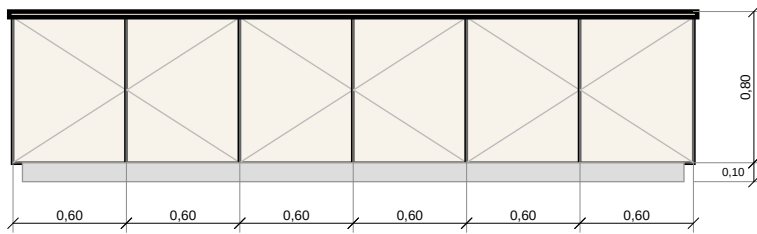


3 BC-04 GABINETE SOB GRANITO
ESCALA 1:40

6 mod. - 0 pontos - 0 gar - 36 pontos - perfil gabi de alumínio graf

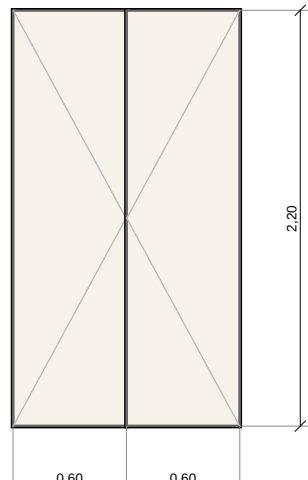


6 AR-08 ARMARIO ALTO
ESCALA 1:40

2 mod. - 2 pontos - 0 gar - 20 pontos - perfil gabi de alumínio graf

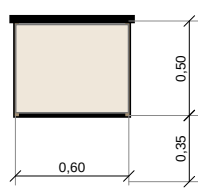


9 LC-02 GAB. LAVATORIO
ESCALA 1:40

1 mod. - 0 pontos - 2 gar - 20 pontos - canto voltado a 45 graus (sem)

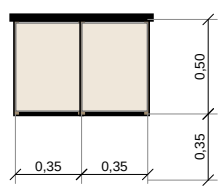


11 LC-05 GAB. LAVATORIO
ESCALA 1:40

2 mod. - 0 pontos - 2 gar - 20 pontos - canto voltado a 45 graus (sem)

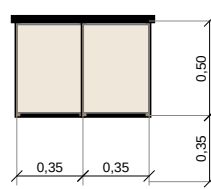


10 LC-15 GAB. LAVATORIO
ESCALA 1:40

2 mod. - 0 pontos - 2 gar - 20 pontos - canto voltado a 45 graus (sem)

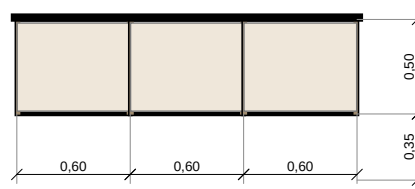

12 LC-11 GAB. LAVATORIO
ESCALA 1:40

3 mod. - 0 pontos - 3 gar - 30 pontos - canto voltado a 45 graus (sem)

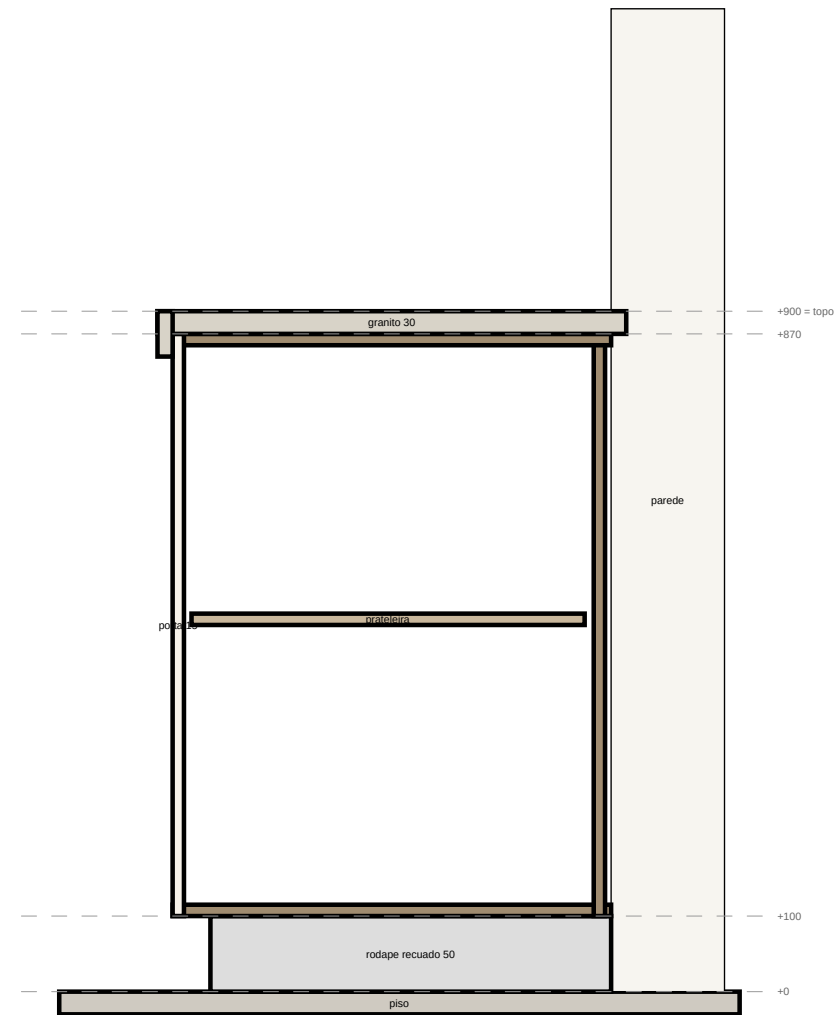

A SECAO DO GABINETE SOB GRANITO — APOIO E RODAPE
ESCALA 1:10

NOTAS

- Gabinete sob granito: canto de MDF 15 mm sobre suporte, rodape recuado 50 mm, tempo a 900 mm. Módulo com todos sem prateleira, módulo de cooktop com uma.
- Gabinete de lavatório suspenso a 200 mm do piso, uma gaveta por módulo, cuba de apoio.
- Porta por módulo, dobradiças pela altura (2 até 900, 3 até 1.500, 4 até 2.000, 5 acima).
- Prateleira trançada e arcos de porta. Puxador perfil gabi graf no canto externo.

PROJETO PORTO REAL

RESIDENCIA UNIFAMILIAR (MANAUS - AM) | SOUZA TATIANA-PS

PROJETO ARQUITETONICO

MARCENARIA I — GABINETES DE COZINHA, GOURMET, OFICINA E BANHOS

BASE GEOMETRICA	ESCALA	EMISSAO	PROJECION
União Consolidada	1:40 • 1:10	ESTUDO PRELIMINAR RBS	56
Projeto (previsão)	FORMATO A1	NAO LIBERADO PARA OBRA	SEM ART / RNT
UNIDADE: METRO: MM	MAQUETA: 600/900/300		DE 15 REVIEWS