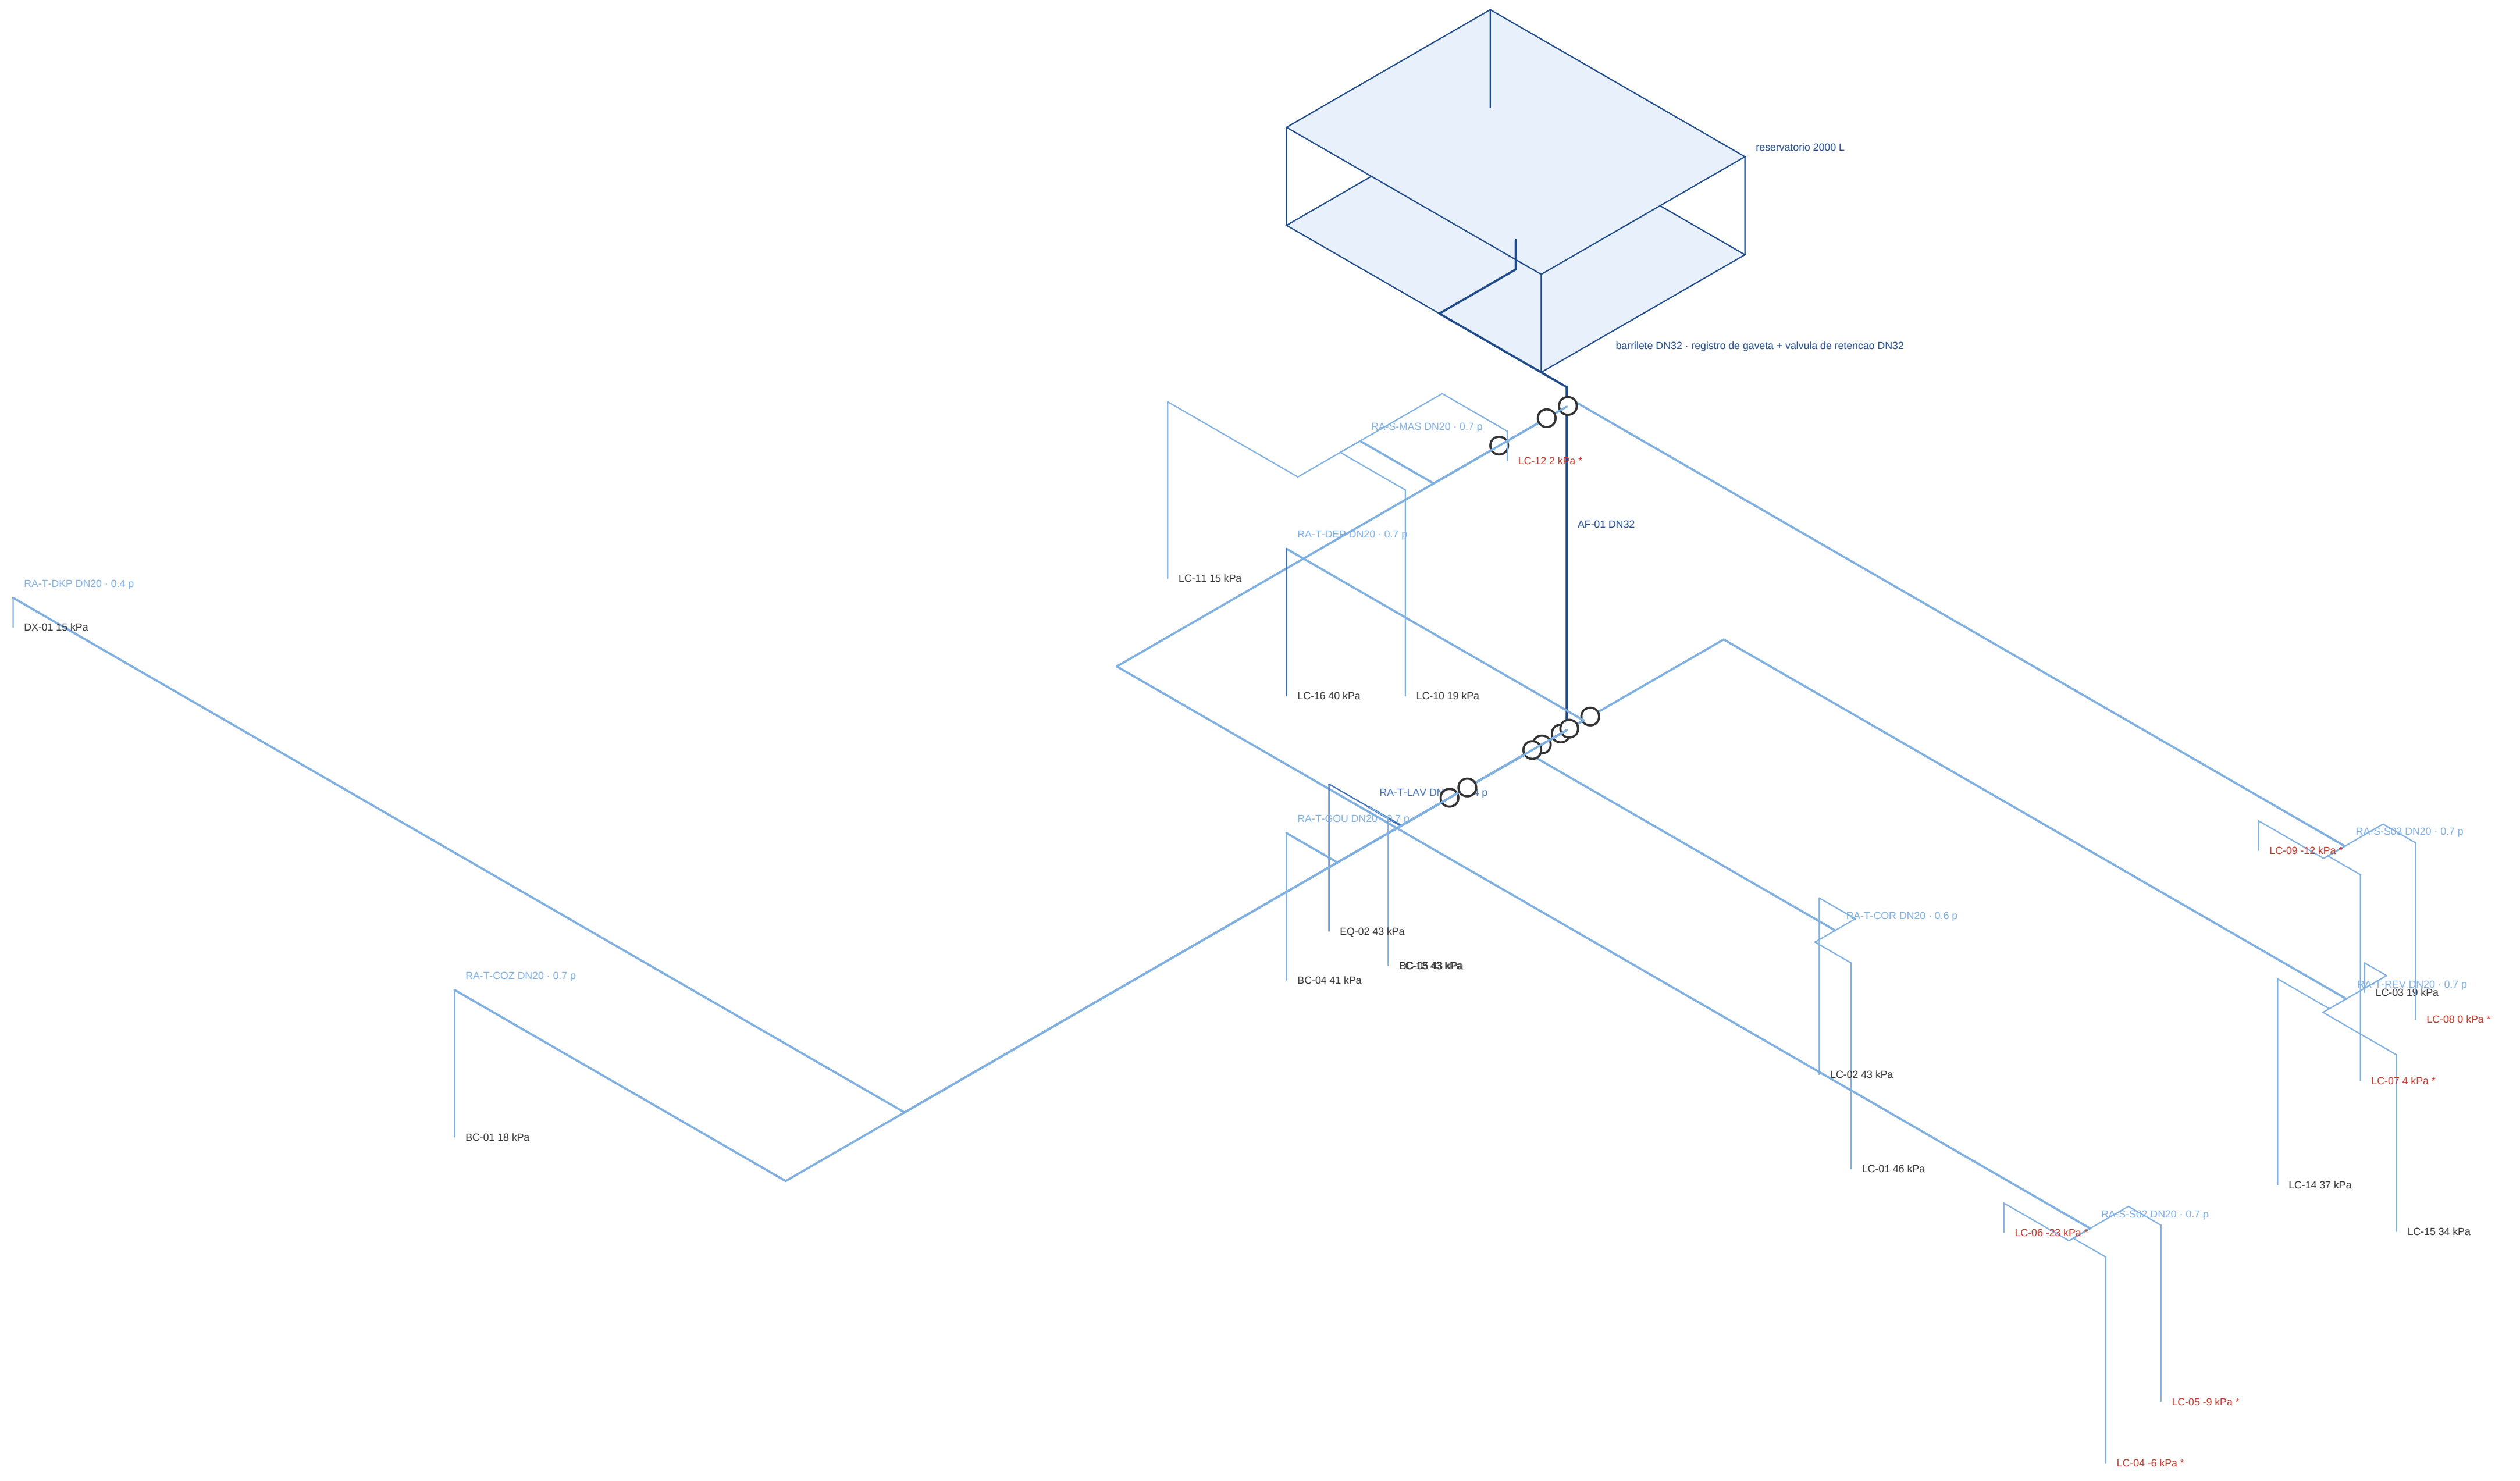

1

ISOMETRICO DE AGUA FRIA (* abaixo de 10 kPa por gravidade: pressurizado)

ESCALA 1:75

DIAGRAMA VERTICAL

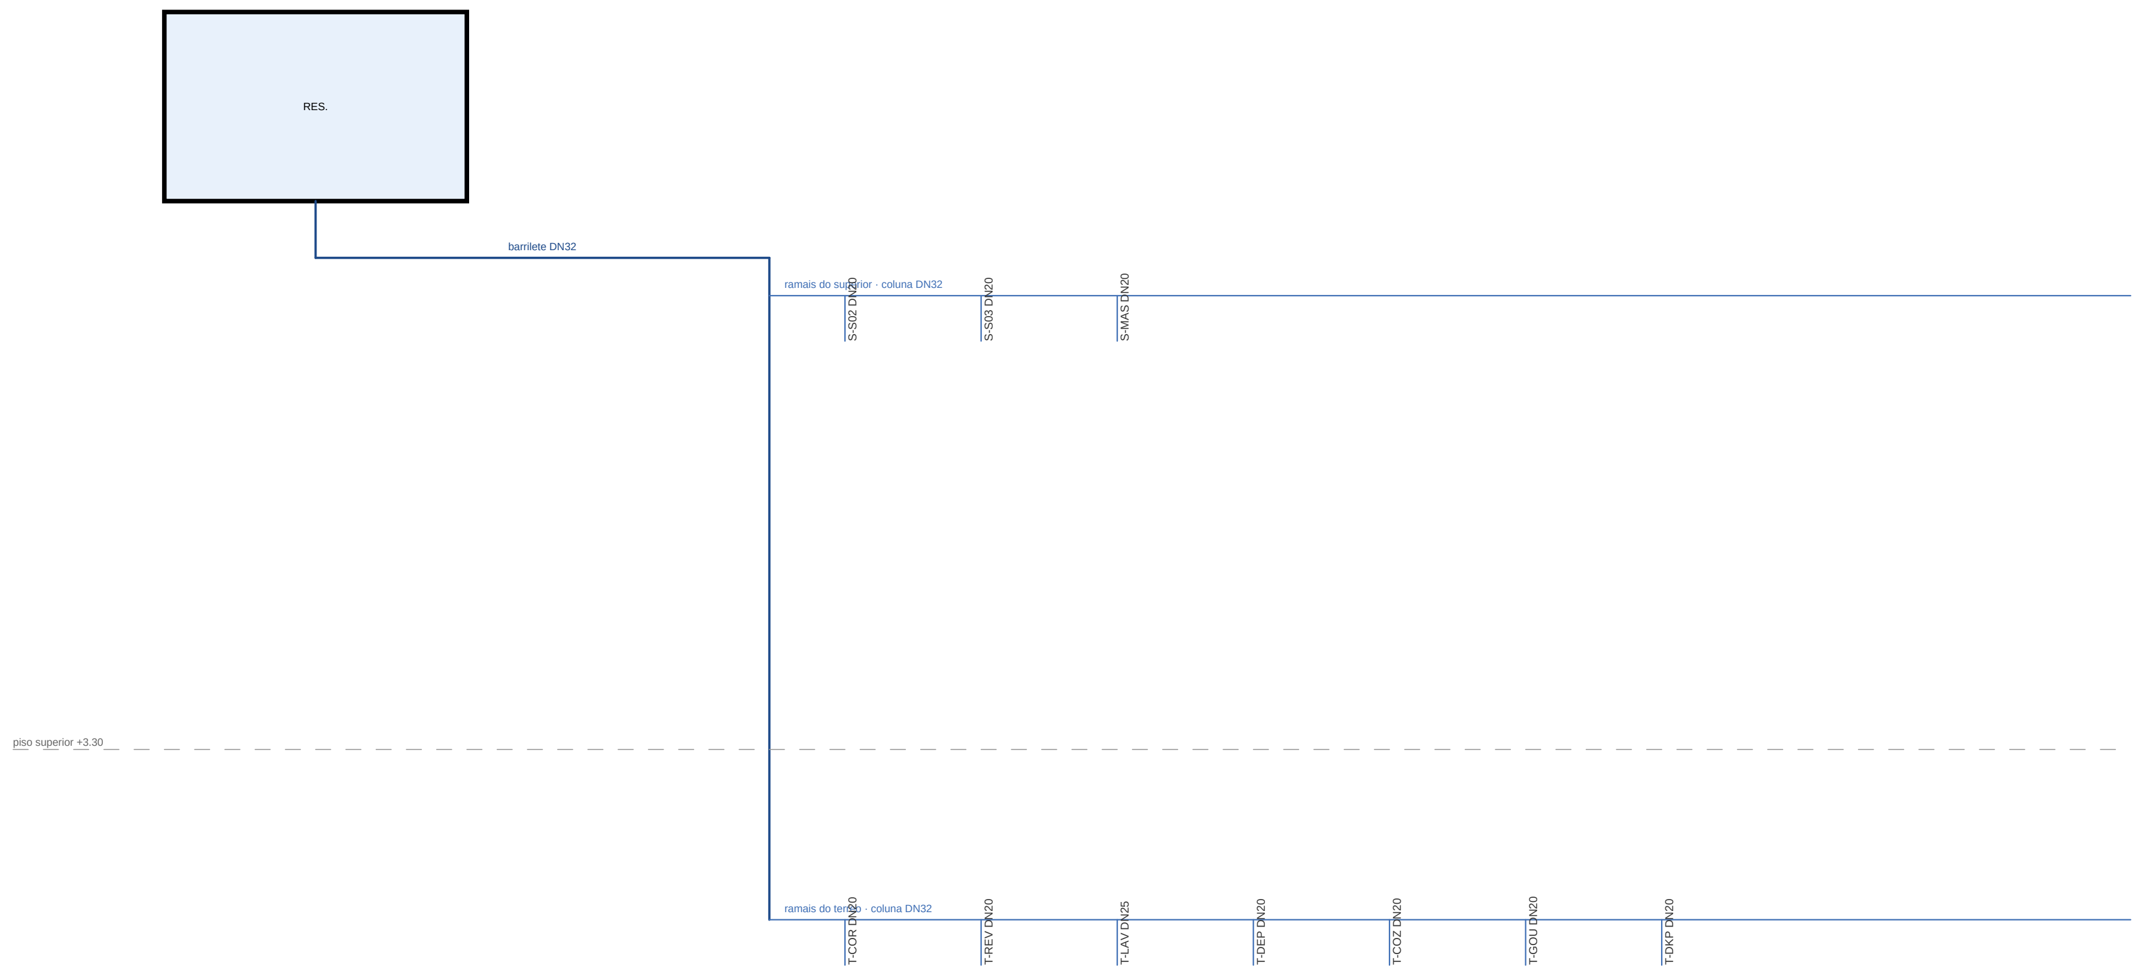

PRESSAO EM CADA PECA (kPa)

PECA	AMB	TIPO	z mm	SUB	ESTAT.	PERDAS	DINAM.	COMO
LC-01	T-COR	vaso	300	DN20	60	14	46	gravidade
LC-02	T-COR	lavatorio	600	DN20	57	14	43	gravidade
LC-03	T-REV	box	2100	DN20	42	23	19	gravidade
LC-14	T-REV	vaso	300	DN20	60	23	37	gravidade
LC-15	T-REV	lavatorio	600	DN20	57	23	34	gravidade
LC-04	S-S02	vaso	3600	DN20	28	33	-6	TC-14
LC-05	S-S02	lavatorio	3900	DN20	24	33	-9	TC-14
LC-06	S-S02	box	5400	DN20	10	33	-23	TC-14
LC-07	S-S03	vaso	3600	DN20	28	24	4	TC-14
LC-08	S-S03	lavatorio	3900	DN20	24	24	0	TC-14
LC-09	S-S03	box	5400	DN20	10	21	-12	TC-14
LC-10	S-MAS	vaso	3600	DN20	28	8	19	gravidade
LC-11	S-MAS	lavatorio	3900	DN20	24	10	15	gravidade
LC-12	S-MAS	box	5400	DN20	10	8	2	TC-14
LC-13	T-LAV	tanque	900	DN25	54	11	43	gravidade
LC-16	T-DEP	tanque	900	DN25	54	14	40	gravidade
BC-01	T-COZ	pia	900	DN20	54	36	18	gravidade
BC-04	T-GOU	pia	900	DN20	54	13	41	gravidade
BC-05	T-LAV	pia	900	DN20	54	11	43	gravidade
EQ-02	T-LAV	lavadora	900	DN25	54	11	43	gravidade
DX-01	T-DKP	ducha_exte	2100	DN20	42	27	15	gravidade

TRECHOS — BARRILETE, COLUNA E RAMAIS

TRECHO	DN	PESOS	Q L/s	L m	PERDA kPa
BAR	DN32	8.3	0.864	3.2	3.8
COL-S	DN32	8.3	0.864	0.2	0.2
COL-T	DN32	6.2	0.747	3.3	3.1
RA-T-COR	DN20	0.6	0.232	4.9	6.2
RA-T-REV	DN20	0.7	0.251	11.0	15.8
RA-S-S02	DN20	0.7	0.251	20.1	28.9
RA-S-S03	DN20	0.7	0.251	11.0	15.8
RA-S-MAS	DN20	0.7	0.251	2.9	4.2
RA-T-LAV	DN25	2.4	0.465	2.8	3.8
RA-T-DEP	DN20	0.7	0.251	4.4	6.4
RA-T-COZ	DN20	0.7	0.251	15.7	22.6
RA-T-GOU	DN20	0.7	0.251	4.0	5.7
RA-T-DKP	DN20	0.4	0.19	22.0	19.4

REGISTROS — 18

COD	ONDE	TIPO
RG-GERAL	saida do reservatorio (barrilete)	registro de gaveta + valvula de re
RG-COL-S	ramais do superior	registro de gaveta DN32
RG-COL-T	ramais do terreo	registro de gaveta DN32
RG-T-COR	entrada do ramal de T-COR	registro de gaveta DN20
RG-T-REV	entrada do ramal de T-REV	registro de gaveta DN20
RG-S-S02	entrada do ramal de S-S02	registro de gaveta DN20
RG-S-S03	entrada do ramal de S-S03	registro de gaveta DN20
RG-S-MAS	entrada do ramal de S-MAS	registro de gaveta DN20
RG-T-LAV	entrada do ramal de T-LAV	registro de gaveta DN25
RG-T-DEP	entrada do ramal de T-DEP	registro de gaveta DN20
RG-T-COZ	entrada do ramal de T-COZ	registro de gaveta DN20
RG-T-GOU	entrada do ramal de T-GOU	registro de gaveta DN20
RG-T-DKP	entrada do ramal de T-DKP	registro de gaveta DN20
RP-LC-03	box LC-03	registro de pressao DN20
RP-LC-06	box LC-06	registro de pressao DN20
RP-LC-09	box LC-09	registro de pressao DN20
RP-LC-12	box LC-12	registro de pressao DN20
RP-DX-01	ducha_externa DX-01	registro de pressao DN20

NOTAS

- Reservatorio de 2000 L com fundo a +6.20 m; barrilete DN32 a +5.90 m; coluna AF-01 DN32.
- Pressao dinamica = estatica (lamina minima 200 mm sobre o fundo) menos as perdas por Fair-Whipple-Hsiao (PVC) com 30 % de localizadas; minimo 10 kPa (NBR 5626).
- Terreo: pior peca com 15 kPa — passa por gravidade. Superior: pior peca com -23 kPa — 7 pecas so funcionam com o pressurizador TC-14. E a conta, nao a frase, que justifica o equipamento.
- Registro de gaveta na entrada de cada ramal; registro de pressao em cada chuveiro; geral com retencao no barrilete.

PROJETO PORTO REAL
RESIDENCIA UNIFAMILIAR | MANAUS - AM | SU16 TARUMA (H)

PROJETO ARQUITETONICO
AGUA FRIA — ISOMETRICO, DIAGRAMA VERTICAL, PRESSOES E REGISTROS

BASE GEOMETRICA	ESCALA	EMISSAO	PRANCHA
Lista Consolidada pos-R32 (prevalece) UNIDADE MESTRE: mm	1:75 FORMATO A1 MALHA 600/300/150	ESTUDO PRELIMINAR R85 NAO LIBERADO PARA OBRA SEM ART / RRT	63 de 76 REV R85