


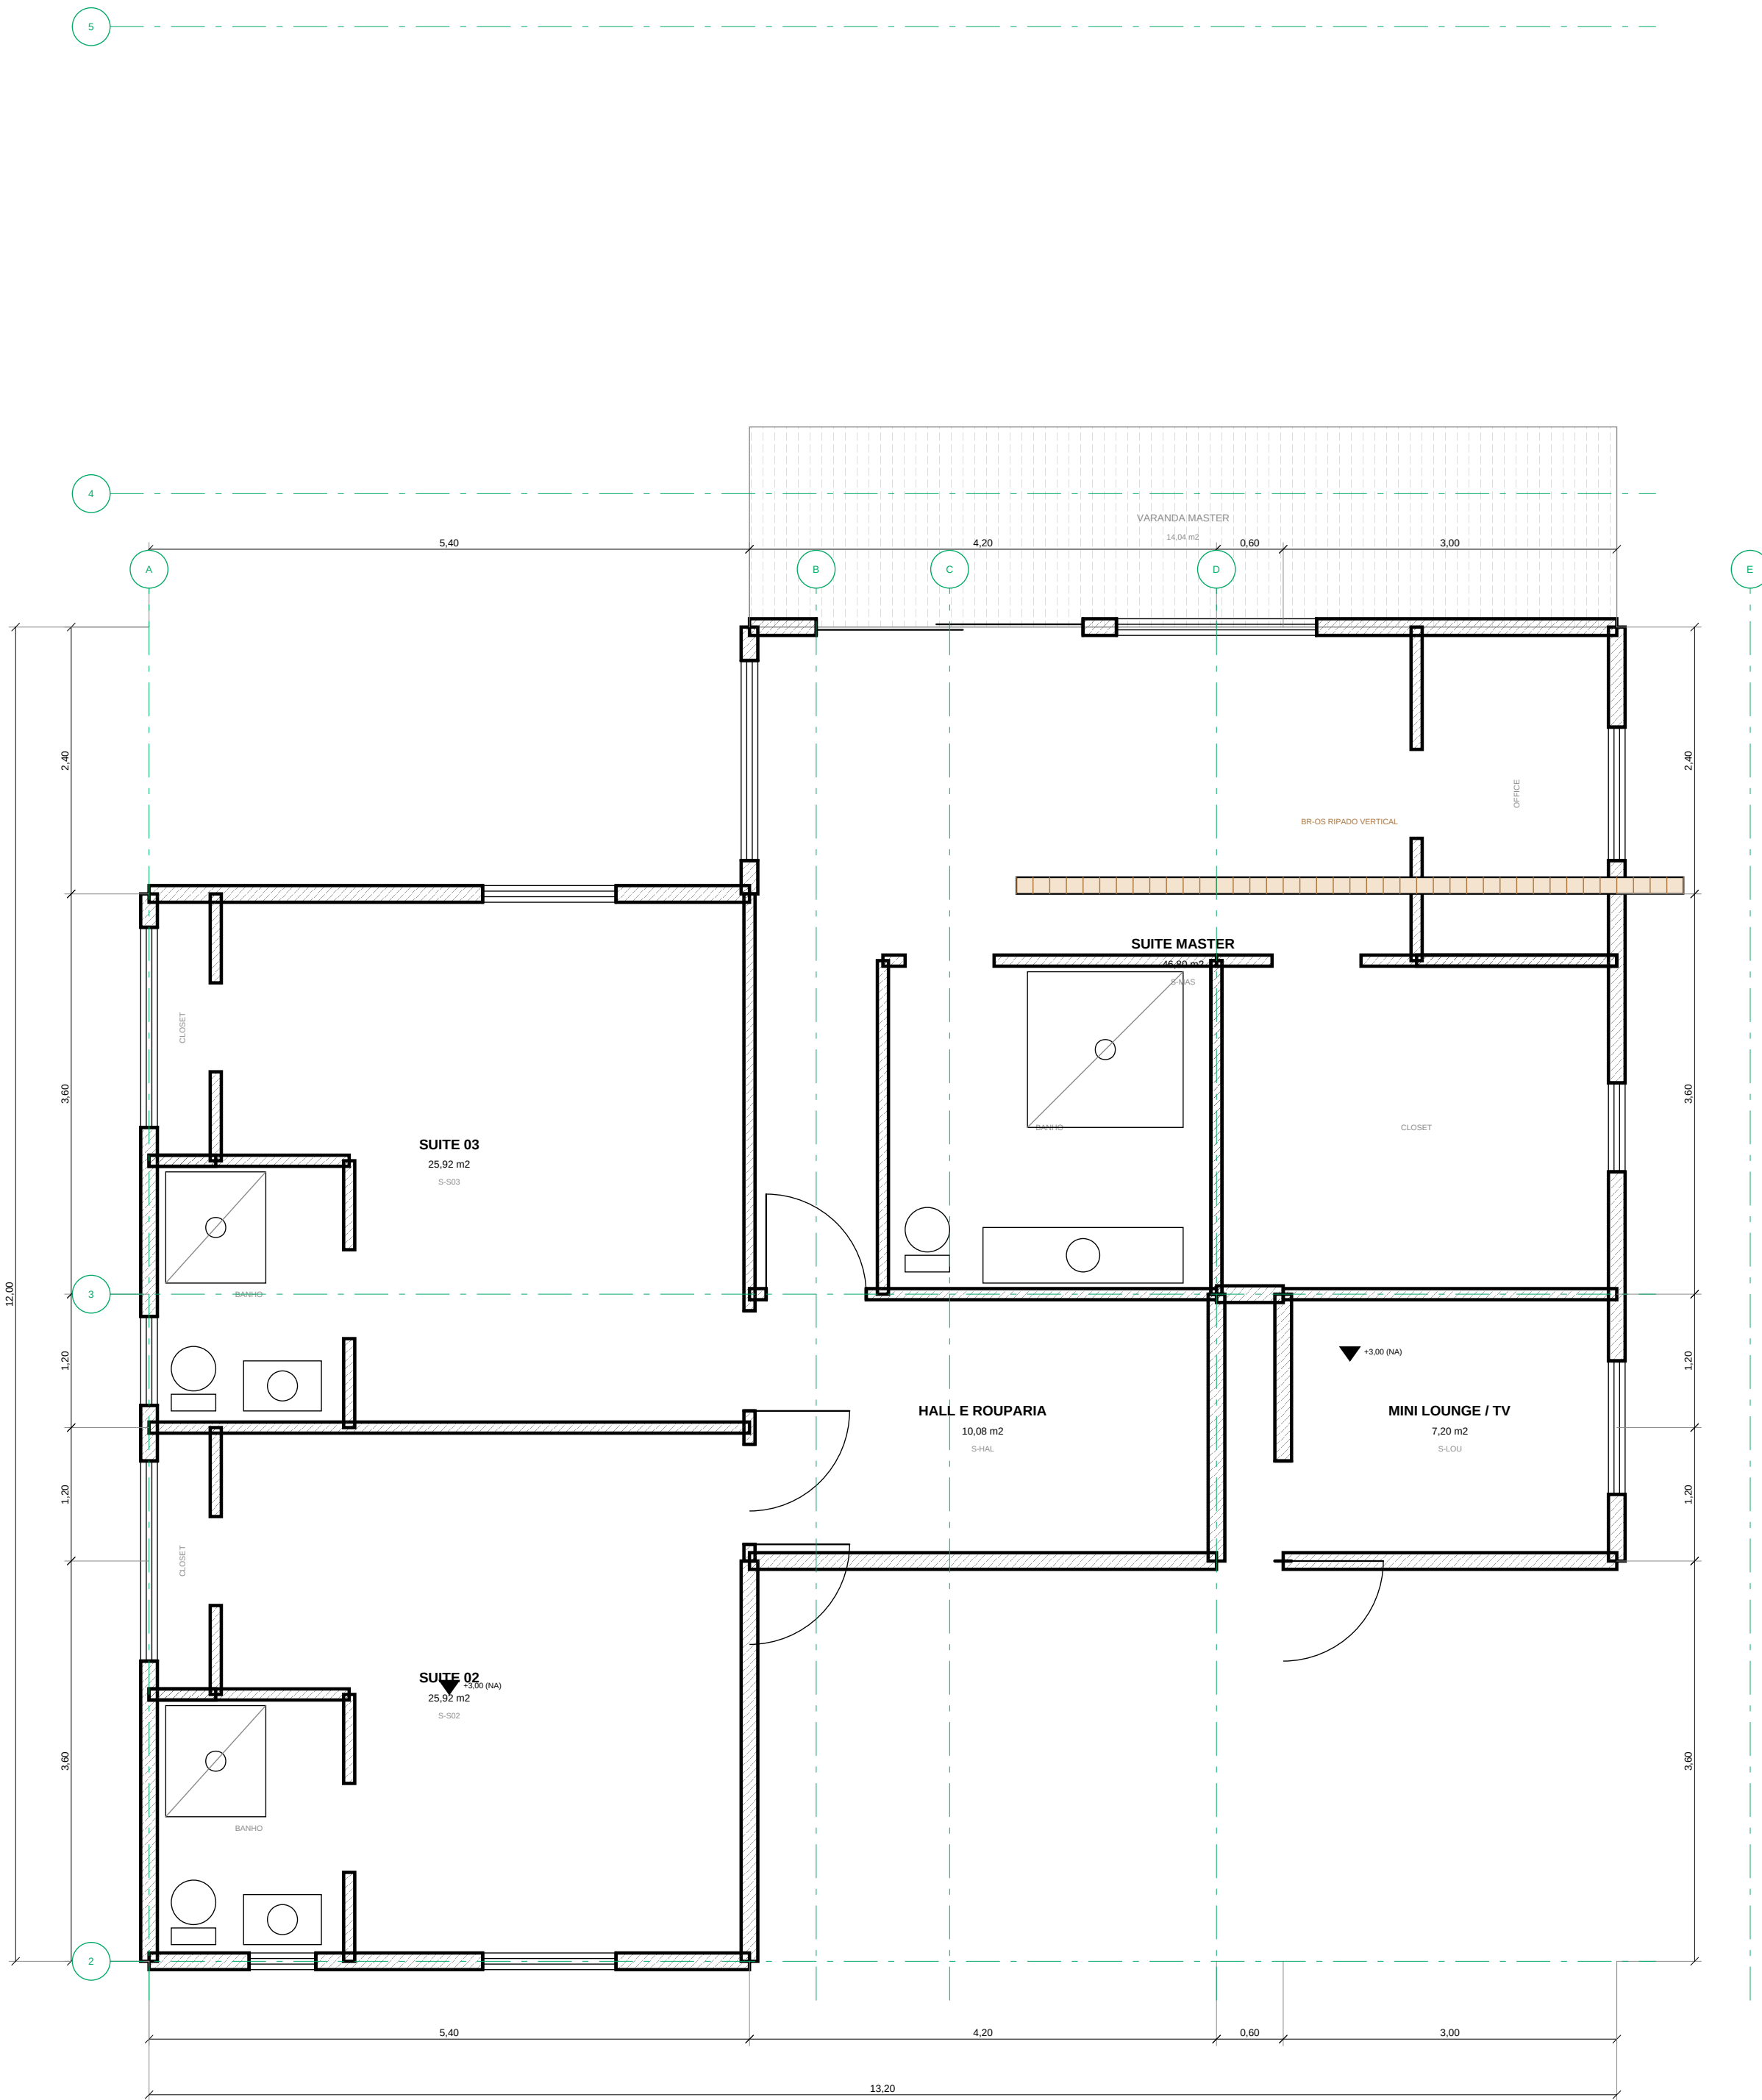

1 PAVIMENTO SUPERIOR
ESCALA 1:50



QUADRO DE ÁREAS — PAVIMENTO SUPERIOR


COD	AMBIENTE	MÓDULO (m²)	ÁREA (m²)
S-001	SUITE 01	5400x4800	25,92
S-002	SUITE 02	5400x4800	25,92
S-003	SUITE 03	5400x4800	25,92
S-004	HALL E ROUPARIA	4200x4800	15,00
S-005	MINI LOUNGE / TV	3000x2400	7,20
S-006	SUITE MASTER	7000x6000	42,00
TOTAL FECHADO			116,04
S-BAL	VARANDA MASTER (aberta)	7000x1800	12,64

MAPA DE ESQUADRIAS DO PAVIMENTO

REF	VÃO (mm)	DET.	QTD	TIPO
J01	1200x1200	1200	4	janela de dormitório, alumínio
J02	600x600	1200	1	janela de banheiro, vidro translúcido
J04	800x800	1200	2	janela alta de banheiro, translúcido
J05	1800x1200	1200	4	janela ampla de dormitório, alumínio
P02	800x1200	0	4	porta interna (chamada unificada)
P03	3000x4800	0	1	porta-folha de entrada (chamada adicional - ver

LEGENDA E CONVENÇÕES (NBR 6492 / 8403)

- Elemento seccionado pelo plano de corte (h = 1,50 m)
- Alvenaria simples / tijolo de esquadro
- Mobiliário fixo, equipamento e eletrotécnica
- Propriedade do pavimento superior e da cobertura
- Eixo modular e linha de corte
- Linha de corte e linha auxiliar

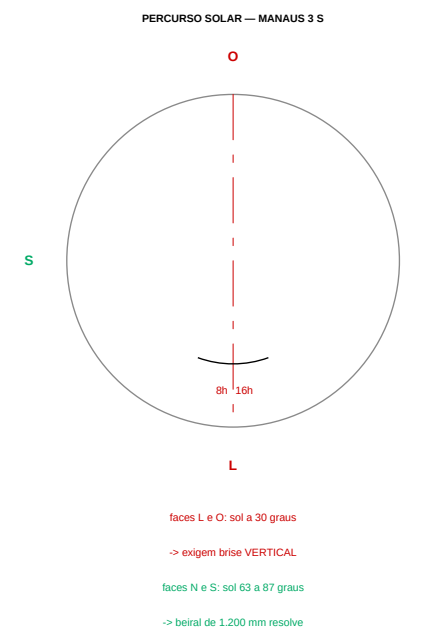

- NOTAS
- Dimensões em milímetros; cotas de nível em metros.
 - Malha modular 600 mm; cotas eixo a eixo.
 - Planta externa 120 mm / distância interna 120 mm (S).
 - Modulador fixo indica pontos de água e energia (NBR 6492).

PROJETO PORTO REAL

RESIDÊNCIA UNIFAMILIAR (MANUS - AM) | SOUZA TATIANA (PS)

PROJETO ARQUITETÔNICO

PLANTA BAIXA — PAVIMENTO SUPERIOR

BASE GEOMÉTRICA Linha Consolidada ISO 8572 (previável) UNIDADE MESTRE: mm	ESCALA 1:50 FORMATO A1 MALHA 600/600 (mm)	EMISSÃO ESTUDO PRELIMINAR NÃO LIBERADO PARA OBRA SEM ART / RNT	PROJETO 03 05/25
--	--	---	------------------------