
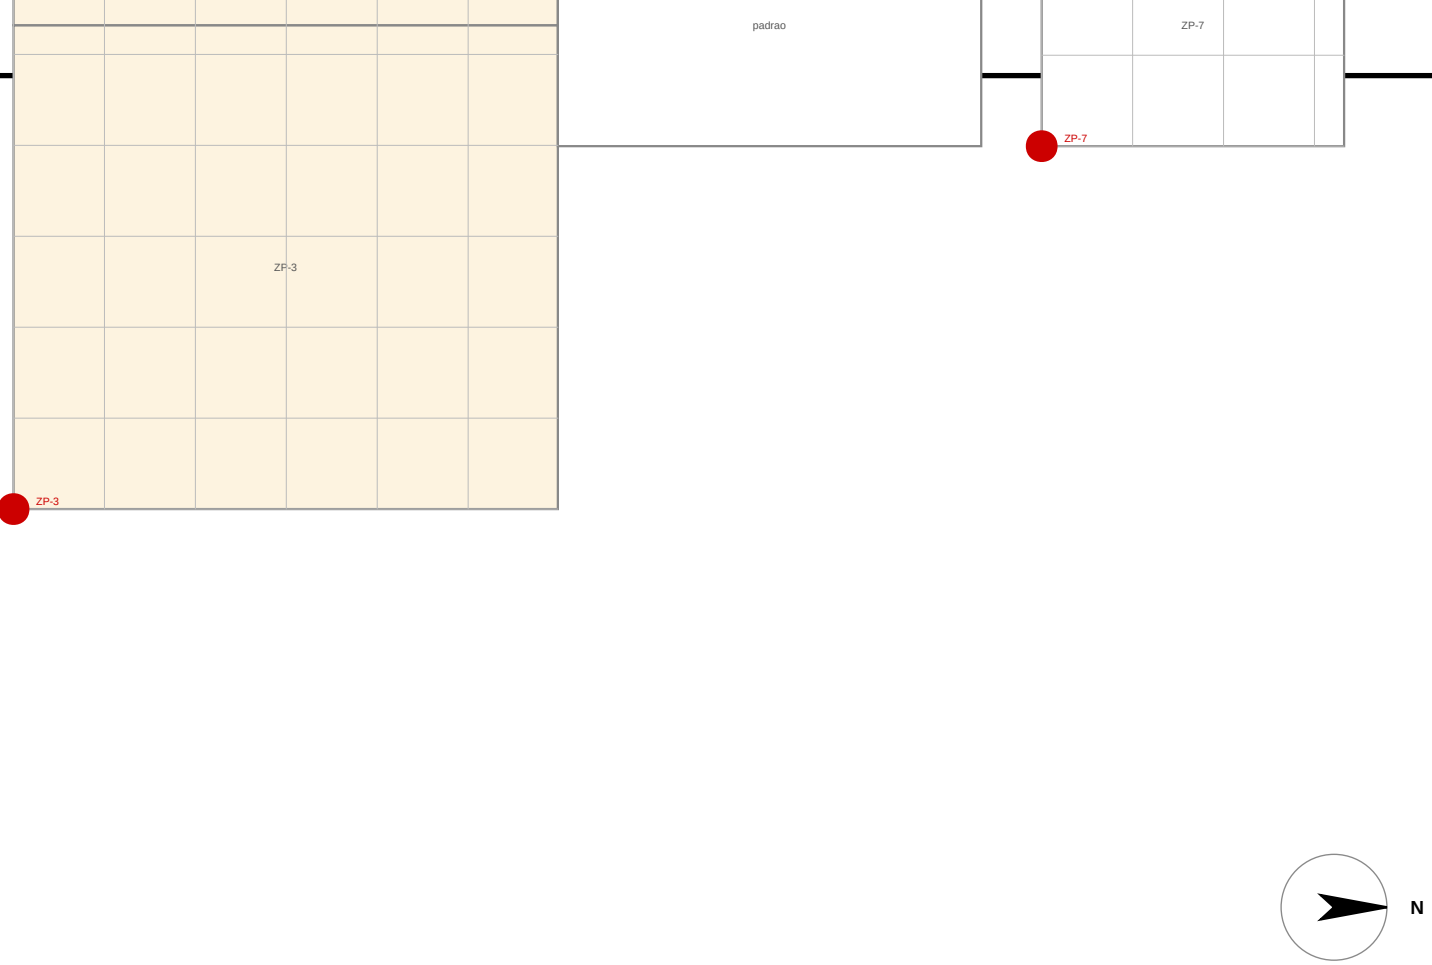


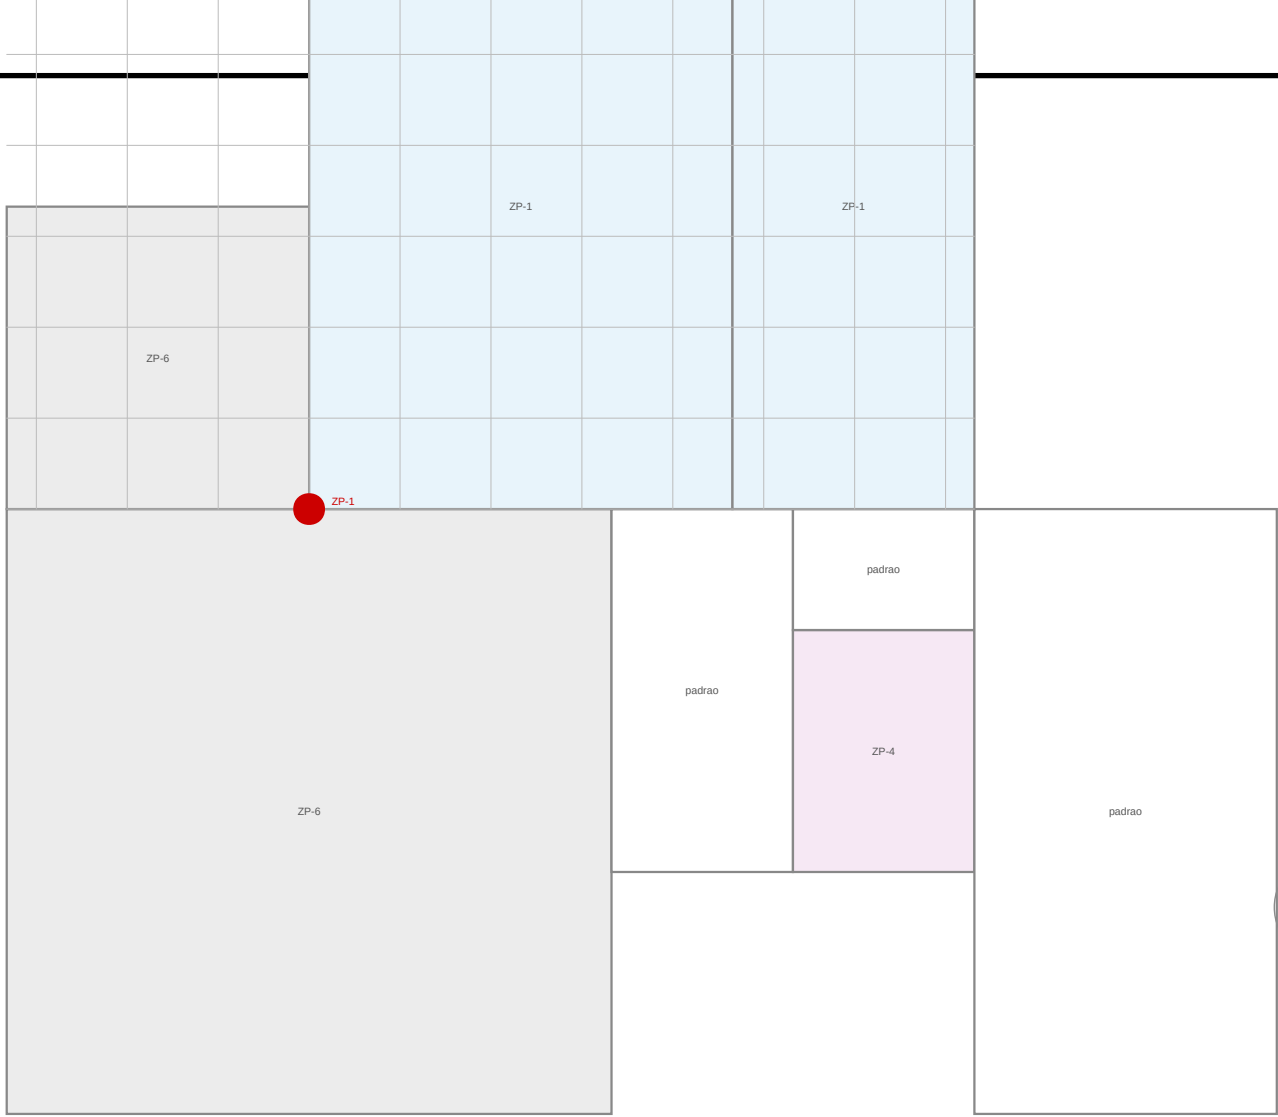

1 PAGINACAO — TERREO
ESCALA 1:75

2 PAGINACAO — SUPERIOR
ESCALA 1:75

ZONAS DE PAGINACAO

ZONA	PEÇA	ORDEM	AMBIENTES	PEÇA ESPECIFICADA	PON RECORTE	COMENTARIO
ZP-1	piso	(5400, 12000)	T-BOC, T-CORR, T-GOLU, T-COZ	porcelanato retificado 900 x 900	204	risco social interno em uma malha, origem no eixo da porta do n
ZP-2	piso	(7000, 10000)	S-MAS	porcelanato retificado 900 x 900	100	origem no eixo da porta do suite
ZP-3	piso	(2400, 12000)	S-SOC, S-SO3	porcelanato retificado 900 x 900	200	salto 12 e 15 na mesma malha, a parede entre elas é deslanta
ZP-7	piso	(12000, 10000)	S-LOU	porcelanato retificado 900 x 900	202	o lounge tem porta e não é integrado a nada, pagina do projeto
ZP-4	parede	carão do ambiente	T-BWC	ceramica retificado 300 x 600	208	em o bco terminado de 2.400 (que se estende para a esquerda)
ZP-5	parede	carão do ambiente	T-LAV, T-DEP	ceramica retificado 300 x 600	200	em o parede de 1.800 tem o arco do banheiro, das maquina e das p
ZP-6	revestimento	(1400, 12000)	T-GP1, T-GP2	ceramica polido	—	piso ceramico polido de alta resistencia, sem paginação cores

NOTAS

* Pagar no projeto e decidir onde fica o corte. Não pagar e deixar o corte aparecer no lugar mais visível.

* Ambientes integrados revestidos com a mesma malha, a porta deslanta no meio da sala não tem parede para a direita.

* Recorte interno de 20% da peça, além de 20% o recorte deslanta e é reproduzido.

PROJETO PORTO REAL

RESIDENCIA UNIFAMILIAR (MANAUS - AM) | SOU TATIANA-PS

PROJETO ARQUITETONICO

PAGINACAO DE PISO E ZONAS DE REVESTIMENTO

BASE GEOMETRICA Linha Consolidada PIS-RTZ (previsão) UNIDADE: METRO: MM	ESCALA 1:75 FORMATO: A1 MALHA: 600/600/300	EMISSAO ESTUDIO PRELIMINAR NÃO LIBERADO PARA OBRA SEM ART / RNT	PROJETO 24 05-25
--	---	--	------------------------