
 
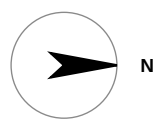


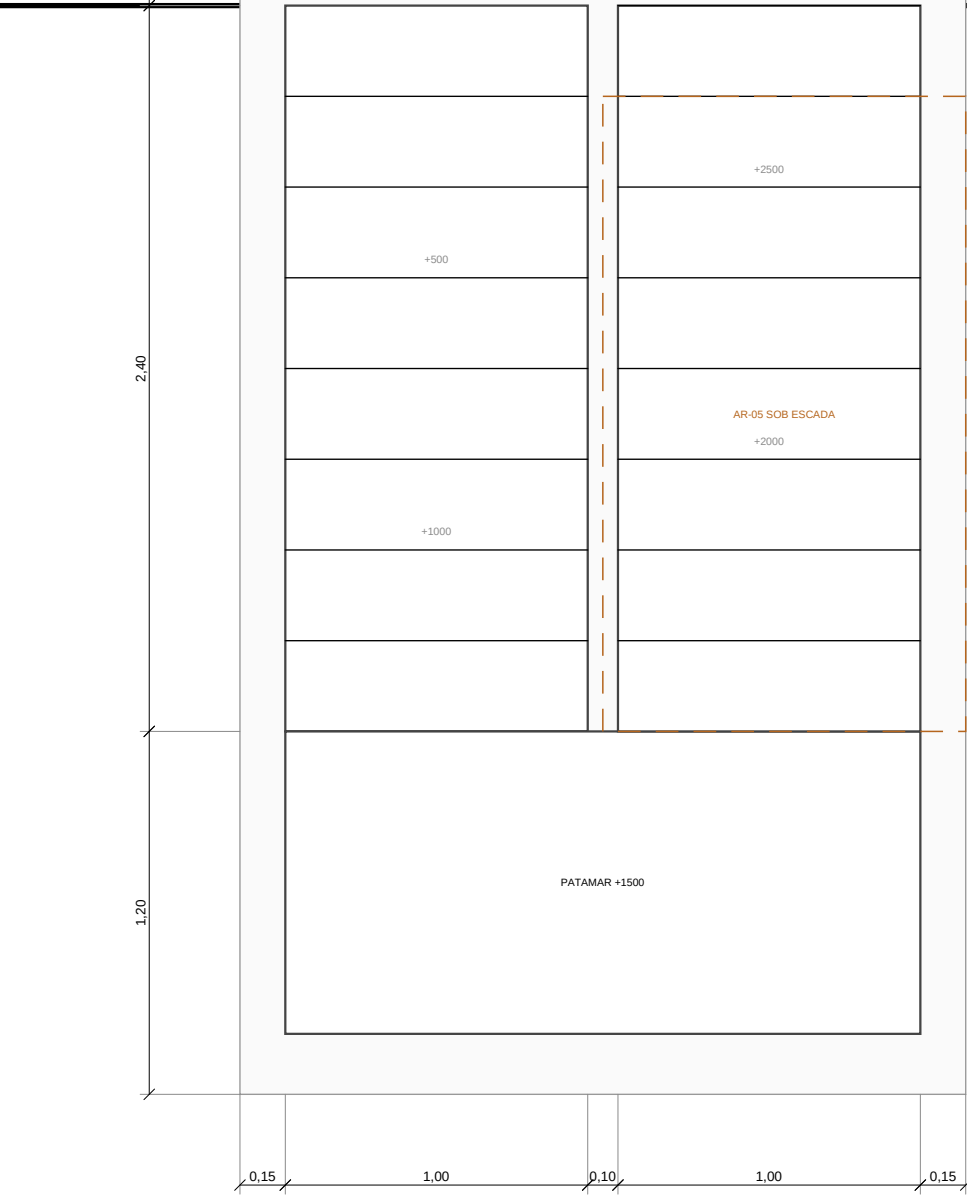

espelho fechado (NBR 9050)

chapa 800x400 3 mm + preenchido 900 x 300

faixa antiderrapante de 25 mm x 25 mm de borda

2 CORTE LONGITUDINAL — ALTURA LIVRE

ESCALA 1:25

3 DETALHE DO DEGRAU

ESCALA 1:5

VERIFICACAO DA ESCADA

ITEM	PROJETO	NORMA	
Espelho	186.67 mm	18 a 18 cm (NBR 9071)	OK
Piso	300 mm	min 28 cm	OK
Bondex (2h + g)	633.3 mm	600 a 650 mm	OK
Largura útil do lance	1000 mm	min 1.200 mm (uso coletivo) / 1.000 mm (particular)	OK
Platamar	1000 mm	→ largura do lance	OK
Altura livre mínima	0 mm	min 2100 mm	EXCETO
Guarda-corpo	1100 mm	min 1.200 mm (NBR 14738)	OK
Corrimão	920 a 1100 mm	Acima 92 cm e 10 cm (NBR 9050)	OK
Espelho fechado	sem	conformidade com esta acurácia	OK
Desnível vencido	3000 mm	18 a 186.67 mm	OK

O QUE A PLANTA NAO MOSTRA

QUESTAO	RESPOSTA
Por que o primeiro espelho sobre o y = 1.2.000	o platamar termina-se 200 mm dentro da projeção do 1º lance superior, com 1.000 mm de altura livre — visto que na altura da colônia do quem termina o primeiro lance
Por que a verificação de altura livre é bidimensional	altura livre do espaço e o único critério que não aparece em planta horizontal, dependendo da cor do degrau e da cor do que há acima dele
O que há sob o segundo lance	intergalo com altura variável, desenhado como amarrado (NBR 9050) mas a circulação tem espaço livre
Por que espelho fechado	degrau visado desde a porta do pé de quem usa largura ou tem mobilidade reduzida (NBR 9050)
Por que corrimão duplo	920 mm para adulto e 700 mm para criança, em caso com escada aberta para a sala, o segundo corrimão é o que realmente se usa

NOTAS

- 18 espelho de 186.67 mm e piso de 300 mm. Bondex 2h + g = 633.3 mm (falso recomendado 600 a 650).
- Altura livre mínima 2100 mm (NBR 9071), verificada desde o degrau contra a laje e o vazio acima.
- Guarda-corpo 1100 mm, corrimão duplo em 920 e 700 mm (NBR 9050).
- dois perfis U 200 laterais com degrau em chapa dobrada 3 mm

PROJETO PORTO REAL

RESIDENCIA UNIFAMILIAR (MANSÃO - AM) | SOUS TATIANA-PS

PROJETO ARQUITETONICO

ESCALA — DESENHO EXECUTIVO

BASE GEOMETRICA	ESCALA	EMISSAO	PROJECION
União Consolidada	indicada	ESTUDIO PRELIMINAR	
ISO 8522 (previsto)	FORMATO A1	NAO LIBERADO PARA OBRA	
UNIDADE: METRO - MM	MAQUA: 600/500/300	SEM ART / RNT	25