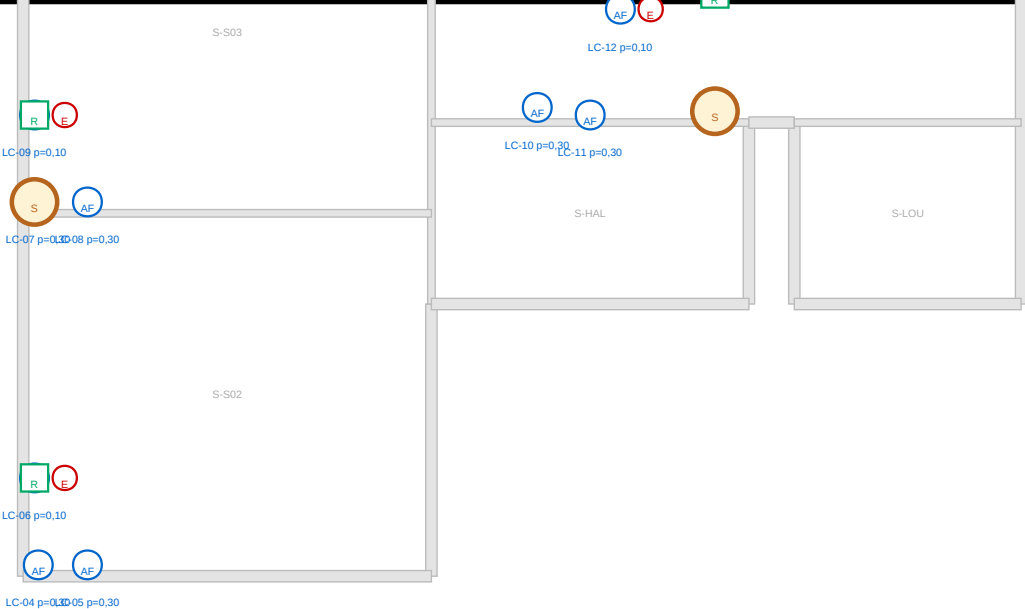
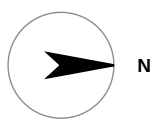
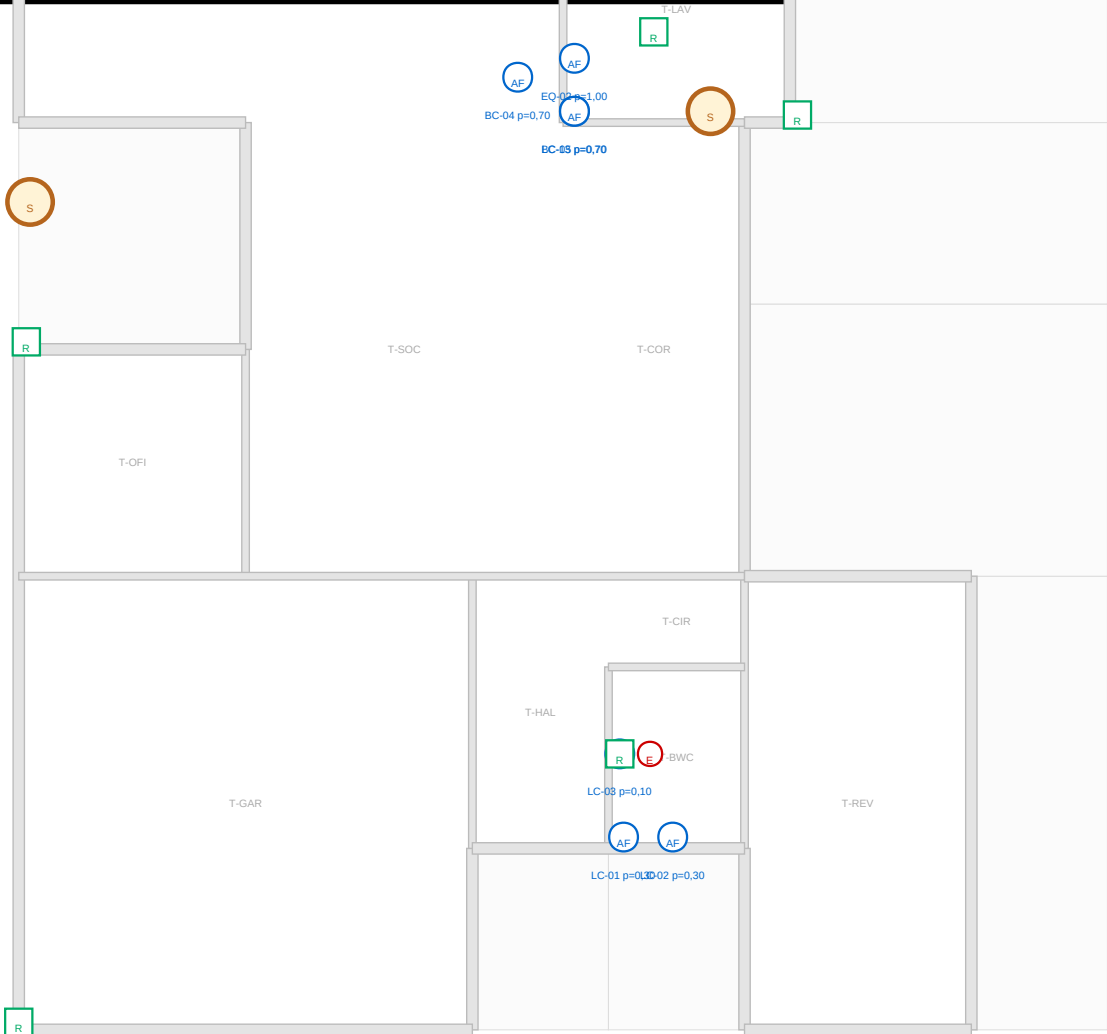


1 PONTOS HIDRAULICOS — TERREO
ESCALA 1:100

DIMENSIONAMENTO — AGUA FRIA E ESGOTO

TRECHO	PECAS	PESOS	Q (L/s)	DN AGUA	V (m/s)	UMC	DN ESGOTO	REGIME
Superior	8	2,10	0,435	DN25	1,19	27	DN200	pressurizado
Terreo	9	4,80	0,884	DN25	1,81	36	DN200	gravidade
GERAL	30	7,90	0,794	DN25	1,31	33	DN200	gravidade

PECAS DE UTILIZACAO

COD	AMB	TIPO	PESO	UMC	DN AF	DN ESS	QUENTE
LC-01	T-800C	W80	0,30	6	DN25	DN20	—
LC-02	T-800C	W80W80	0,30	1	DN25	DN20	—
LC-03	T-800C	Box	0,30	2	DN25	DN20	W80
LC-04	S-800	W80	0,30	6	DN25	DN20	—
LC-05	S-800	W80W80	0,30	1	DN25	DN20	—
LC-06	S-800	Box	0,30	2	DN25	DN20	W80
LC-07	S-800	W80	0,30	6	DN25	DN20	—
LC-08	S-800	W80W80	0,30	1	DN25	DN20	—
LC-09	S-800	Box	0,30	2	DN25	DN20	—

2 PONTOS HIDRAULICOS — SUPERIOR
ESCALA 1:100

DECISOES QUE O DIAMETRO REVELA

DECISAO	CONSEQUENCIA HIDRAULICA
Chuveiro elétrico em vez de aquecimento central	peso 0,02 por chuveiro em vez de 0,40 a soma cai de 0,2 para 7,0 pesos e o alternador de DN20 para DN22
Limite de velocidade por conforto, não por norma	DN25 elevando a norma a 2,37 m/s a 3,0 m/s e tudo não muda. Custa alguns metros de tubo
Pressurizador no ramal superior	0,5 mca por gravidade nos setores chuveiro elétrico, TC-14 entrega 12 mca
Ramais planejados sem ligação a valas	rede de rios e florestamento separada, com cot e identificação próprias. Não há ponto de conexão cruzada possível
Canais de drenagem antes da impermeabilização	canal + TC-11 (DN-1) + TC-12 + rede, DN200 com cobertura de 2%

- NOTAS
- Água fria por metrado dos pesos (DN20) Q = 0,20 + (seção dos pesos) = 0,794 L/s com 7,0 pesos.
 - Alternador DN22 a 1,32 m/s — limitado pelo conforto (2,0 m/s) não pela norma (3,0 m/s).
 - Exigido por LNC (DN20) 33 LNC, tubo de queda DN200, ventilação DN20.
 - Chuveiro 0,40 LTRCO tem peso 0,02, mas 0,40 a decisão de aquecimento requerer água com diâmetro menor em toda a casa.

PROJETO PORTO REAL

RESIDENCIA UNIFAMILIAR (MANAUS - AM) | SUELE TATIANA PI

PROJETO ARQUITETONICO

INSTALACOES HIDROSSANITARIAS

BASE GEOMETRICA	ESCALA	EMISSAO	PROVA
União Consolidada	1:100	ESTUDO PRELIMINAR	26
por R22 (previsão)	FORMATO A1	W80 LIBERADO PARA OBRAS	26
UNIDADE MESTRE: MAN	MAI/24 05/05/2025	SEM ART / RNT	05-25