




● luminária embuída, 3.000 K, RSC 90

□ alçapão técnico 600 x 600 mm

▨ forro absorvente (alfa 0,70)

FORROS POR AMBIENTE

AMBIENTE	SOLUÇÃO	ÁREA	NOTA
T-001	forro absorvente (α=0,70) em todo o pérgo	36,24	único ponto que demanda a instalação de 3,20 x 60
T-002	gesso liso + cantoneira e lapiseira	25,20	abertura para o mobiliário, forro técnico aqui não
T-003	gesso liso + cantoneira	18,00	superfície de fácil limpeza sem necessidade de manutenção
T-004	gesso liso + la mineral sobre o forro	25,80	o forro é forro técnico todo de 3,20 x 60 no pérgo
T-005	gesso liso + la mineral sobre o forro	25,80	idem
T-006	gesso liso + la mineral sobre o forro	25,80	idem
T-007	sem forro (estrutura aparente)	36,00	ambiente semi-escuro, acústica não forçada
T-008	sem forro (estrutura aparente)	9,00	idem
T-009	sem forro (estrutura aparente)	3,00	idem

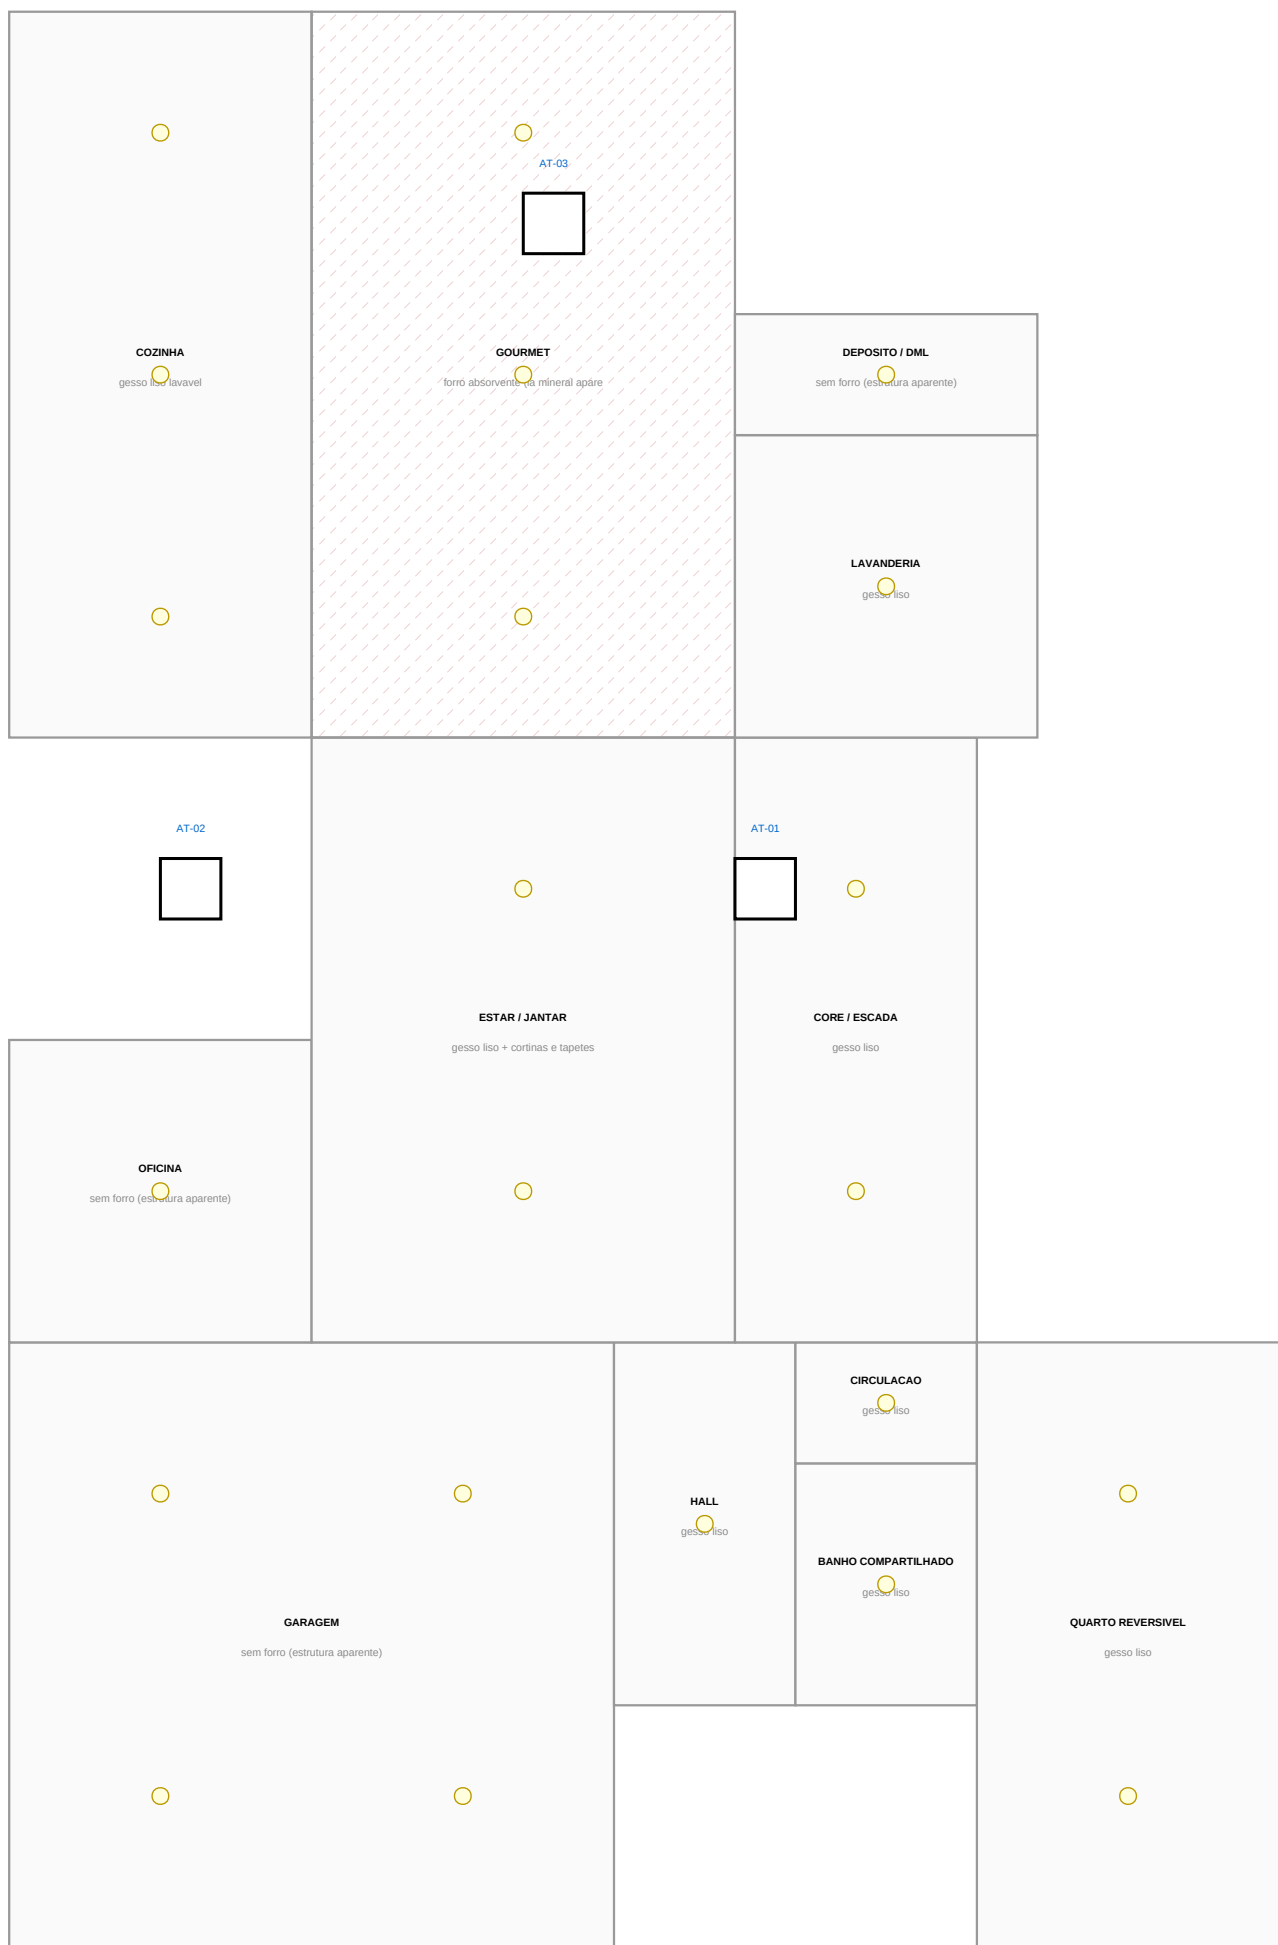

1 FORRO REFLETIDO — TERREO
ESCALA 1:75

NOTAS

- * Planta refletida: vista do forro projetada no plano horizontal.
- * Forro absorvente apenas no gourmet — único ponto com necessidade crítica.
- * Alçapão técnico de 600 x 600 mm, passando de cobertura de 600 mm.
- * Luminária para 3.000 K, RSC 90.

PROJETO PORTO REAL

RESIDÊNCIA UNIFAMILIAR (MANAUS - AM) | SOUZA TATIANA-PS

PROJETO ARQUITETÔNICO

PLANTA DE FORRO E ILUMINAÇÃO

BASE GEOMÉTRICA	ESCALA	EMISSÃO	PROVA
Unidade Consolidada	1:75	ESTUDO PRELIMINAR RSI	16
RSI-PSZ (previsão)	FORMATO A1	IMÓVEL LIBERADO PARA OBRAS	
UNIDADE MÉTRICA: mm	MAQUETA: 600/600/300	SEM ART / RNT	06-28 REV 01