


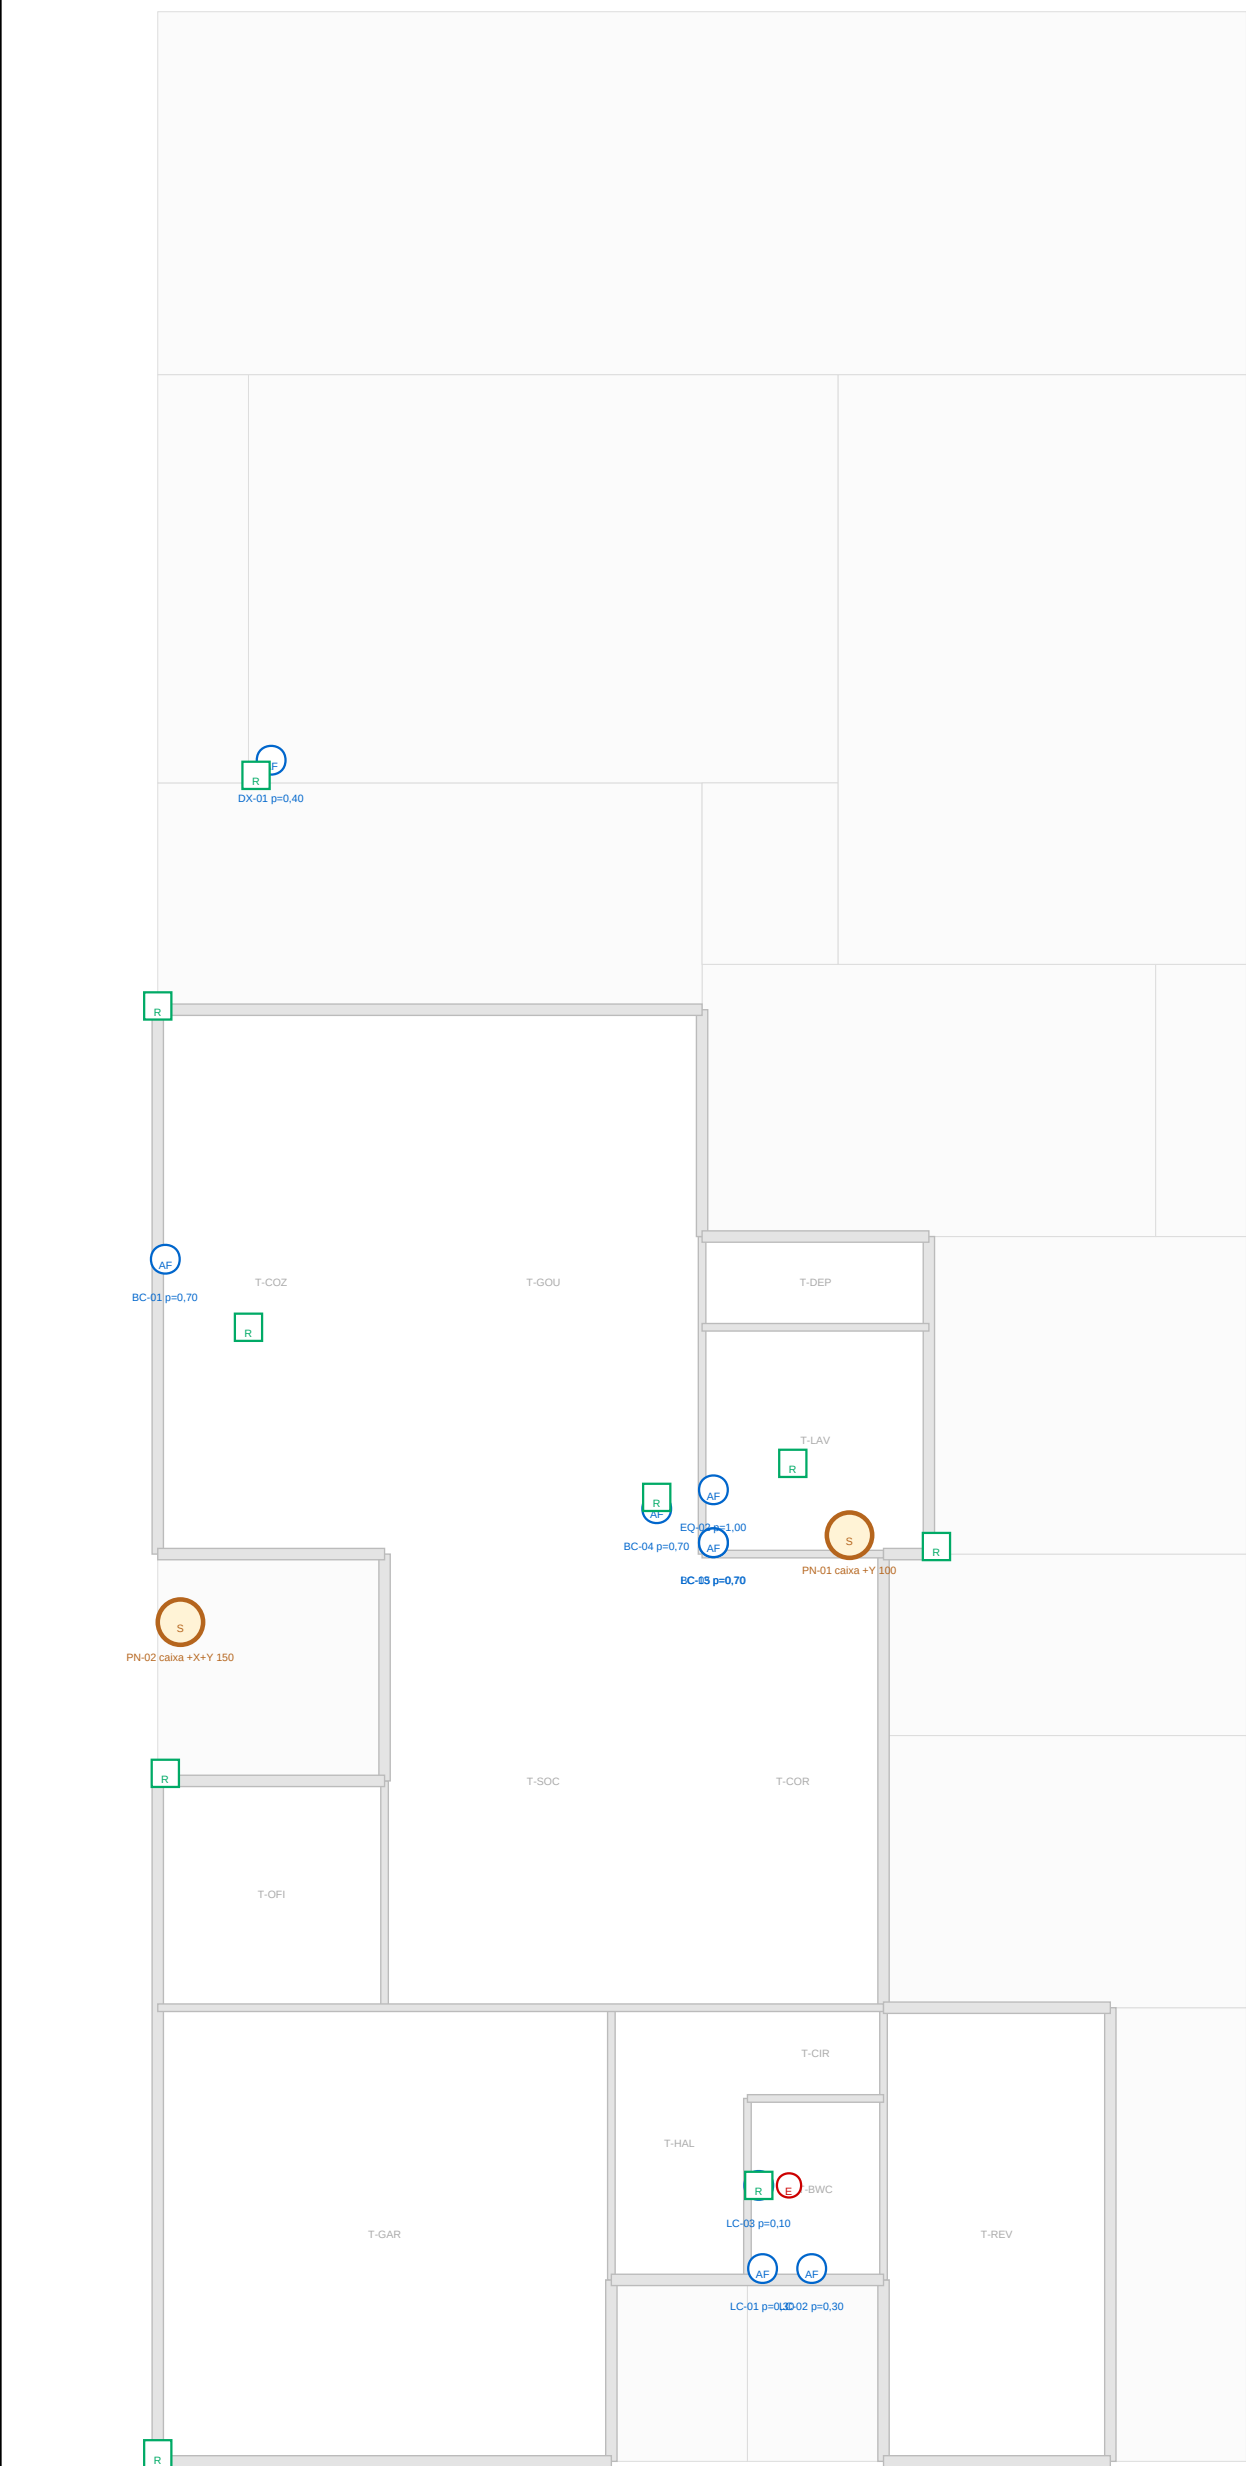


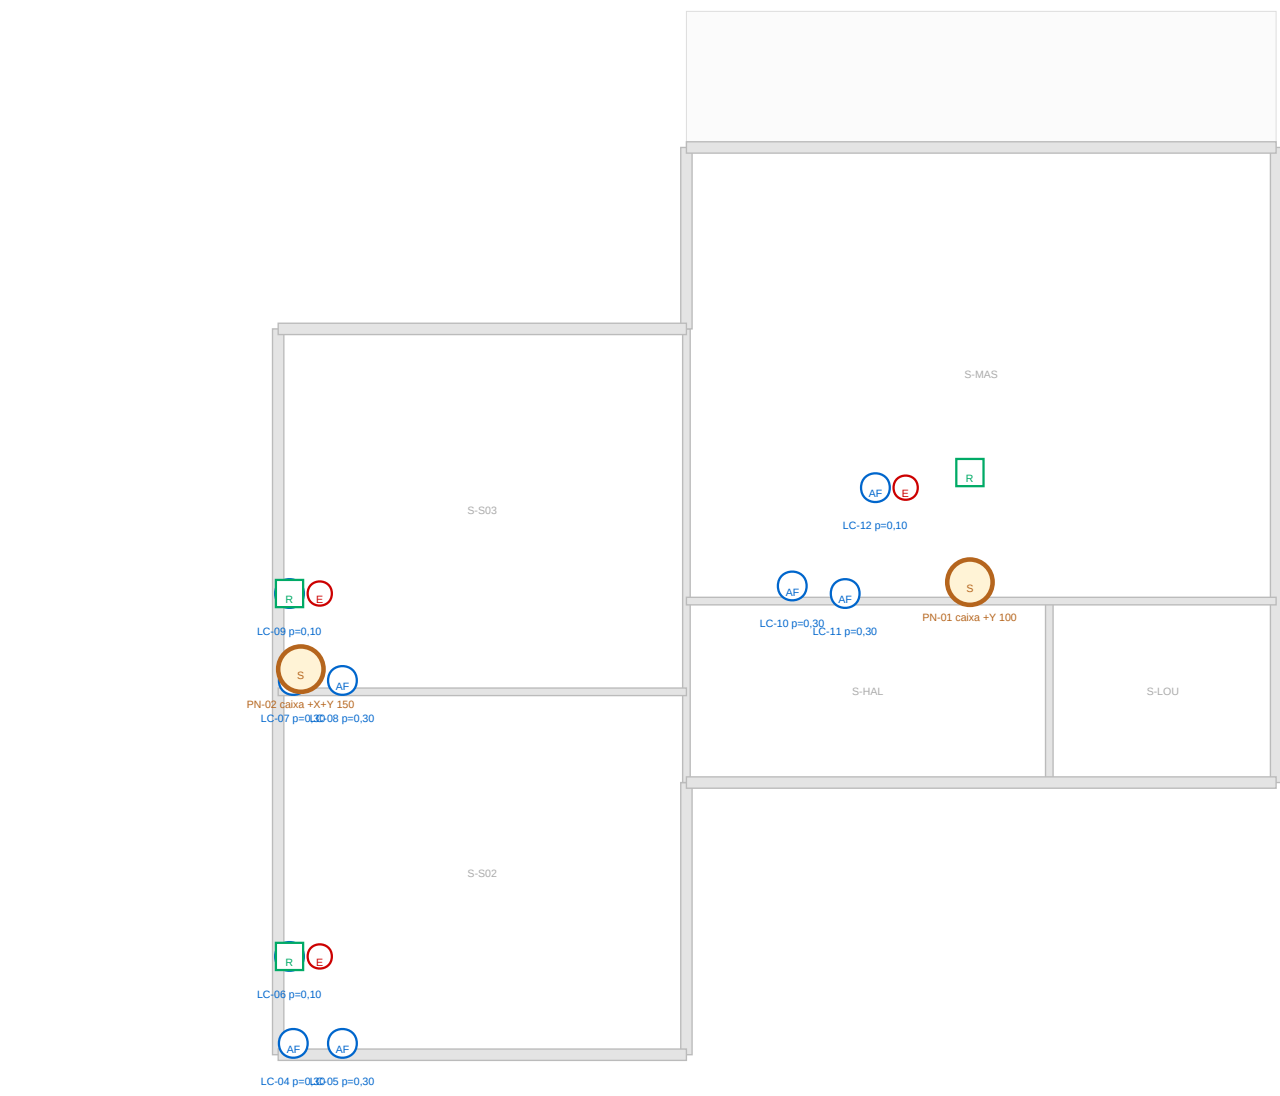

1 PONTOS HIDRAULICOS — TERREO
ESCALA 1:100

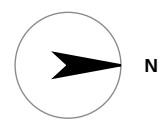

2 PONTOS HIDRAULICOS — SUPERIOR
ESCALA 1:100

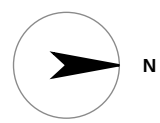

TRECHO	PECAS	PESOS	Q (L/s)	DN AGUA	V (m/s)	UMC	DN ESGOTO	REGIME
Superior	8	2,10	0,435	DN25	1,19	27	DN100	pressurizado
Terreo	9	4,80	0,884	DN25	1,81	36	DN100	gravidade
GERAL	30	7,00	0,794	DN32	1,31	33	DN100	gravidade

COD	AMB	TIPO	PESO	UMC	DN AF	DN ESG	QUENTE
LC-01	T-001C	vaso	0,30	6	DN25	DN40	—
LC-02	T-001C	lavatório	0,30	1	DN25	DN40	—
LC-03	T-001C	box	0,30	2	DN25	DN40	sim
LC-04	S-002	vaso	0,30	6	DN25	DN40	—
LC-05	S-002	lavatório	0,30	1	DN25	DN40	—
LC-06	S-002	box	0,30	2	DN25	DN40	sim
LC-07	S-003	vaso	0,30	6	DN25	DN40	—
LC-08	S-003	lavatório	0,30	1	DN25	DN40	—
LC-09	S-003	box	0,30	2	DN25	DN40	sim

COD	AMB	TIPO	PESO	UMC	DN AF	DN ESG	QUENTE
LC-01	S-005	vaso	0,30	6	DN25	DN40	—
LC-02	S-005	lavatório	0,30	1	DN25	DN40	—
LC-03	S-005	box	0,30	2	DN25	DN40	sim
LC-04	T-LAV	vaso	0,30	3	DN25	DN40	—
LC-05	T-LAV	lavatório	0,30	3	DN25	DN40	—
LC-06	T-LAV	box	0,30	3	DN25	DN40	sim
LC-07	T-LAV	vaso	0,30	3	DN25	DN40	—
LC-08	T-LAV	lavatório	0,30	3	DN25	DN40	—
LC-09	T-LAV	box	0,30	3	DN25	DN40	sim

DECISAO	CONSEQUENCIA HIDRAULICA
Chuveiro elétrico em vez de aquecimento central	peso 0,02 por chuveiro em vez de 0,40 a soma cai de 8,2 para 7,0 pesos e o alimentador de DN40 para DN32
Limite de velocidade por conforto, não por norma	DN32 elevando a soma a 2,07 m/s a 3,0 m/s e não nas bocais. Causa alguns metros de tubo
Pressurizador na rede superior	0,5 mca por gravidade nas setores chuveiro elétrico, TC-14 entrega 12 mca
Redes pluviais sem ligação a valas	rede de rede e fisicamente separada, com cot e identificação próprias, não há pontos de conexão cruzada possíveis
Canal de grelhas antes da inspeção	cota 10 + TC-11 (DN-1) + TC-12 = rede, DN100 com cobertura de 2 m

NOTAS

- Água fria por rede de dois pesos (DN25) Q = 0,20 e rede de dois pesos = 0,794 L/s com 7,0 pesos.
- Alimentador DN32 a 1,12 m/s — limitado pelo conforto (2,0 m/s) não pela norma (3,0 m/s).
- Exigido por LNC (DN25) 33 LNC, tubo de queda DN100, ventilação DN80.
- Chuveiro ELA TRACO tem peso 0,02, mas 0,40 a decisão de aquecimento requerer água quente diâmetro menor em toda a casa.

PROJETO PORTO REAL

RESIDENCIA UNIFAMILIAR (MANSÃO - AM) | SOUS TATIANA-PS

PROJETO ARQUITETONICO

INSTALACOES HIDROSSANITARIAS

BASE GEOMETRICA

União Consolidada

Projeto (previsão)

UNIDADE MESTRE: AM

ESCALA

1:100

FORMATO A1

MALHA 600/600/600

EMISSAO

ESTUDO PRELIMINAR RSI

NAO LIBERADO PARA OBRA

SEM ART / RNT

PROVACA

26

06-28 REV RSI