


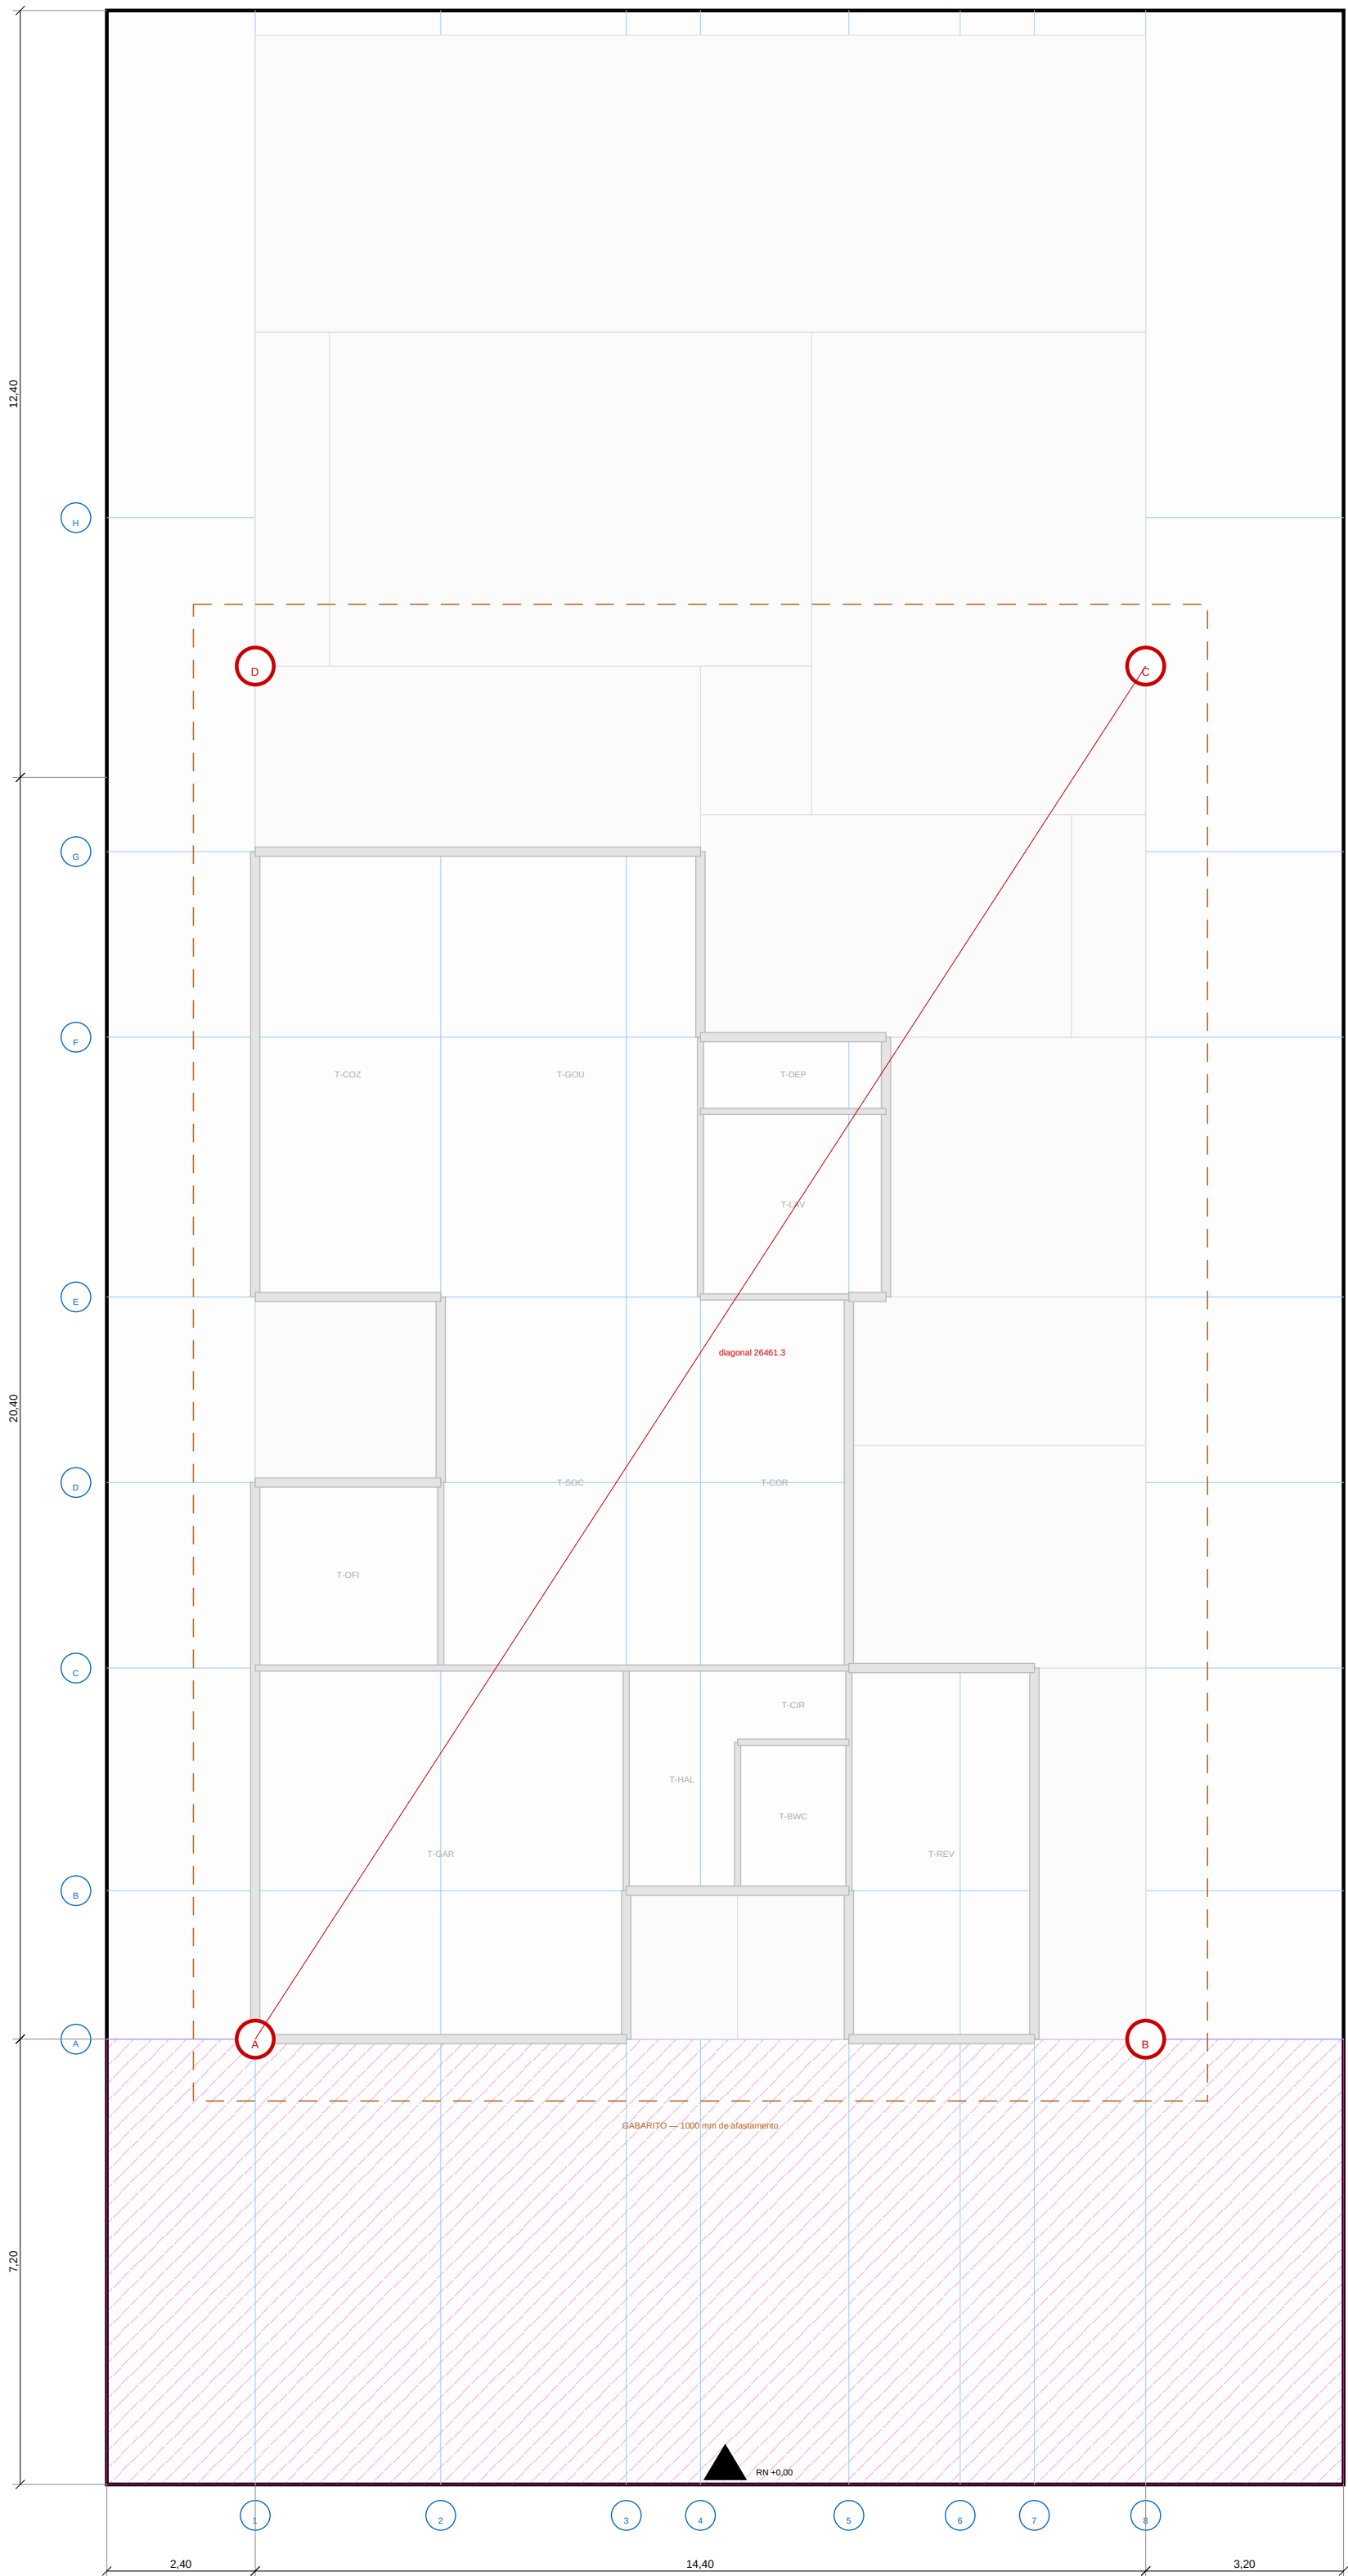

COORDENADAS DOS CANTOS (mm)

CANTO	X	Y	DISSA-ALA	DISSA-NORTE	TESTADA	FORNO	DIAGONAL
A	2400	7200	2400	17600	7200	32800	26461,3
B	18800	7200	18800	3200	7200	32800	26461,3
C	18800	28400	18800	3200	28400	19600	26461,3
D	2400	28400	2400	17600	28400	19600	26461,3

PROCEDIMENTO DE LOCACAO

#	PASSO	CRITERIO DE ACABO
1	Conferir as divisões com a malha e o memorial de lote	divergência acima de 10 mm interromper a locação
2	Instalar o PNM: marcos de concreto 200 x 200 x 100 mm, fora da área de obra	fora da área de obra
3	Montar o gabarito a 1000 mm do cantoneiro	perguntas 75 x 75 e tubos 20 x 100
4	Marcar os eixos X (1) e Y (1) a 10 m no gabarito	linha coordenada múltipla de 200 mm
5	Colar cado canto dos OLAS diretos	verificar em cado: erro de cado de soma
6	Conferir a diagonal A-C	26461,3 mm com tolerância de 20 mm
7	Conferir o quadrado por 3-4-5 em cada canto	antes de qualquer concretagem
8	Registrar em ata com foto e modelo	gabarito continuo nos dois lados da obra, conferência

EIXOS MODULARES

DIRECAO	PROJECAO (mm)
X (1) e Y (1)	2400 - 5400 - 9400 - 13400 - 17400 - 21400 - 25400
Y (1) e X (1)	7200 - 9400 - 11600 - 13800 - 16000 - 18200 - 20400 - 22600 - 24800
Malha	principal 600 mm - subgrid 300 mm
Origem	canto frontal esquerdo do lote
Unidade	milímetros

NOTAS

- Locação é o único documento em que o erro não tem contorno técnico: o caso se dá do lugar.
- Cada canto é o cado dos OLAS diretos, nunca em cado acumulados — erro de cado de soma, erro de referência independente não.
- Conferência obrigatória pela diagonal 26461,3 mm entre A e C antes de concretar o malho.
- Ata no ato de locação, assinada por todos os envolvidos (TC-OB, cado OLAS) e pelo acoberto do terreno.

PROJETO PORTO REAL

RESIDENCIA UNIFAMILIAR (MANAUS - AM) | SOUZA TATIANA-PS

PROJETO ARQUITETONICO

LOCACAO DE OBRA E GABARITO

BASE GEOMETRICA Linha Consolidada Projeto (previsão) UNIDADE: METRO (m)	ESCALA 1:100 FORMATO A1 MALHA: 600/300/300	DISSAÇÃO ESTUDO PRELIMINAR RSL Linha LIBERADA PARA OBRA SEM ART / RNT	PROJECÇÃO 31 06-28 REV RSL
--	--	--	---