
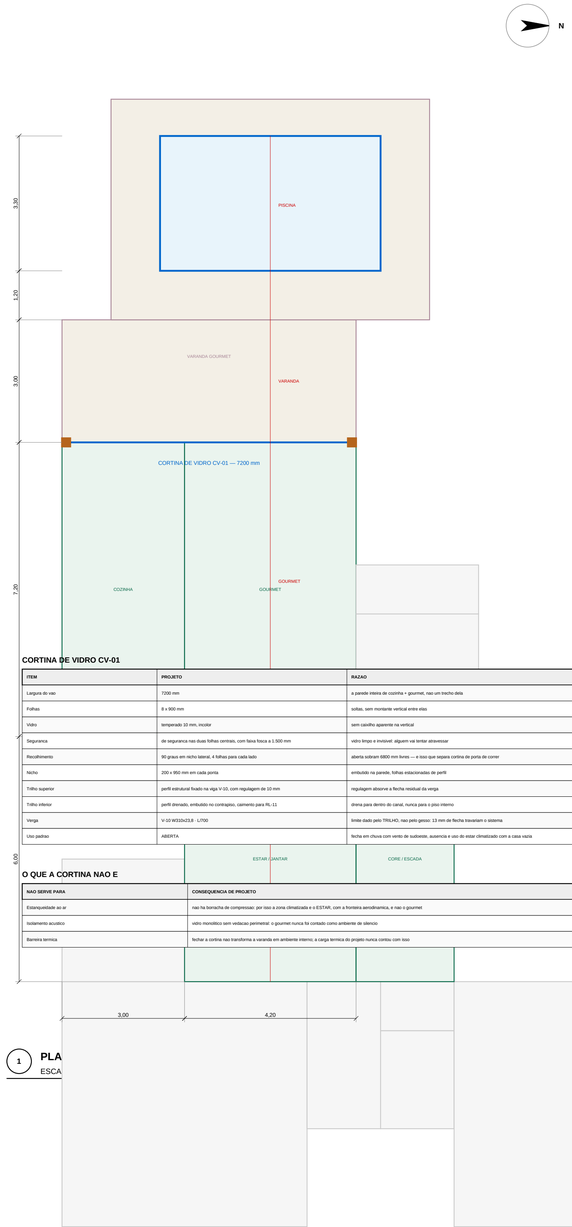


1 PLA
ESCA

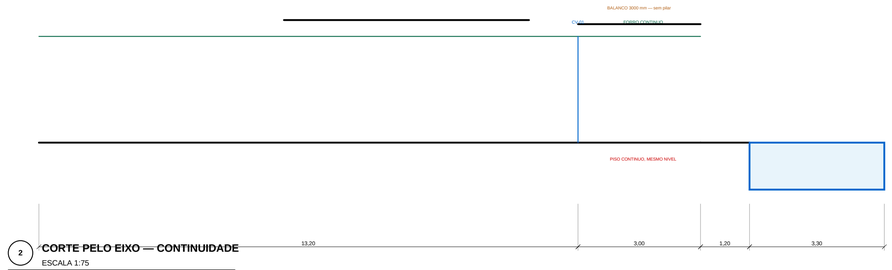

2 CORTE PELO EIXO — CONTINUIDADE
ESCALA 1:75

CORTINA DE VIDRO CV-01

ITEM	PROJETO	RAZAO
Largura do vao	7200 mm	a parede inteira de cozinha + gourmet, nao um trecho dela
Folhas	8 x 900 mm	soltas, sem montante vertical entre elas
Vidro	temperado 10 mm, incolor	sem caixilho aparente na vertical
Seguranca	de seguranca nas duas folhas centrais, com faixa fosca a ≥ 500 mm	vidro limpo e invisivel: alguem vai tentar atravessar
Recolhimento	90 graus em nicho lateral, 4 folhas para cada lado	aberta sobram 6800 mm livres — e isso que separa cortina de porta de correr
Nicho	200 x 950 mm em cada ponta	embutido na parede, folhas estacionadas de perfil
Trilho superior	perfil estrutural fixado na viga V-10, com regulagem de 10 mm	regulagem absorve a flecha residual da verga
Trilho inferior	perfil rebaixado, embutido no contrapiso, caimento para RL-11	drena para dentro do canal, nunca para o piso interno
Verga	V-10 W310x23,8 - L=700	limite dado pelo TRELHO, nao pelo gesso: 13 mm de flecha travariam o sistema
Uso padrao	ABERTA	fecha em chuva com vento de sudoeste, ausencia e uso do estar climatizado com a casa vazia

O QUE A CORTINA NAO E

NAO SERVE PARA	CONSEQUENCIA DE PROJETO
Estanqueidade ao ar	nao ha borracha de compressao: por isso a zona climatizada e o ESTAR, com a fronteira aerodinamica, e nao o gourmet
Isolamento acustico	vidro monolitico sem vedacao perimetral: o gourmet nunca foi contado como ambiente de silencio
Barreira termica	fechar a cortina nao transforma a varanda em ambiente interno; a carga termica do projeto nunca contou com isso

AS TRES MEDIDAS QUE FAZEM A INTEGRACAO FUNCIONAR

MEDIDA	PROJETO	SE ERRAR
Desnivel de piso na soleira	0 mm	qualquer degrau e ido como limite: o olho passa a ver dois ambientes, nao um
Paginacao atravessando a linha	sim — mesma malha ZP-1 dentro e fora	junta desalinhada na soleira denuncia a costura exatamente onde nao ha parede para disfarcar
Forro continuo sobre o trilho	sim	forro interrompido no vao devolve a leitura de porta
Bancada fora da linha da vista	BC-04 foi para a parede teste	a bancada estava encostada no fundo ocupando 3.900 dos 4.200 mm: era ela, e nao a esquadria, o que tapava a piscina
Profundidade da varanda	3000 mm	com 1.200 mm nao se usa o espaco durante chuva, que era o objetivo declarado
Piscina no eixo	0 mm de desalinhamento	piscina fora do eixo transforma a abertura em janela para o lado

O EIXO, EM NUMEROS

TRECHO	COTA Y	PROFUNDIDADE ACUMULADA
Inicio do estar	13200 mm	0
Cozinha e gourmet (integrados)	19.200 mm	6,00 m
Cortina de vidro CV-01	26400 mm	13,20 m
Borda da varanda coberta	29400 mm	16,20 m
Borda da piscina	30600 mm	17,40 m
Fim da piscina	33900 mm	20,70 m

NOTAS

- Cozinha e gourmet sao UM ambiente de 51,84 m2, sem parede entre eles, abrindo por 7200 mm de cortina de vidro.
- Aberta, a cortina deixa 6800 mm livres: as folhas giram 90 graus e estacionam de perfil nos nichos das duas pontas.
- Varanda de 3000 mm em balanco — nenhum pilar entre a mesa e a agua.
- Eixo continuo de 20,7 m do estar ao fim da piscina, com 0 mm de desalinhamento.

PROJETO PORTO REAL

RESIDENCIA UNIFAMILIAR | MANAUS - AM | SUB TARUMA (H)

PROJETO ARQUITETONICO

EIXO SOCIAL — COZINHA, GOURMET, CORTINA DE VIDRO E PISCINA

BASE GEOMETRICA	ESCALA	EMISSAO	PRANCHA
Lista Consolidada pos-R32 (prevalece)	indicada FORMATO A1 MALHA 600/3000/150	ESTUDO PRELIMINAR RS1 NAO LIBERADO PARA OBRA SEM ART / RRT	35 de 36 REV RS1

UNIDADE MESTRE: mm