



VERIFICACAO NBR 9050

| ITEM                      | EXISTIDO            | PROJETO                     |          |
|---------------------------|---------------------|-----------------------------|----------|
| Vel. livre de porta       | 800 mm              | 940 mm (altura de 900)      | OK       |
| Circulo de giro 360 graus | 1.500 mm            | hall, banheiro e quarto     | OK       |
| Desnivel sem rampas       | até 5 mm            | soluções niveladas          | OK       |
| Largura de circulação     | 900 mm              | 1.800 mm no hall            | OK       |
| Barras de apoio           | relívato previsto   | instaladas na PTE 1 e PTE 2 | OK       |
| Barrameda acessível       | altura livre 750 mm | sem obstáculos até a calha  | OK       |
| Contraste e interruptor   | 600 a 1.000 mm      | a definir no eletrico       | pendente |

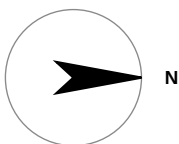

FLUXOS — SEPARACAO DE CIRCUITOS

| CIRCUITO        | PERCURSO                                                  | CIRCULO SOCIAL? |
|-----------------|-----------------------------------------------------------|-----------------|
| Servico         | garagem -> oficina -> lavanderia -> cozinha -> despensa   | NAO             |
| Social          | entrada -> hall -> estar -> gourmet -> alameda -> piscina | —               |
| Intimo Intimo   | hall -> banheiro compartilhado -> quarto compartilh       | NAO             |
| Intimo Superior | hall -> cora -> hall superior -> suíte                    | NAO             |
| Uso e carga     | cozinha -> despensa -> reserv. sal                        | NAO             |

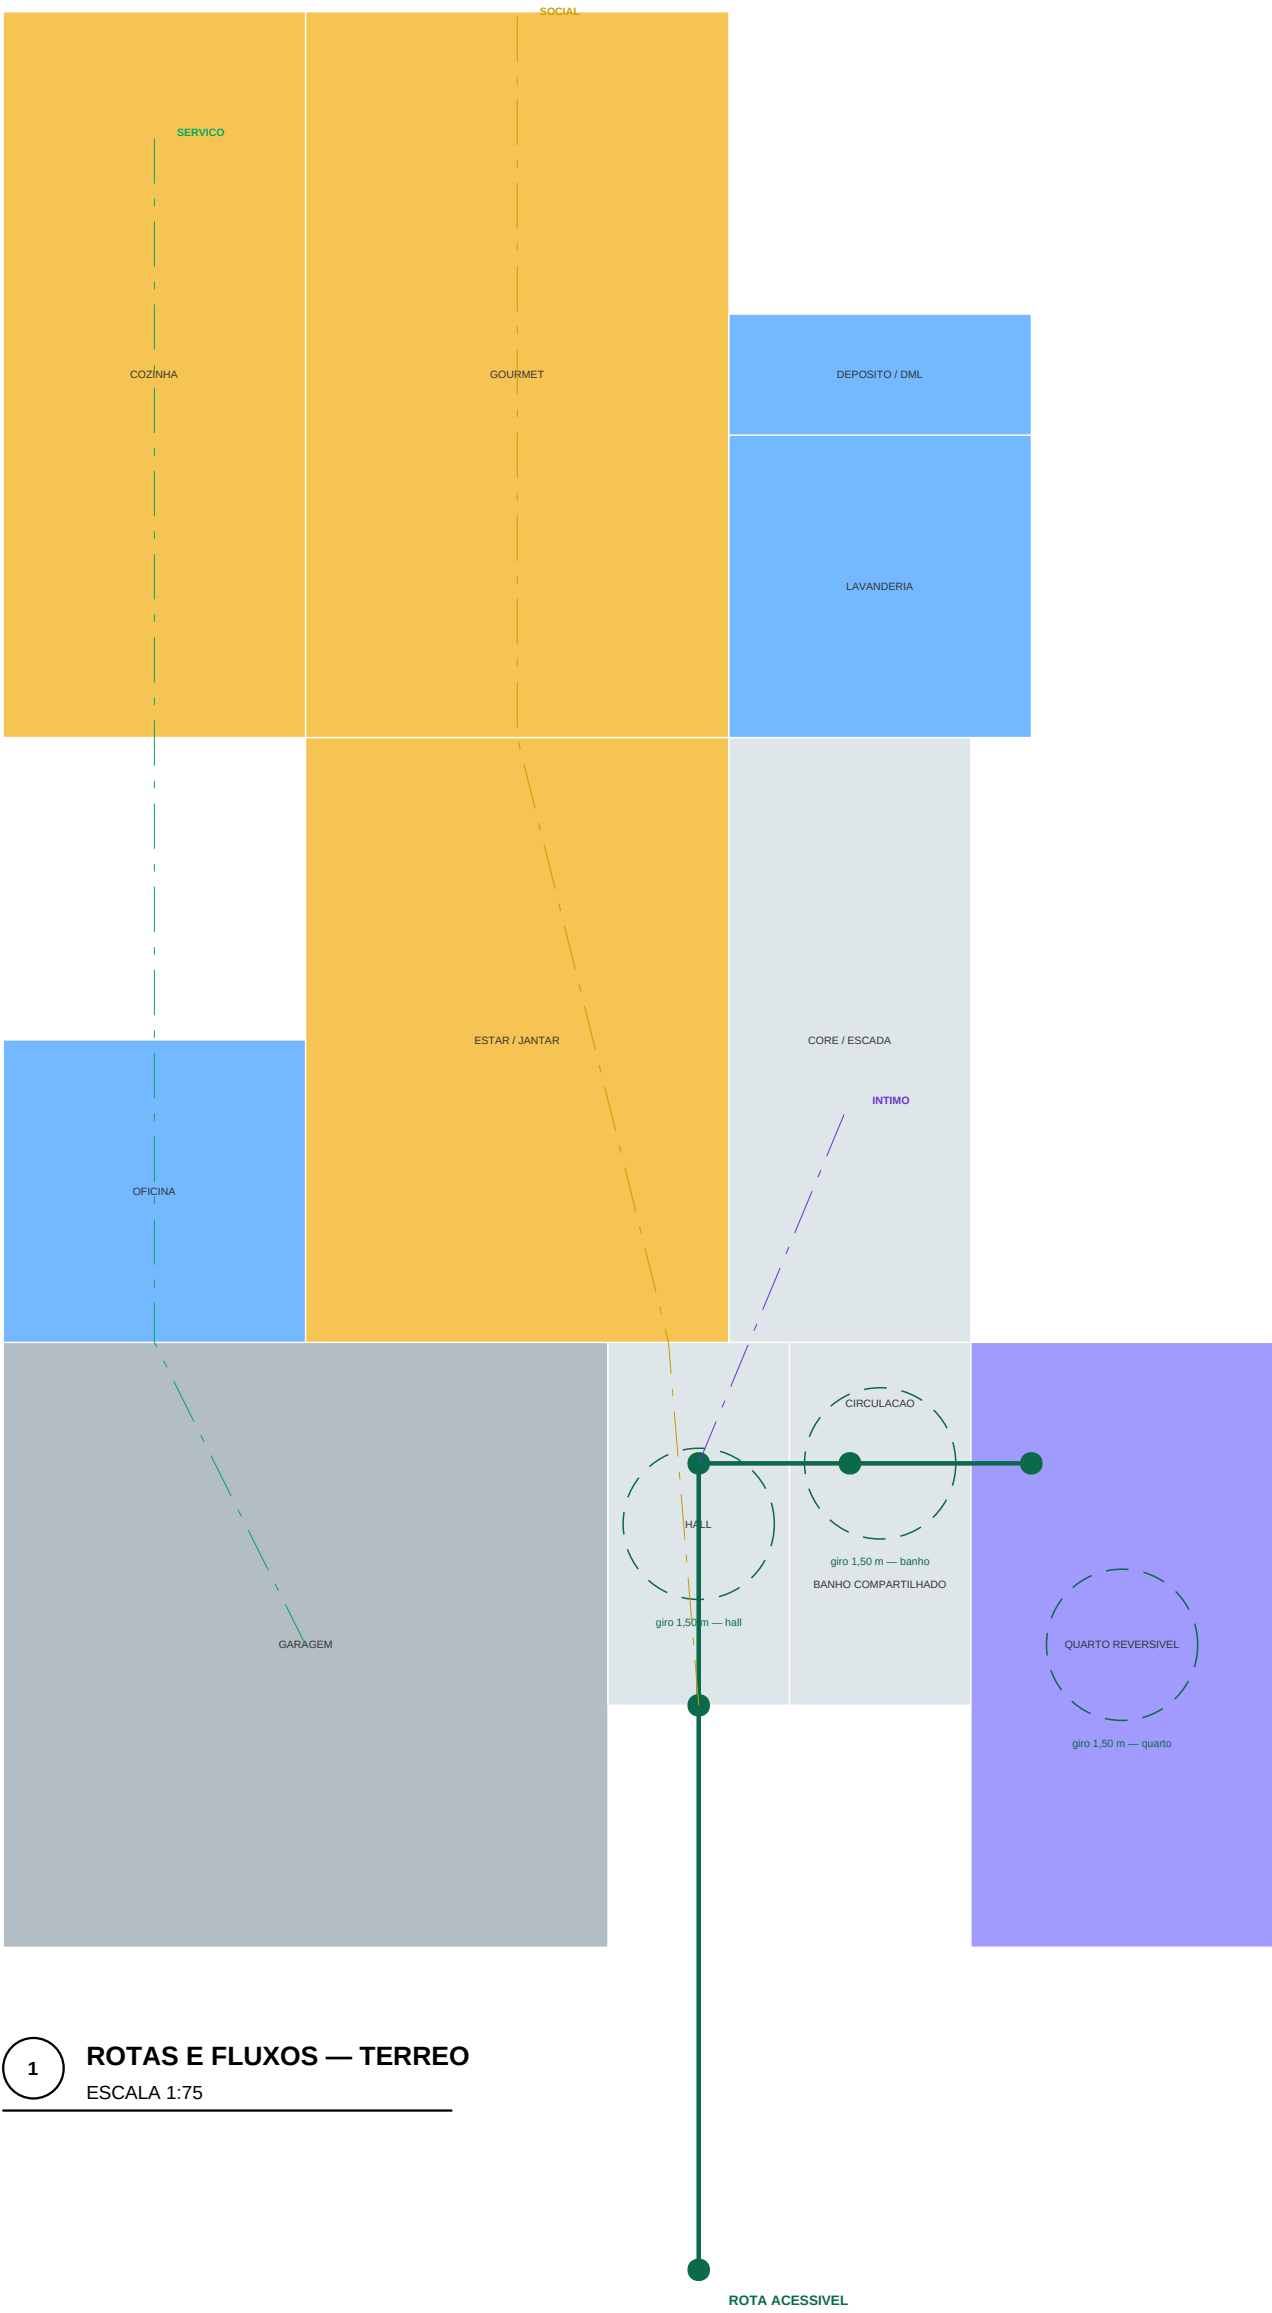

- NOTAS
- \* Rota acessível do passeio ao quarto reservado e ao banheiro compartilhado.
  - \* Circulo de giro de 1.500 mm verificado nos pontos de manobra.
  - \* Porta de correr de 900 mm no banheiro libera a área de manobra.
  - \* Reforços para barras de apoio instaladas antes do fechamento das placas.

PROJETO PORTO REAL

RESIDENCIA UNIFAMILIAR (MANAUS - AM) | SUELE TATIANA-PS

PROJETO ARQUITETONICO

ACESSIBILIDADE E FLUXOS

|                      |                   |                        |              |
|----------------------|-------------------|------------------------|--------------|
| BASE GEOMETRICA      | ESCALA            | EMISSAO                | PROVA        |
| União Consolidada    | 1:75              | ESTUDO PRELIMINAR R39  | 17           |
| ISO-R32 (previsível) | FORMATO A1        | NAO LIBERADO PARA OBRA |              |
| UNIDADE MESTRE: 040  | MAI/24 05/05/2025 | SEM ART / RNT          | 05-25 REV-03 |