


VERIFICACAO URBANISTICA (H)

PARAMETRO	PROJETO	LIMITE	
Taxa de ocupação	31,14 %	max 50 %	OK
Coeff. de aproveitamento	0,370	max 1,00	OK
Galvao	2 pavimentos	max 4	OK
Recuo frontal	7200 mm	conforme 50,00 [4]	OK
Recuo lateral esq.	2400 mm	sem limite no lado	OK
Recuo lateral dir.	3000 mm	max 3000 mm	OK
Recuo de fundo	13800 mm	max 5000 mm	OK

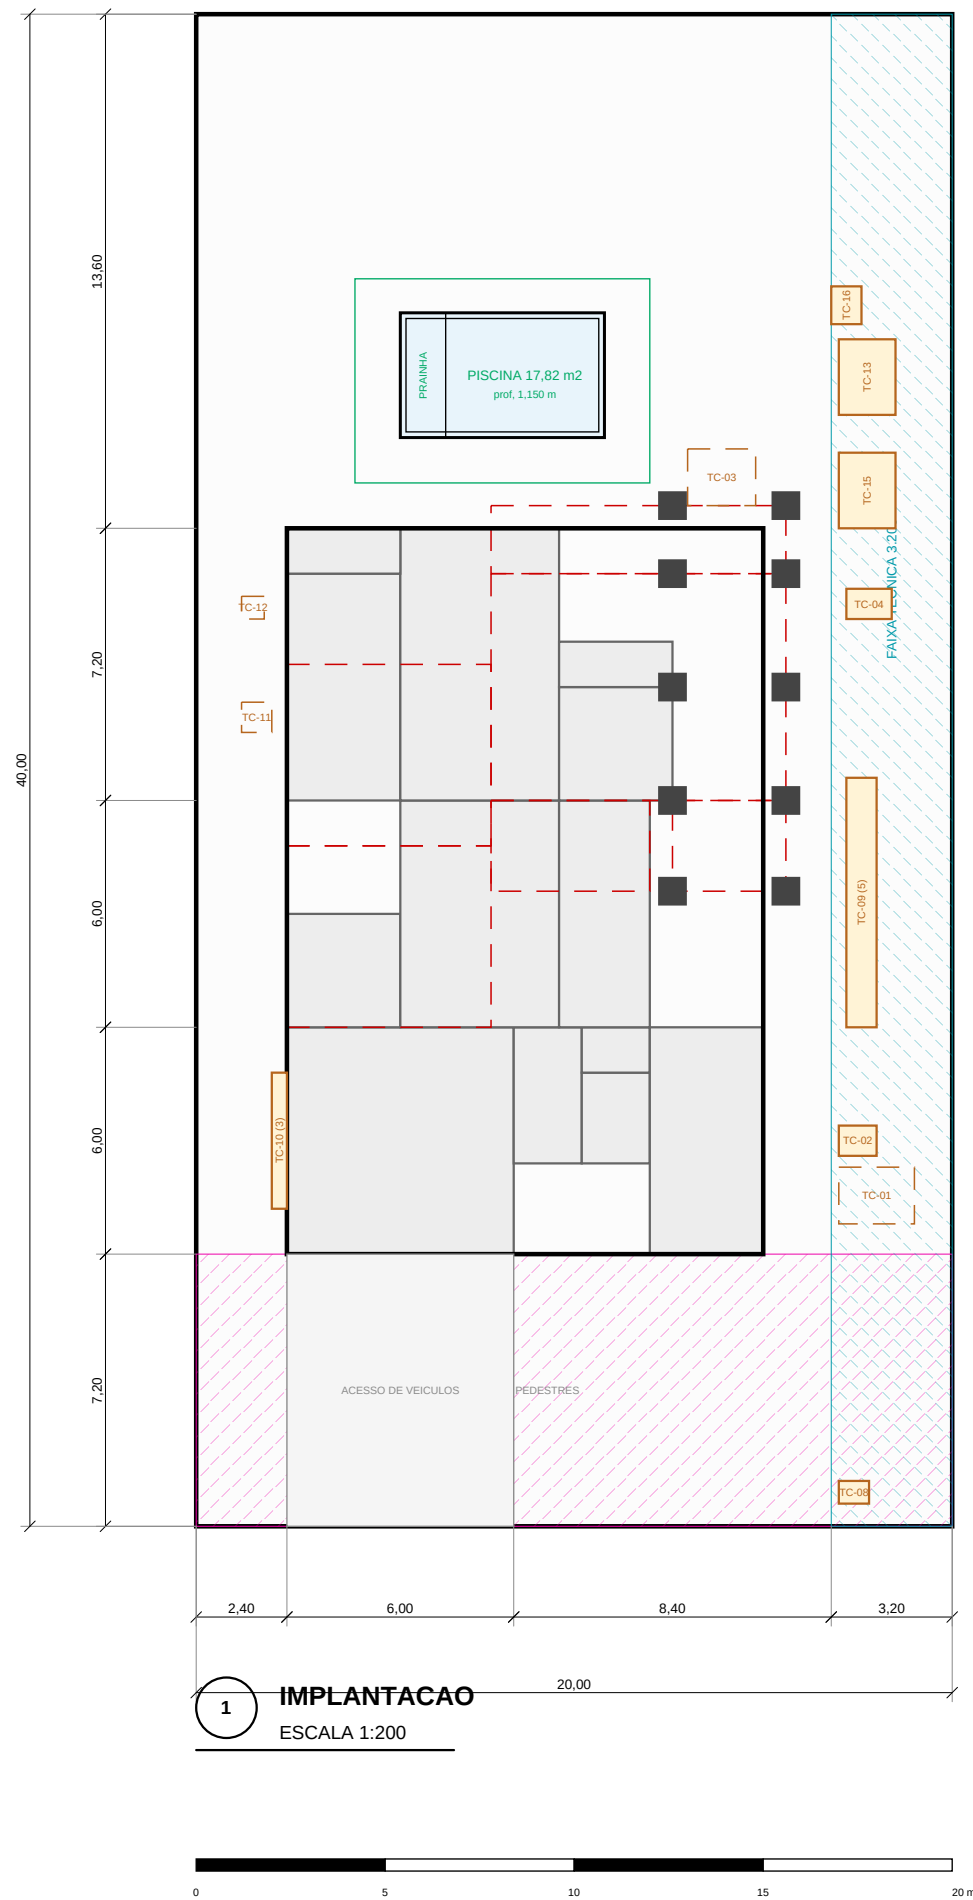

- NOTAS
- * Lote 25.000 x 40.000 m² = 800.000 m².
 - * Recuo: frontal 7.200 / lateral esq. 2.400 / lateral dir. 3.000 / fundo 13.800 mm.
 - * Parametros do SUD Tatuá/Tatuá-Açu sem topografia [H] - pendentes controlados de uso do solo.
 - * Sem muro frontal, mural lateral e de fundo 0 x 2.000 mm.

PROJETO PORTO REAL

RESIDENCIA UNIFAMILIAR (MANSÃO - AM) | SOUS TATUÁ-PA

PROJETO ARQUITETONICO

IMPLANTACAO E SITUACAO

BASE GEOMETRICA Linha Consolidada Projeto (previsão) UNIDADE: METROS - MM	ESCALA 1:200 FORMATO: A1 MILHA 465/500/500	EMISSAO ESTUDO PRELIMINAR LADO LIBERADO PARA DRENA SEM ART / RNT	PROJECION 01 01/24
--	--	---	---------------------------------