


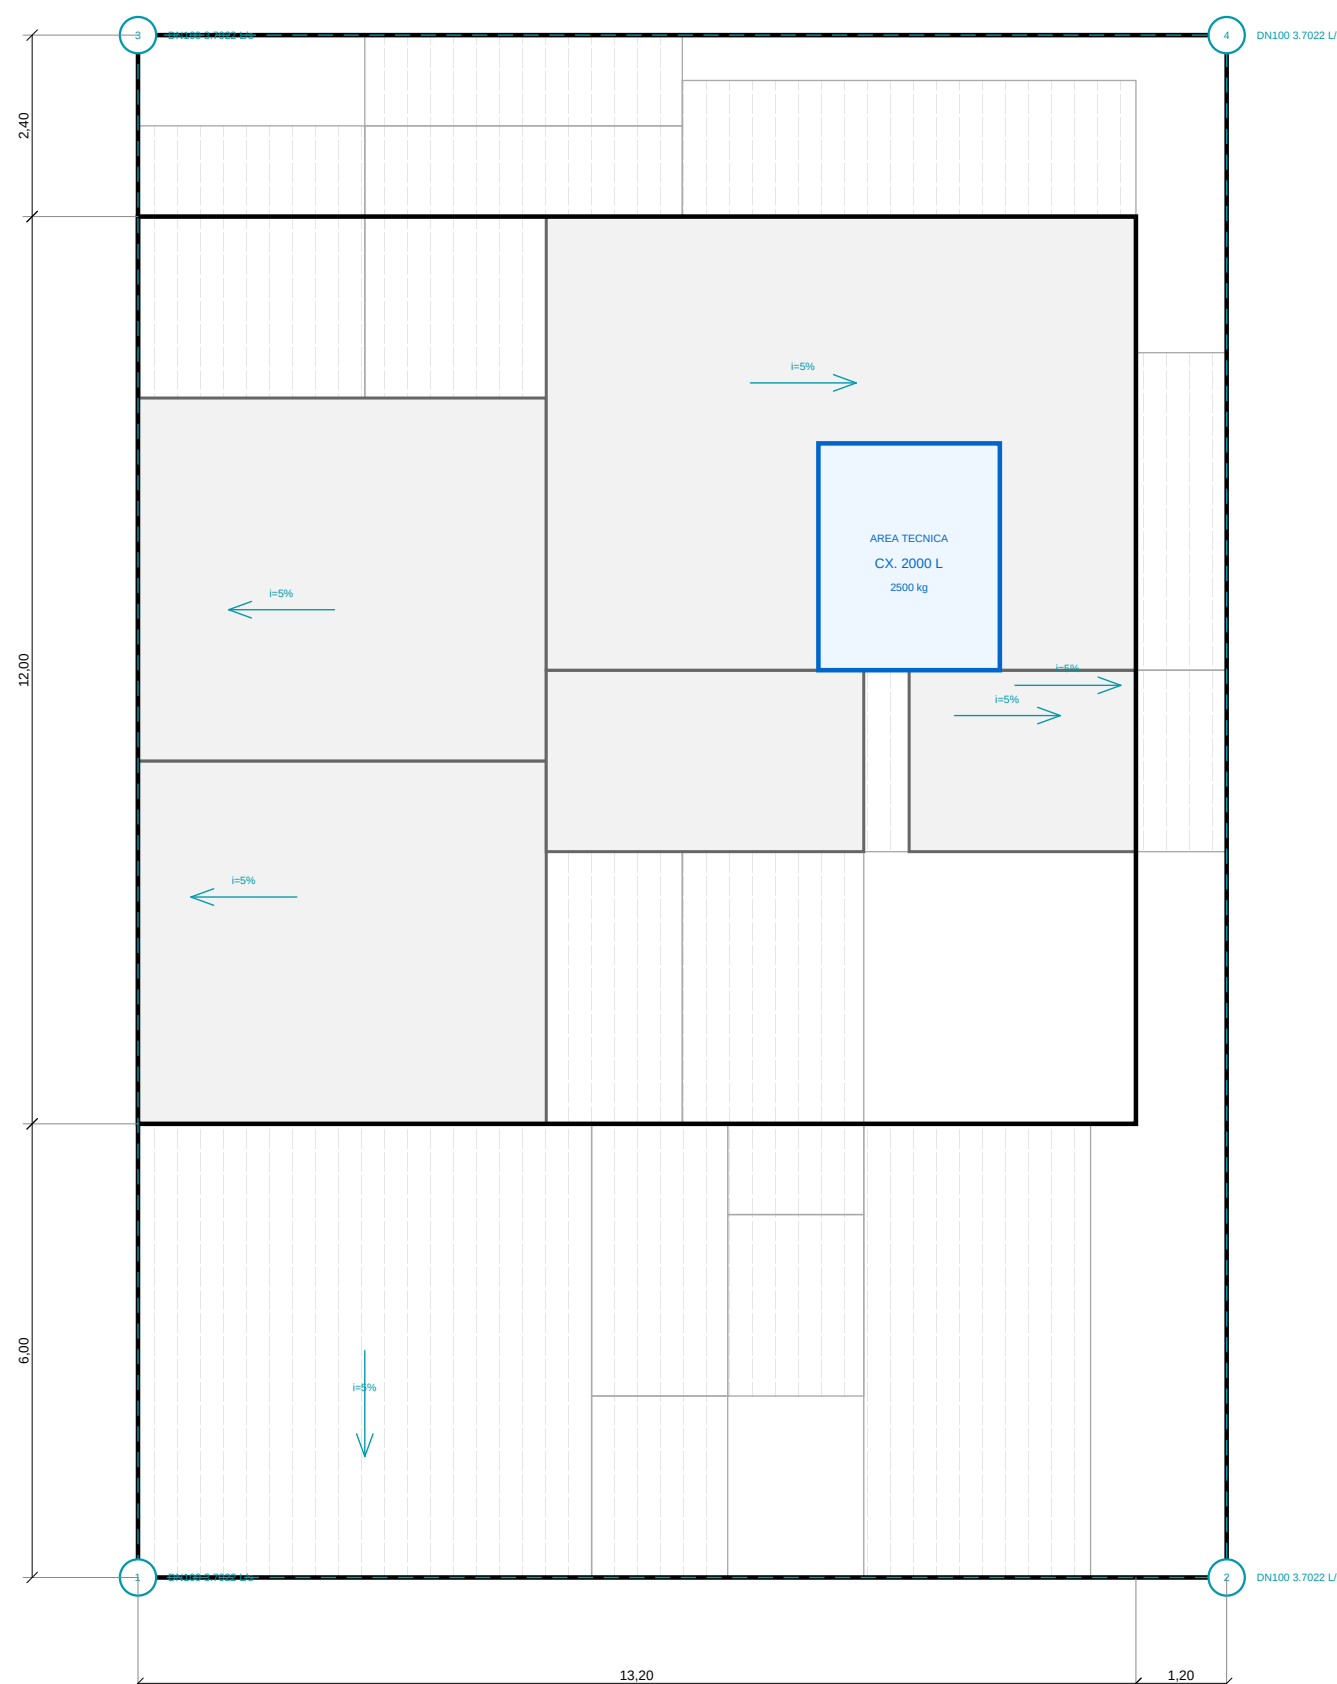

1 COBERTURA  
ESCALA 1:100



- NOTAS
- Plafond sandbach PPR 75 mm, inclinação 5 %.
  - Calha externa 120x120 mm, 4 bocanais Ø100.
  - Contribuição 312,76 m<sup>2</sup> (+ 100 mm) C = 9,39 = Q = 14.808 Lt.
  - Reservatório de retenção pluvial 2.000 L. --> irrigação e lavagem, sem ligação a rede pública.

PROJETO PORTO REAL

RESIDÊNCIA UNIFAMILIAR (MANSÃO - AM) | SOUS TATIANA-PS

PROJETO ARQUITETÔNICO

PLANTA DE COBERTURA

| BASE GEOMÉTRICA    | ESCALA            | EMISSÃO                    | PROJETO |
|--------------------|-------------------|----------------------------|---------|
| União Consolidada  | 1:100             | ESTUDO PRELIMINAR          | 05      |
| Projeto (previsão) | FORMATO A1        | IMÓVEL LIBERADO PARA OBRAS |         |
| UNIDADE MESTRE: AM | MALHA 600/600/300 | SEM ART / RNT              | 05-24   |