


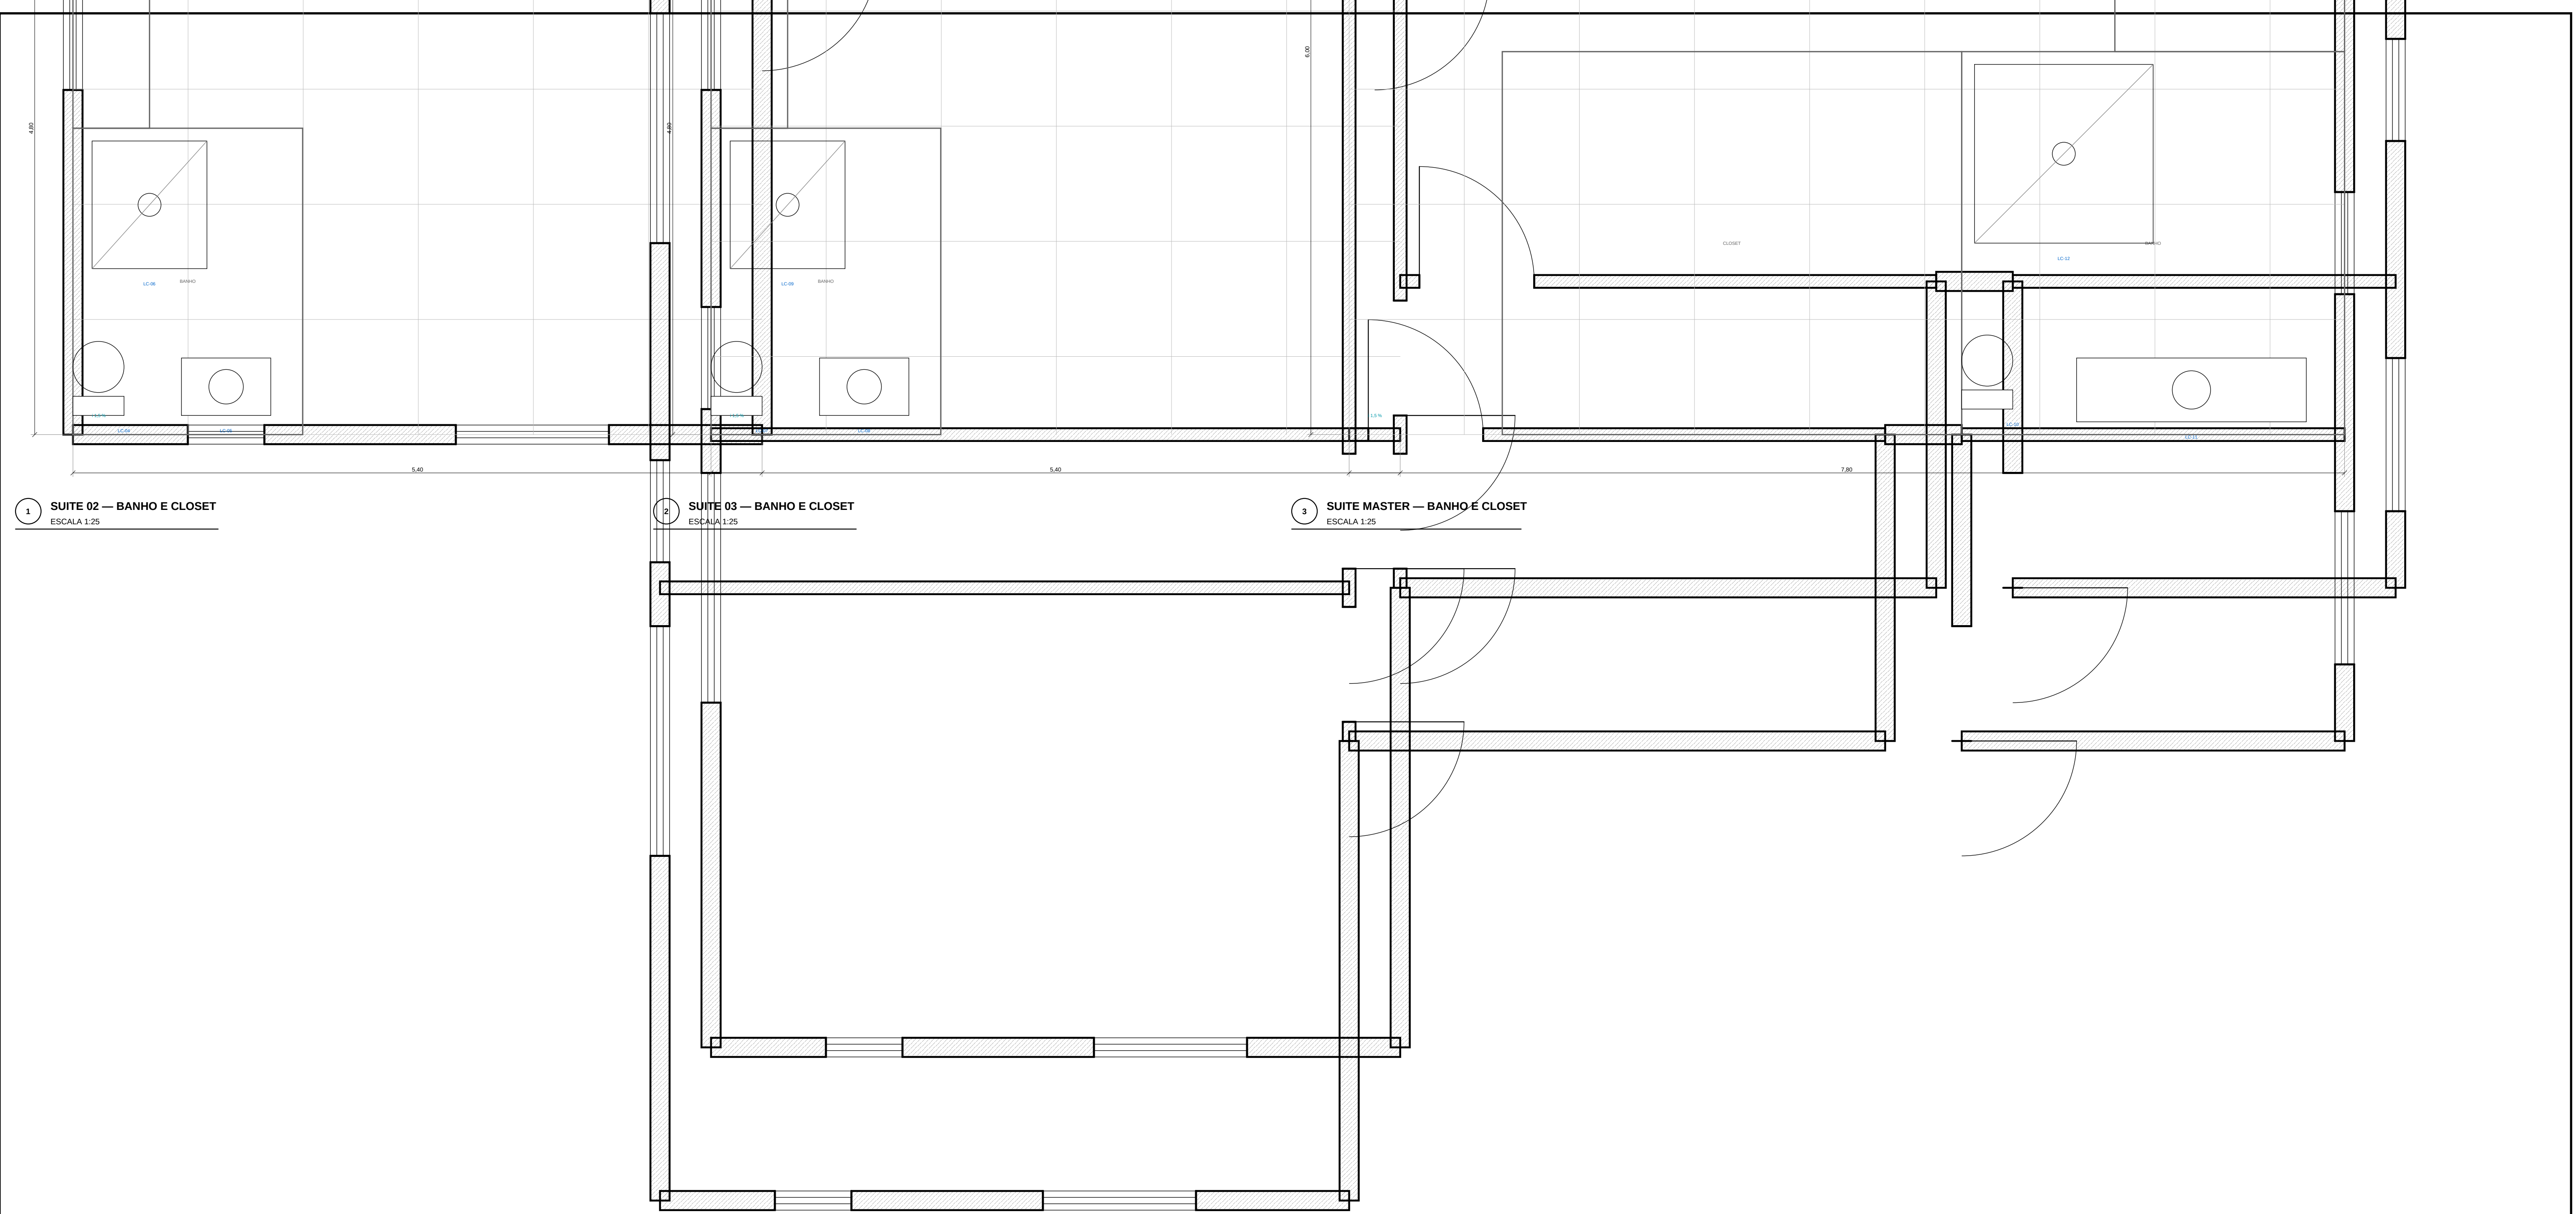

1 SUITE 02 — BANHO E CLOSET
ESCALA 1:25

2 SUITE 03 — BANHO E CLOSET
ESCALA 1:25

3 SUITE MASTER — BANHO E CLOSET
ESCALA 1:25

PAGINACAO VERIFICADA — PECAS INTEIRAS + RECORTE EM CADA PONTA

AMB	AMBIENTE	ZONA	PEÇA	ESQD X	ESQD Y	ALTURA (mm)
S-002	SUITE 02 — BANHO E CLOSET	2P-0	010	0 + 0000	0 + 0000	—
S-003	SUITE 03 — BANHO E CLOSET	2P-0	010	0 + 0000	4 + 0000	—
S-005	SUITE MASTER — BANHO E CLO	2P-0	010	0 + 0000	0 + 0000	—

- NOTAS
- * Pignetas de piso em linha fina, a malha vem da ZONA de pignetas, não do canto do ambiente.
 - * Pica de piso porcelanado retificado 300 x 300, parede cerâmico retificado 300 x 600, jato 2 mm.
 - * Cimento de 1,5 % para o piso em toda área molhada, solaria elevada 15 mm nos bicos.
 - * Representação: manta líquida em 2 demãos, subido 300 mm na parede e 1.800 mm nos bicos.

PROJETO PORTO REAL

RESIDENCIA UNIFAMILIAR (MARIA) - AM | SUITE TUPUNA-PS

PROJETO ARQUITETONICO

AMPLIACOES DE AREA MOLHADA — SUPERIOR

BASE GEOMETRICA Linha Consolidada PROJETO (previsão) UNIDADE MEDIDA: mm	ESCALA 1:25 FORMATO A1 MILHA 000000000	EXATIDAO ESTUDO PRELIMINAR NAO LIBERADO PARA OBRA SEM ART / INT	PROJETO 23 00-24
--	---	--	------------------------