
 
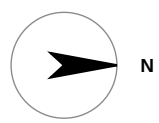


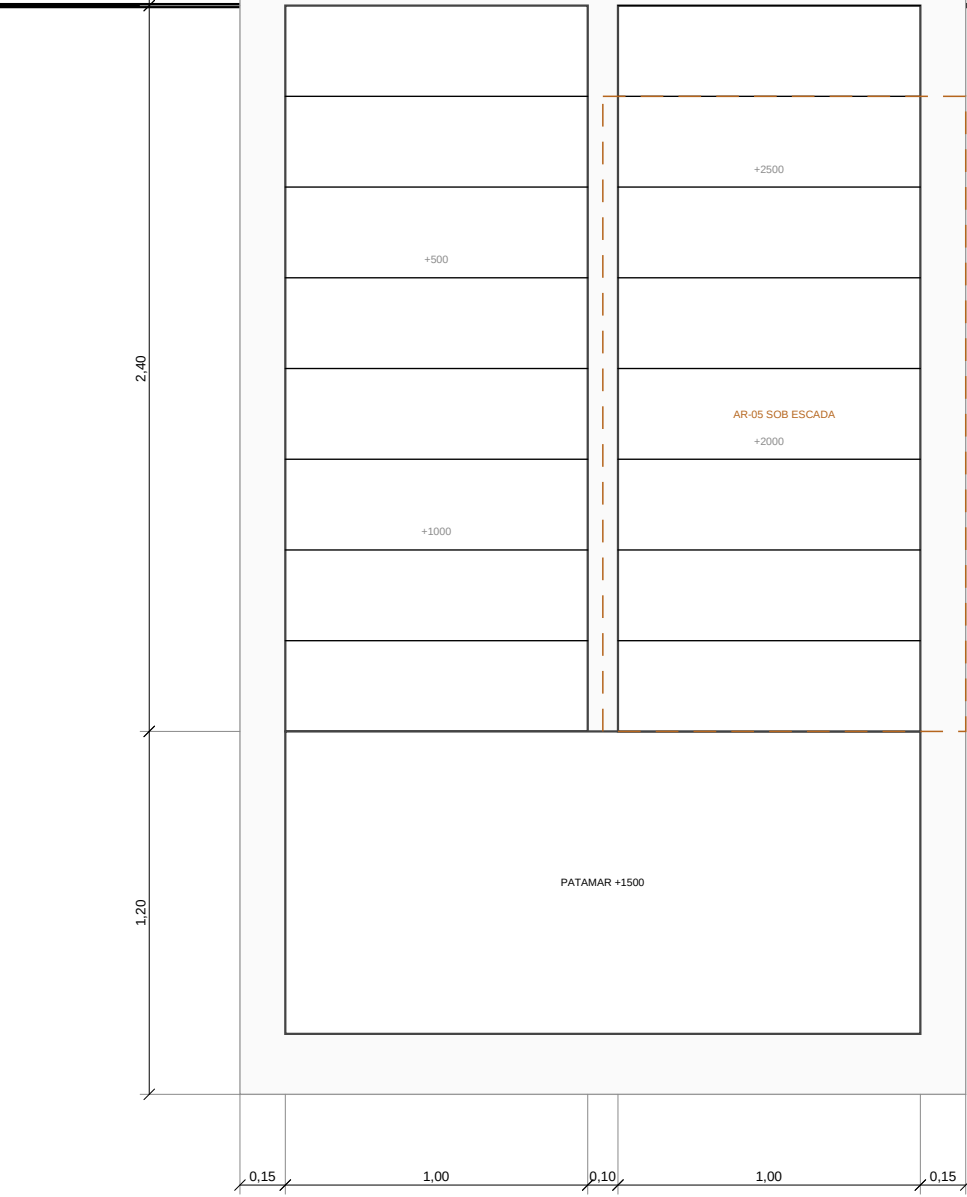

espelho fechado (NBR 9050)

chapa 800x400 3 mm + preenchido 900 x 300

faixa antideslizante de 25 mm x 25 mm de borda

2 CORTE LONGITUDINAL — ALTURA LIVRE

3 DETALHE DO DEGRAU

VERIFICACAO DA ESCADA

ITEM	PROPOSTO	NORMA	
Espelho	188.67 mm	18 a 18 cm (NBR 9071)	OK
Piso	300 mm	min 28 cm	OK
Bondex (2h + g)	633.3 mm	600 a 650 mm	OK
Largura útil do lance	1000 mm	min 1.200 mm (uso coletivo) / 1.000 mm (particular)	OK
Platamar	1000 mm	→ largura do lance	OK
Altura livre mínima	0 mm	min 2100 mm	EXCETO
Guarda-corpo	1100 mm	min 1.200 mm (NBR 14738)	OK
Corrimão	920 a 1000 mm	Acima 92 cm a 10 cm (NBR 9050)	OK
Espelho fechado	sem	conformar em caso necessário	OK
Desnível vencido	3000 mm	18 a 188.67 mm	OK

O QUE A PLANTA NAO MOSTRA

QUESTAO	RESPOSTA
Por que o primeiro espelho sobre o x e y é 1.8.00?	o primeiro terçeira 180 mm dentro da projeção do 1º degrau, com 1.000 mm de altura livre — visto que na altura da calçada do quem termina o primeiro lance
Por que a verificação de altura livre é bidimensional?	altura livre da escada e o único critério que não aparece em planta horizontal, dependendo da cor do degrau e da cor do que há acima dele
O que há sob o segundo lance?	intergelo com altura variável, destinada como amarra (NBR 9050) mas a circulação tem espaço livre
Por que espelho fechado?	degrau visado desde a porta do pé de quem usa degrau ou tem mobilidade reduzida (NBR 9050)
Por que corrimão duplo?	920 mm para adulto e 700 mm para criança, em caso com escada aberta para a sala, o segundo corrimão é o que realmente se usa

NOTAS

- 18 espelho de 188.67 mm e piso de 300 mm. Bondex 2h + g = 633.3 mm (falso recomendado 600 a 650).
- Altura livre mínima 2100 mm (NBR 9071), verificado degrau a degrau contra a tape e o resto acima.
- Guarda-corpo 1100 mm, corrimão duplo em 920 + 700 mm (NBR 9050).
- dois perfis U 200 laterais com degrau em chapa aluminada 3 mm

PROJETO PORTO REAL

RESIDENCIA UNIFAMILIAR (MANSÃO - AM) | SOUS TATIANA-PS

PROJETO ARQUITETONICO

ESCALADA — DESENHO EXECUTIVO

BASE GEOMETRICA	ESCALA	EMISSAO	PROJECOA
Lista Consolidada	indicada	ESTUDO PRELIMINAR	
ISO 8522 (previsto)	FORMATO A1	NAO LIBERADO PARA OBRA	
UNIDADE: MESTRE: MM	MAQUA: 600/500/300	SEM ART / RNT	25