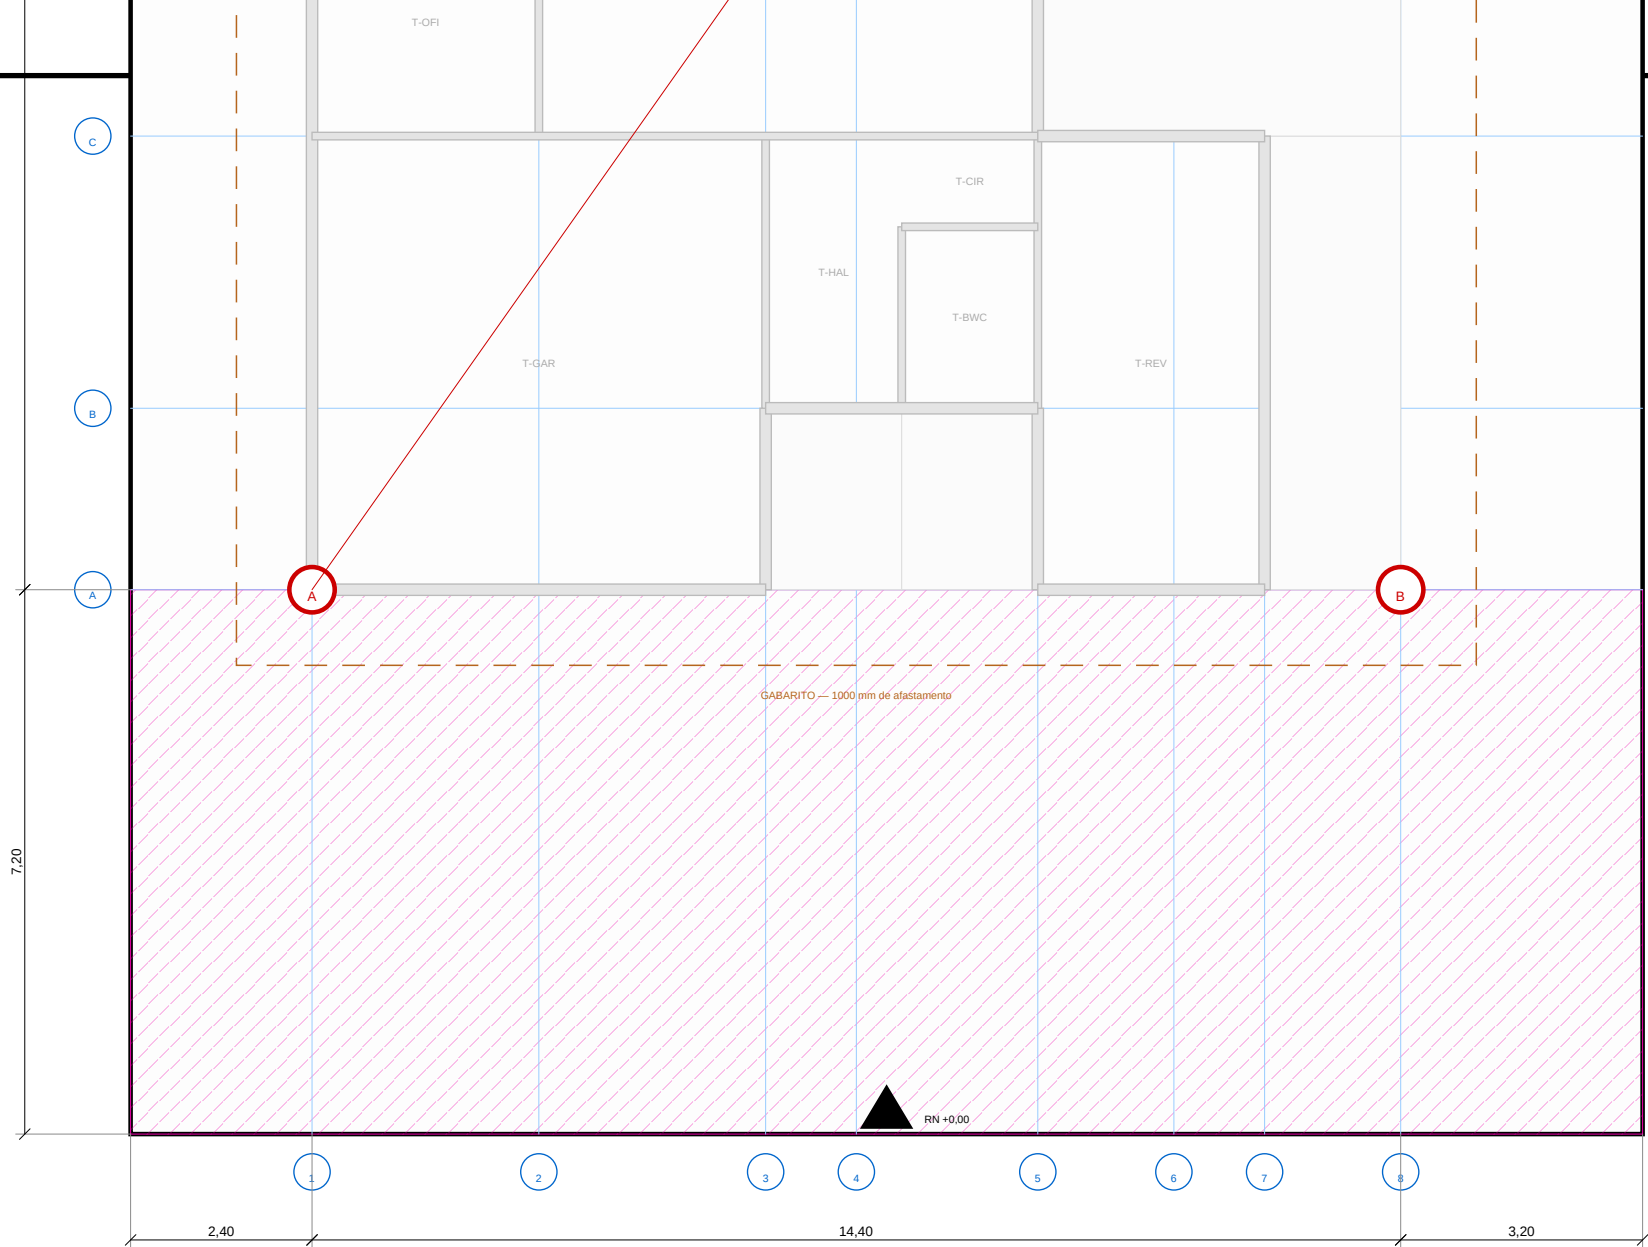


COORDENADAS DOS CANTOS (mm)

CANTO	X	Y	DIVISA SUL	DIVISA NORTE	TESTADA	FUNDO	DIAGONAL
A	2400	7200	2400	17600	7200	32000	24870,4
B	16800	7200	16800	3200	7200	32800	24870,4
C	16800	27600	16800	3200	27600	12400	24870,4
D	2400	27600	2400	17600	27600	12400	24870,4

PROCEDIMENTO DE LOCACAO

#	PASSO	CRITERIO DE ACEITE
1	Conferir as divisas com a malha e o memorial de lote.	divergencia acima de 10 mm interrompe a locacao
2	Instalar o PNM sobre o concreto 100 x 200 x 100 mm, fora da area de obra.	fora da area de obra
3	Montar o gabarito a 1000 mm do cantoneiro.	pergunte 75 x 75 a tubos 20 x 100
4	Marcar os eixos X (1) a X (8) e Y (A) a Y (H) no gabarito.	linha coordenada mltipla de 300 mm
5	Colar cado sobre os OLAS ditados.	verificar em cado: erro de cado soma
6	Conferir a diagonal A-C.	24870,4 mm com tolerancia de 10 mm
7	Conferir o quadrado por 3-4-5 em cada canto.	senao de qualquer concorrencia
8	Registrar em ata com foto e modelo.	gabarito continuo nos dois lados da obra, conferenci

EIXOS MODULARES

DIRECAO	MODULO (mm)
X (1 a 8)	2400 5400 8400 9600 12000 13800 15000 16800
Y (A a H)	7200 9600 13200 16200 19200 21600 24600 32800
Malha	principal 600 mm - subgrid 300 mm
Origem	canto frontal esquerdo do lote
Unidade	milímetros

NOTAS

- Locacao e o unico desenho em que o erro nao tem impacto direto a casa sai do lugar.
- Cada canto e cotado dos OLAS ditados, nunca em cado acumulado — erro de cado soma, erro de referencia independente nao.
- Conferencia obrigatoria pela diagonal 24870,4 mm entre A e C antes de concretar o nada.
- Nao se usa de brado, alinhado ao medidor TC-06, com 0,001 m por acabado do terreno.

PROJETO PORTO REAL

RESIDENCIA UNIFAMILIAR (MANAUS - AM) | SOUS TATIANA-PS

PROJETO ARQUITETONICO

LOCACAO DE OBRA E GABARITO

BASE GEOMETRICA Linha Consolidada em PDF (previsão) UNIDADE: METROS - MM	ESCALA 1:100 FORMATO A1 MALHA: 600/300/300	EMISSAO ESTUDIO PRELIMINAR NAO LIBERADO PARA OBRA SEM ART / RNT	PROJETA 31 05/24
---	--	--	-------------------------------