



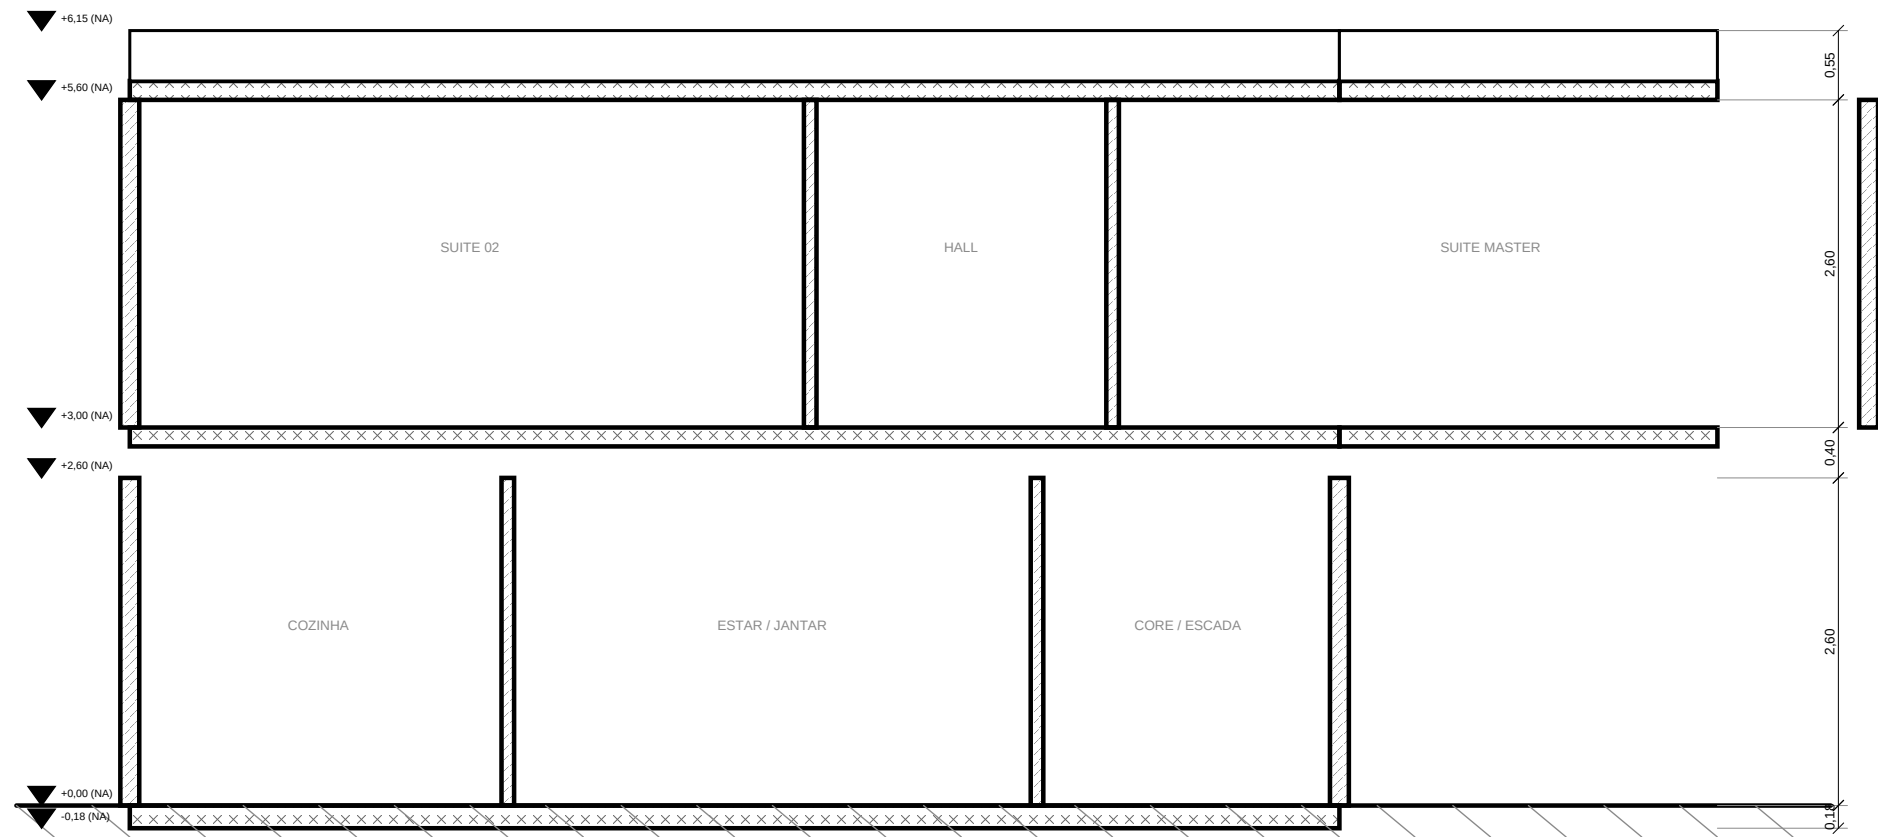

1 CORTE AA — TRANSVERSAL
ESCALA 1:60

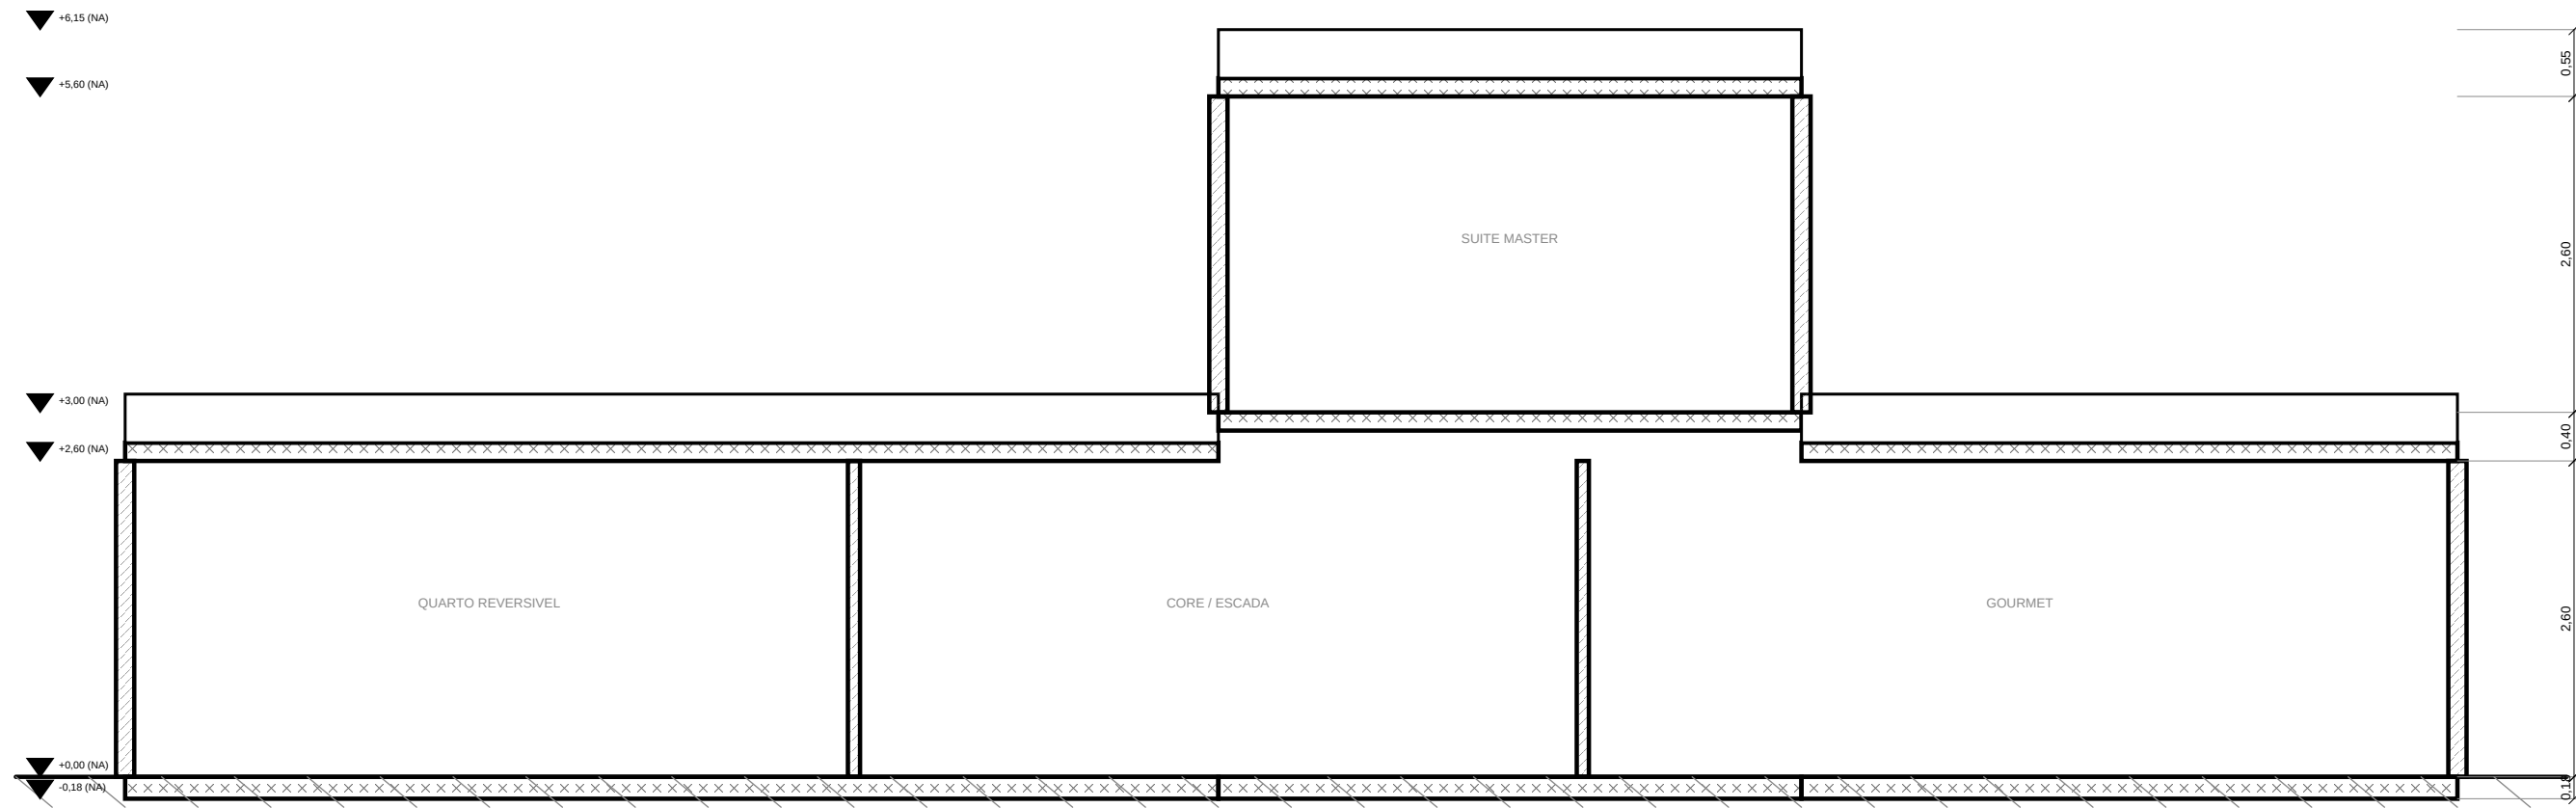

2 CORTE BB — LONGITUDINAL
ESCALA 1:60



NOTAS

- * Piso elevado acabado 2500 mm, piso a piso 3000 mm.
- * Topo da platibanda +0.250 m (não pavimentado) e +0.100 m (pavimentado) — H.
- * Fundação em radier 180 mm, traço 30 MPa, aço CA-50 (S).
- * Vedação em Light Steel Frame, vãos grandes em perfil metálico estrutural.

PROJETO PORTO REAL

RESIDÊNCIA UNIFAMILIAR (MANSÃO) - AM | SUDOESTE-PR

PROJETO ARQUITETÔNICO

CORTES AA E BB

FASE GEOMÉTRICA	ESCALA	EMISSÃO	PROJETO
Lista Consolidada	1:60	ESTUDO PRELIMINAR	06
Projeto (preliminar)	FORMATO A1	IMÓVEL LIBERADO PARA OBRAS	06.25
UNIDADE MESTRE: AM	MALHA 600/600/300	SEM AMT / RMT	