


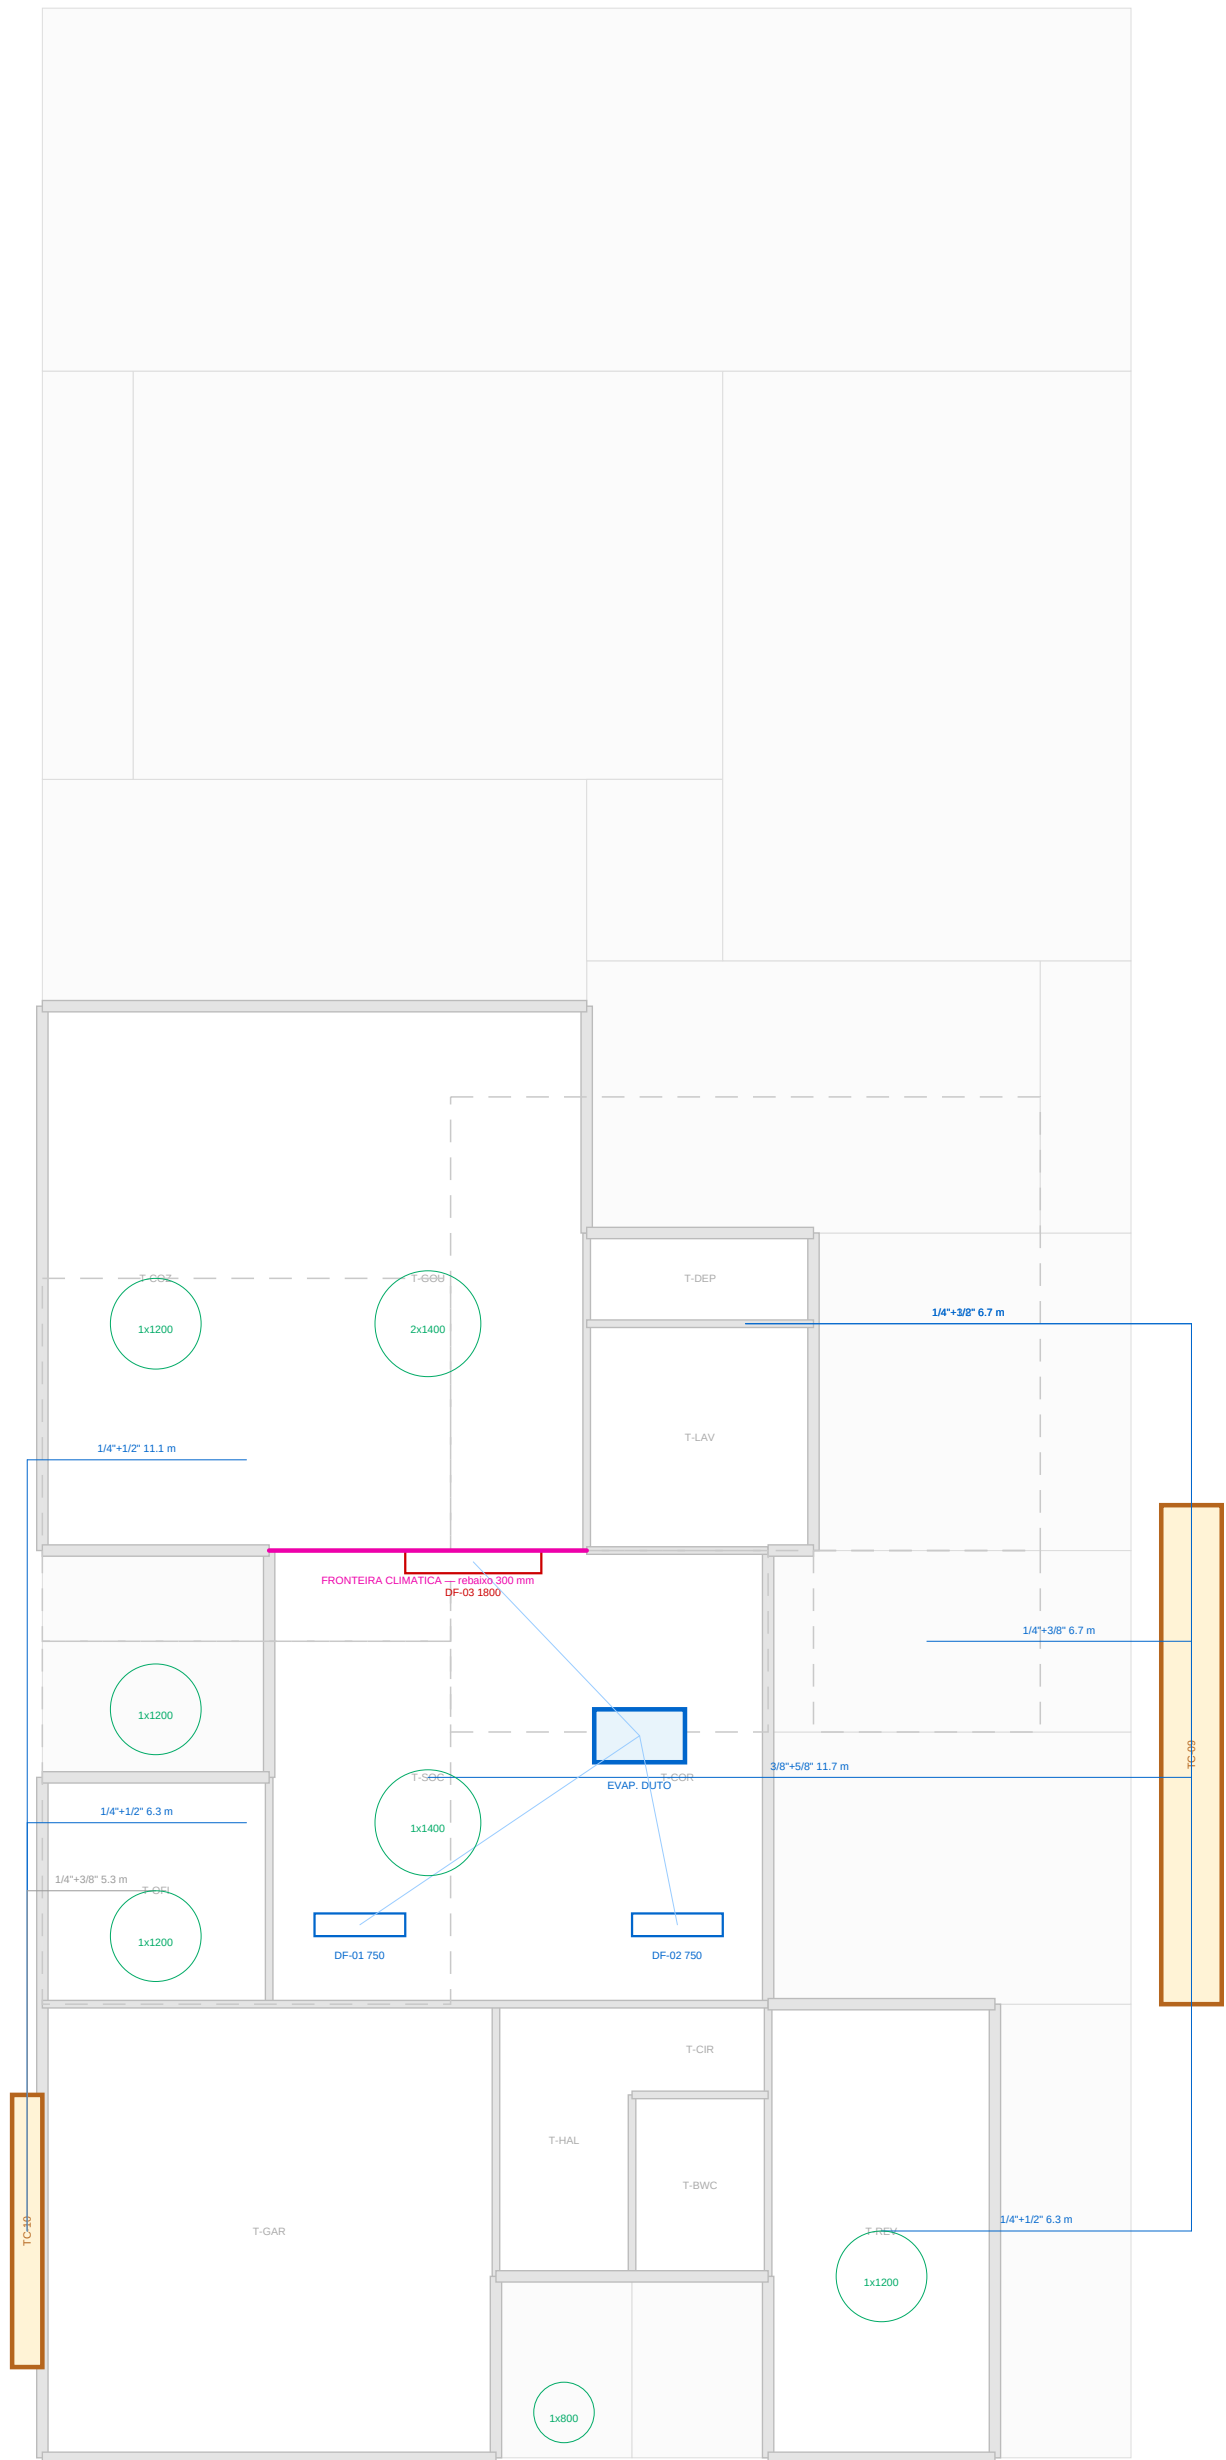

1 PERCURSO DAS LINHAS E DUTOS
ESCALA 1:100

LINHAS FRIGORÍGENAS — PERCURSO E BITOLA

Linha	AMB	INCHO	BTU/h	HORIZ (m)	VERT (m)	TOTAL (m)	SUCCASÃO	DRENO	CARGA EXTRA	FASE
S-MA5	S-MA5	TC-09	18.000	1,6	3,8	6,7	1/4" x 1/2"	DN25	—	ABR
T-REV	T-REV	TC-09	18.000	2,2	2,6	6,3	1/4" x 1/2"	DN25	—	ABR
S-SE2	S-SE2	TC-10	18.000	1,2	3,8	6,3	1/4" x 1/2"	DN25	—	ABR
S-SE3	S-SE3	TC-10	18.000	6,0	3,6	11,1	1/4" x 1/2"	DN25	R2 g	ABR
S-SDC	T-SDC	TC-08	20.000	1,6	2,8	11,7	3/8" x 1/2"	DN25	R2 g	ABR
S-UDV	S-UDV	TC-09	9.000	1,6	3,8	6,7	1/4" x 3/8"	DN25	—	ABR
PFCE	S-MA5	TC-09	9.000	1,6	3,8	6,7	1/4" x 3/8"	DN25	—	ABR
T-OR	T-OR	TC-10	9.000	1,2	2,8	5,3	1/4" x 3/8"	DN25	—	ABR

DUTOS, DIFUSORES E EXAUSTÃO

ELEMENTO	VIAJADA (mm)	DNOM	OBSERVAÇÃO
DP-02 — insulflex	750	T-SDC	junto parede contra do motor
DP-02 — insulflex	750	T-COR	com tubo o pouco de luz

(continuação)

ELEMENTO	VIAJADA (mm)	DNOM	OBSERVAÇÃO
EX-02 — ducto oval	85	T-SDC	DN25
EX-02 — ducto oval	105	T-COR	DN25, nota unidade da máquina o da máquina
EX-02 — ducto oval	125	S-MA5	DN25
EX-02 — ducto oval	85	S-MA5	DN25, instalado contra da parede com grampo de 6

- NOTAS
- Dots rictos de condensação. Linha mais longa 11,7 m, contra o limite de contorno de 15 m.
 - Dreno DN25 com calçamento mínimo de 2% e altura antes da descarga, nunca ligado a engelo sem alho.
 - Duto de insulflex no comprimento de 400 mm — nunca abreviar montado.
 - Isolamento contínuo na travessa de parede, com bucha de passagem, caso de isolamento na parede condensa dentro da montante.

PROJETO PORTO REAL

RESIDENCIA UNIFAMILIAR (MANUS - AM) (SOL TATIANA-PS)

PROJETO ARQUITETONICO

CLIMATIZACAO — LINHAS FRIGORÍGENAS, DUTOS E DRENOS

BASE GEOMETRICA Linha Consolidada Projeto (previsão) Unidade: METRE (m)	ESCALA 1:100 FORMATO A1 MILHA 650/500/500	EXATIDÃO ESTUDO PRELIMINAR R2 Linha LIBERADO PARA OBRA SEM ART / RNT	PROVA 28 IN 25 REV R2
--	--	---	-----------------------------