


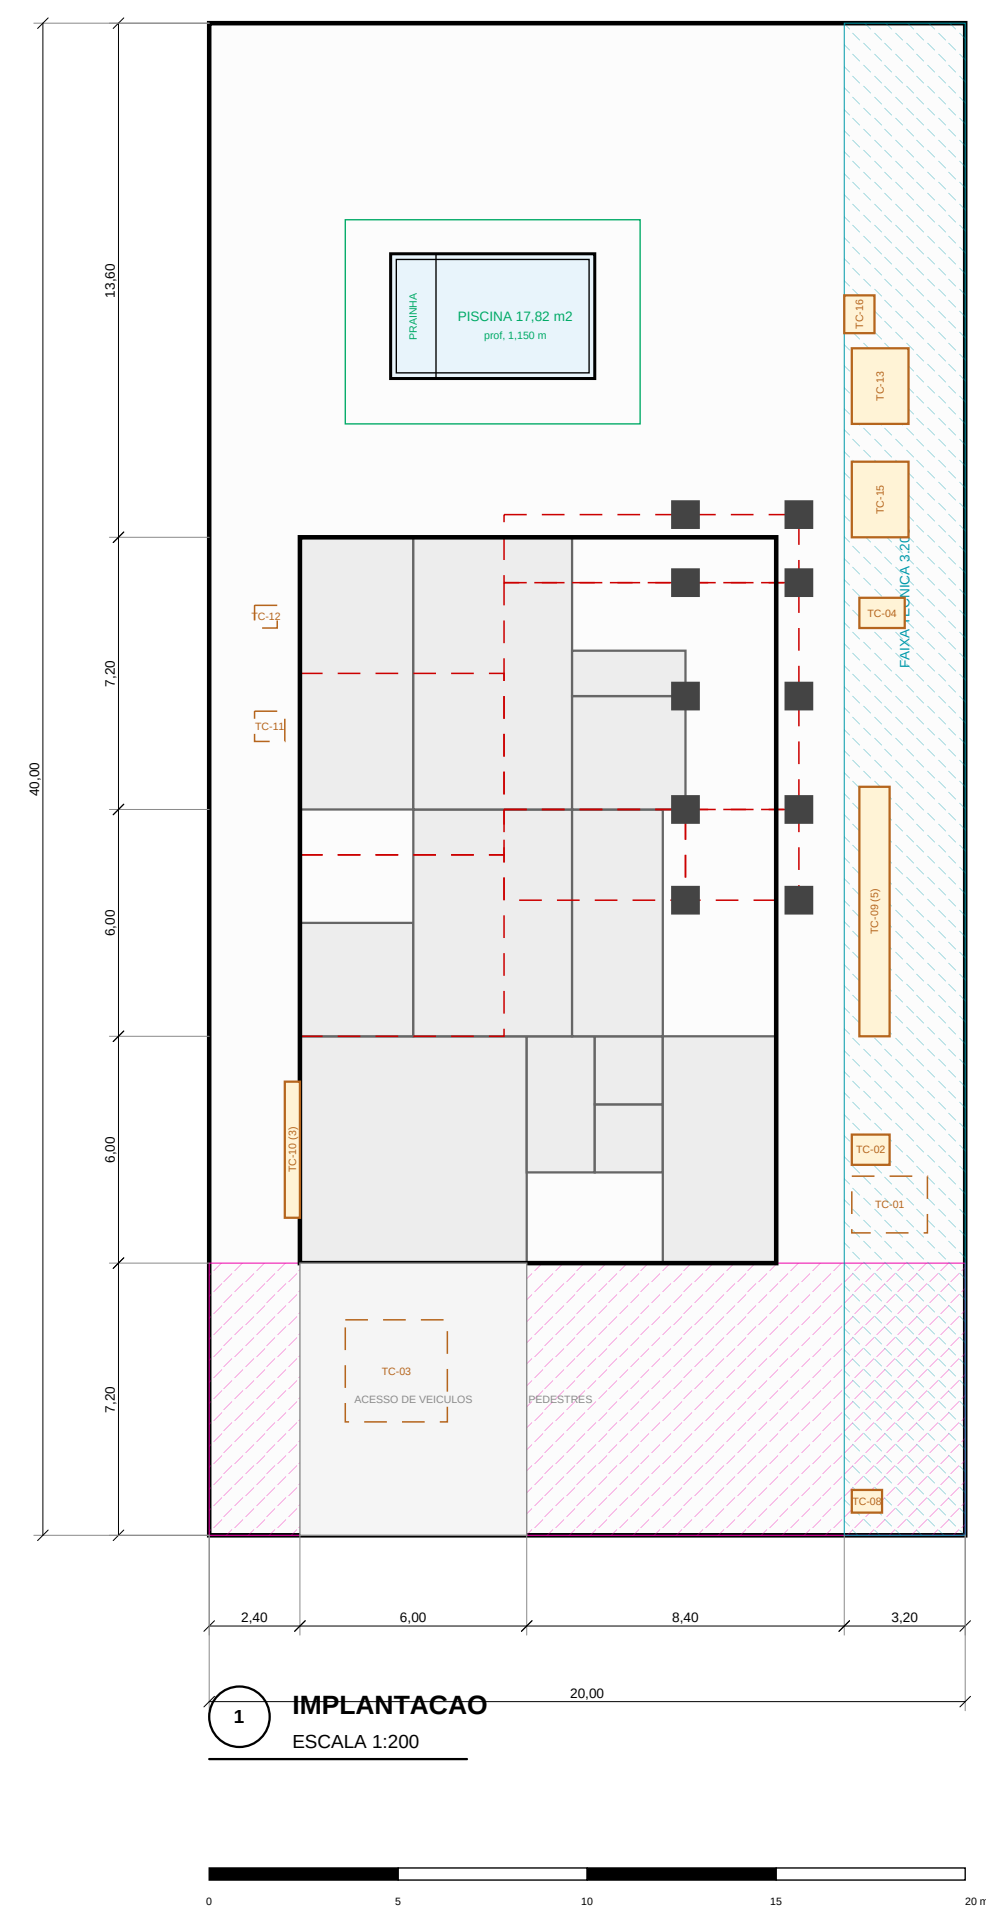

NOTAS

- Lote 25 000 x 40,000 mm = 800,00 m².
- Recuos: frontal 7,200 / lateral esq. 2,400 / faixa técnica dir. 3,200 / fundo 13,600 mm.
- Parâmetros do S/25 Tarumã/Tarumã-Açu são hipotéticos (H) — pendente certidão de uso do solo.
- Sem muro frontal; muros laterais e de fundo h = 2,200 mm.

RESIDENCIA UNIFAMILIAR | MANAUS - AM | SUÍTE TARIUMA (H)

PROJETO ARQUITETÔNICO

BASE: GEOMETRICA

Lista Consolidada

pos-R32 (prevalence)

UNIDADE MESTRE: m

ESCALA

1:200

FORMATO A1

EMISSÃO

ESTUDO PRELIMINAR R56

NAO LIBERADO PARA OBRA

SEM ART / RNT

FRANCHIA

01

de 40 REV R55