




● luminária embuída, 3.000 K, RSC 90

□ alçapão técnico 600 x 600 mm

▨ forro absorvente (alfa 0,70)

FORROS POR AMBIENTE

AMBIENTE	SOLUÇÃO	ÁREA	NOTA
T-03A	forro absorvente (α=0,70) e refletor no par	36,24	único ponto que demanda a instalação de 3,20 x 3,20
T-03C	gesso liso + cantoneira e lapinha	25,20	abertura entre os módulos, forro técnico aqui não
T-03D	gesso liso + refletor	18,00	superfície de fácil limpeza sem necessidade de manutenção
S-03D	gesso liso + la mineral sobre o forro	25,80	la sobre o forro absorve o calor do teto no parafuso
S-03E	gesso liso + la mineral sobre o forro	25,80	idem
S-03F	gesso liso + la mineral sobre o forro	25,80	idem
T-03G	sem forro (estrutura aparente)	36,00	ambiente semi-industrial, acústica não forçada
T-03H	sem forro (estrutura aparente)	9,00	idem
T-03I	sem forro (estrutura aparente)	9,00	idem

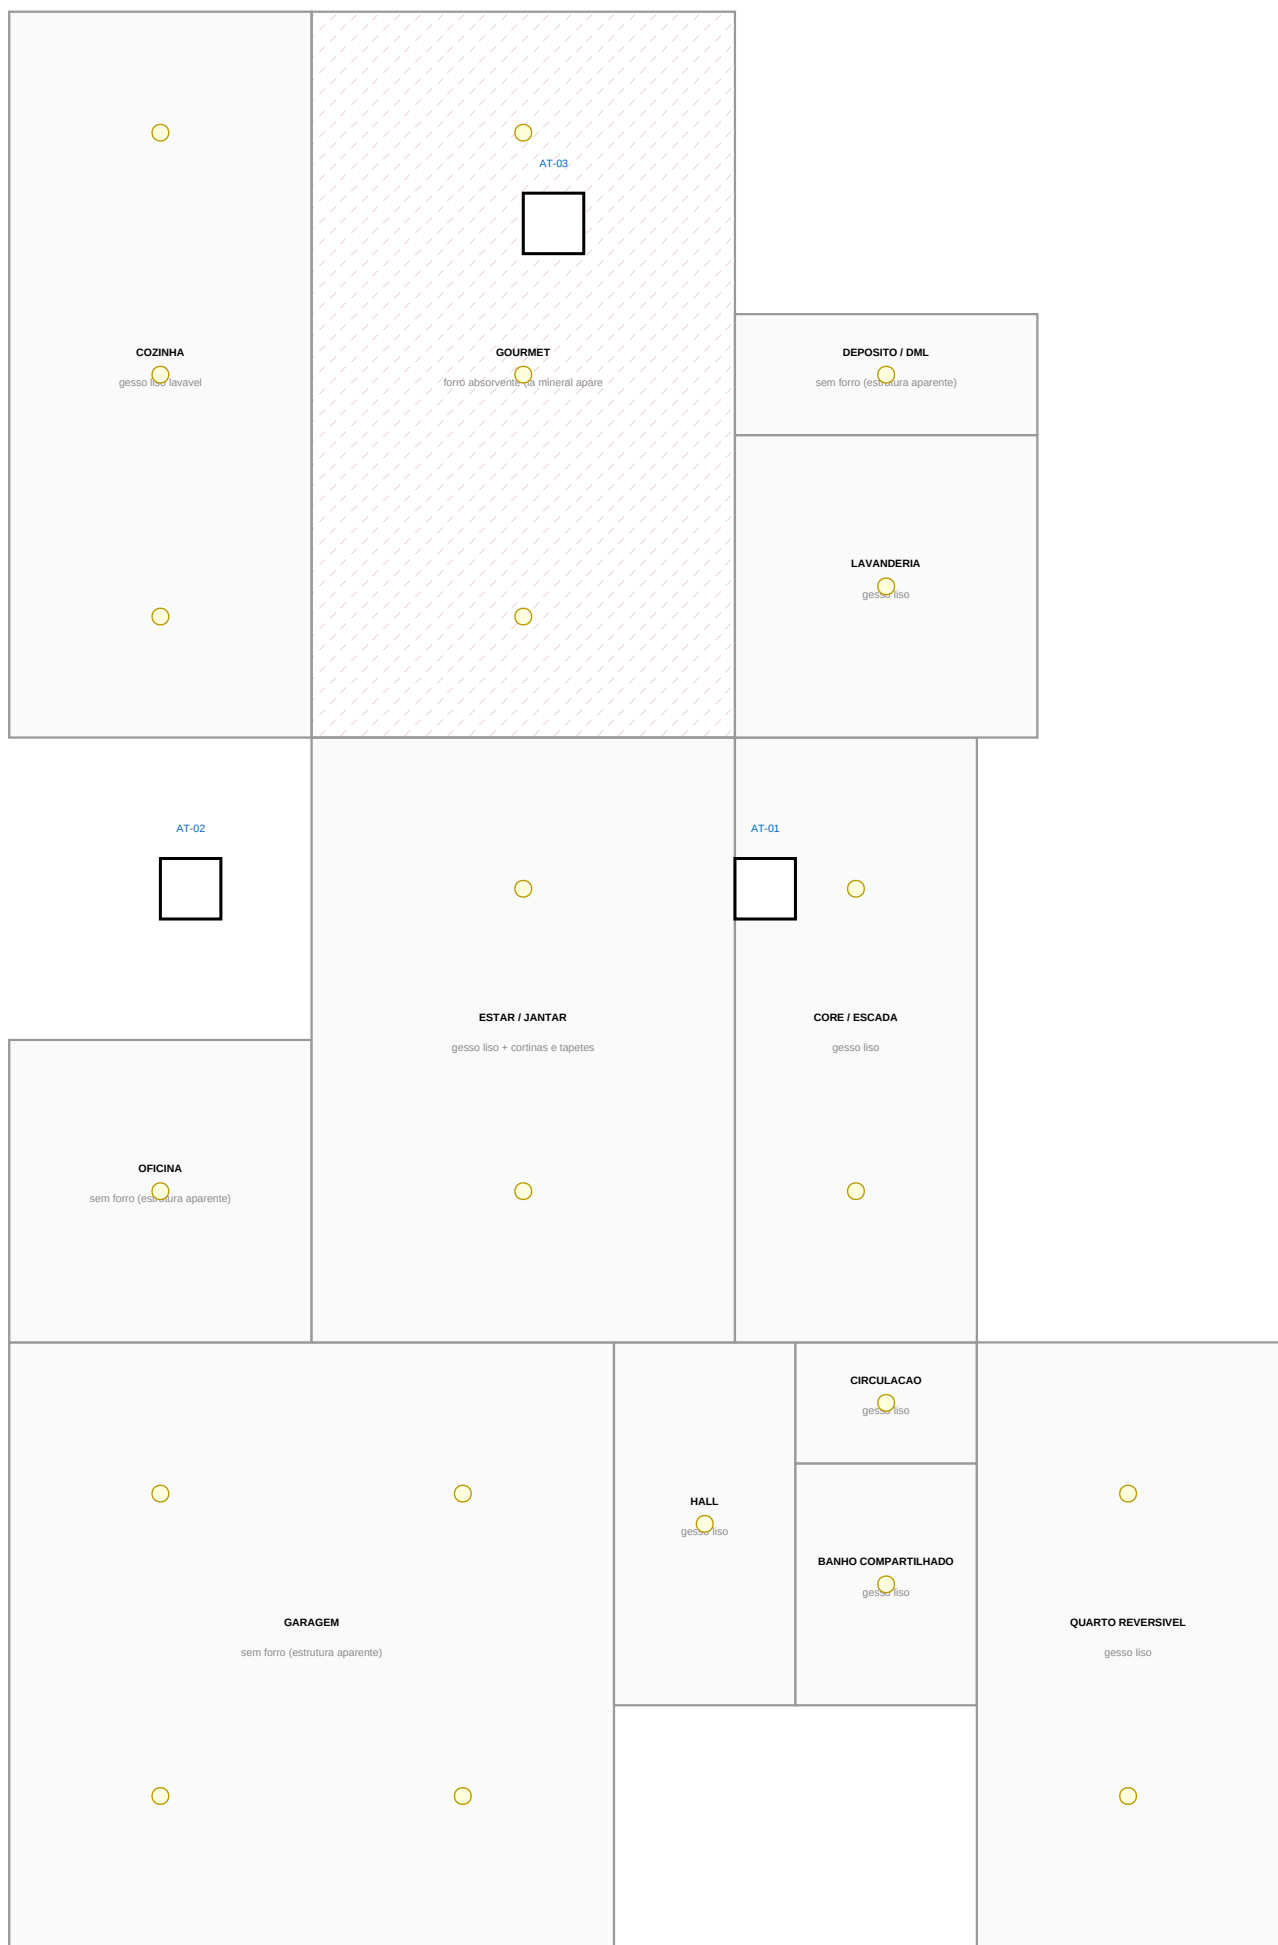

1 FORRO REFLETIDO — TERREO
ESCALA 1:75

NOTAS

- * Planta refletida: vista do forro projetada no plano horizontal.
- * Forro absorvente apenas no gourmet — único ponto com necessidade crítica.
- * Alçapão técnico de 600 x 600 mm, passando de cobertura de 600 mm.
- * Luminária geral 3.000 K, RSC modelo 90.

PROJETO PORTO REAL

RESIDÊNCIA UNIFAMILIAR (MANSÃO - AM) | SOBR TATIANA-PS

PROJETO ARQUITETÔNICO

PLANTA DE FORRO E ILUMINAÇÃO

BASE GEOMÉTRICA	ESCALA	EMISSÃO	PROVA
União Consolidada	1:75	ESTUDO PRELIMINAR R31	16
PROJETO	FORMATO A1	IMAGEM LIBERADA PARA OBRAS	
UNIDADE MÉTRICA: mm	MÁQUINA: 600/600/300	SEM ART / RNT	06-25 REV 031