


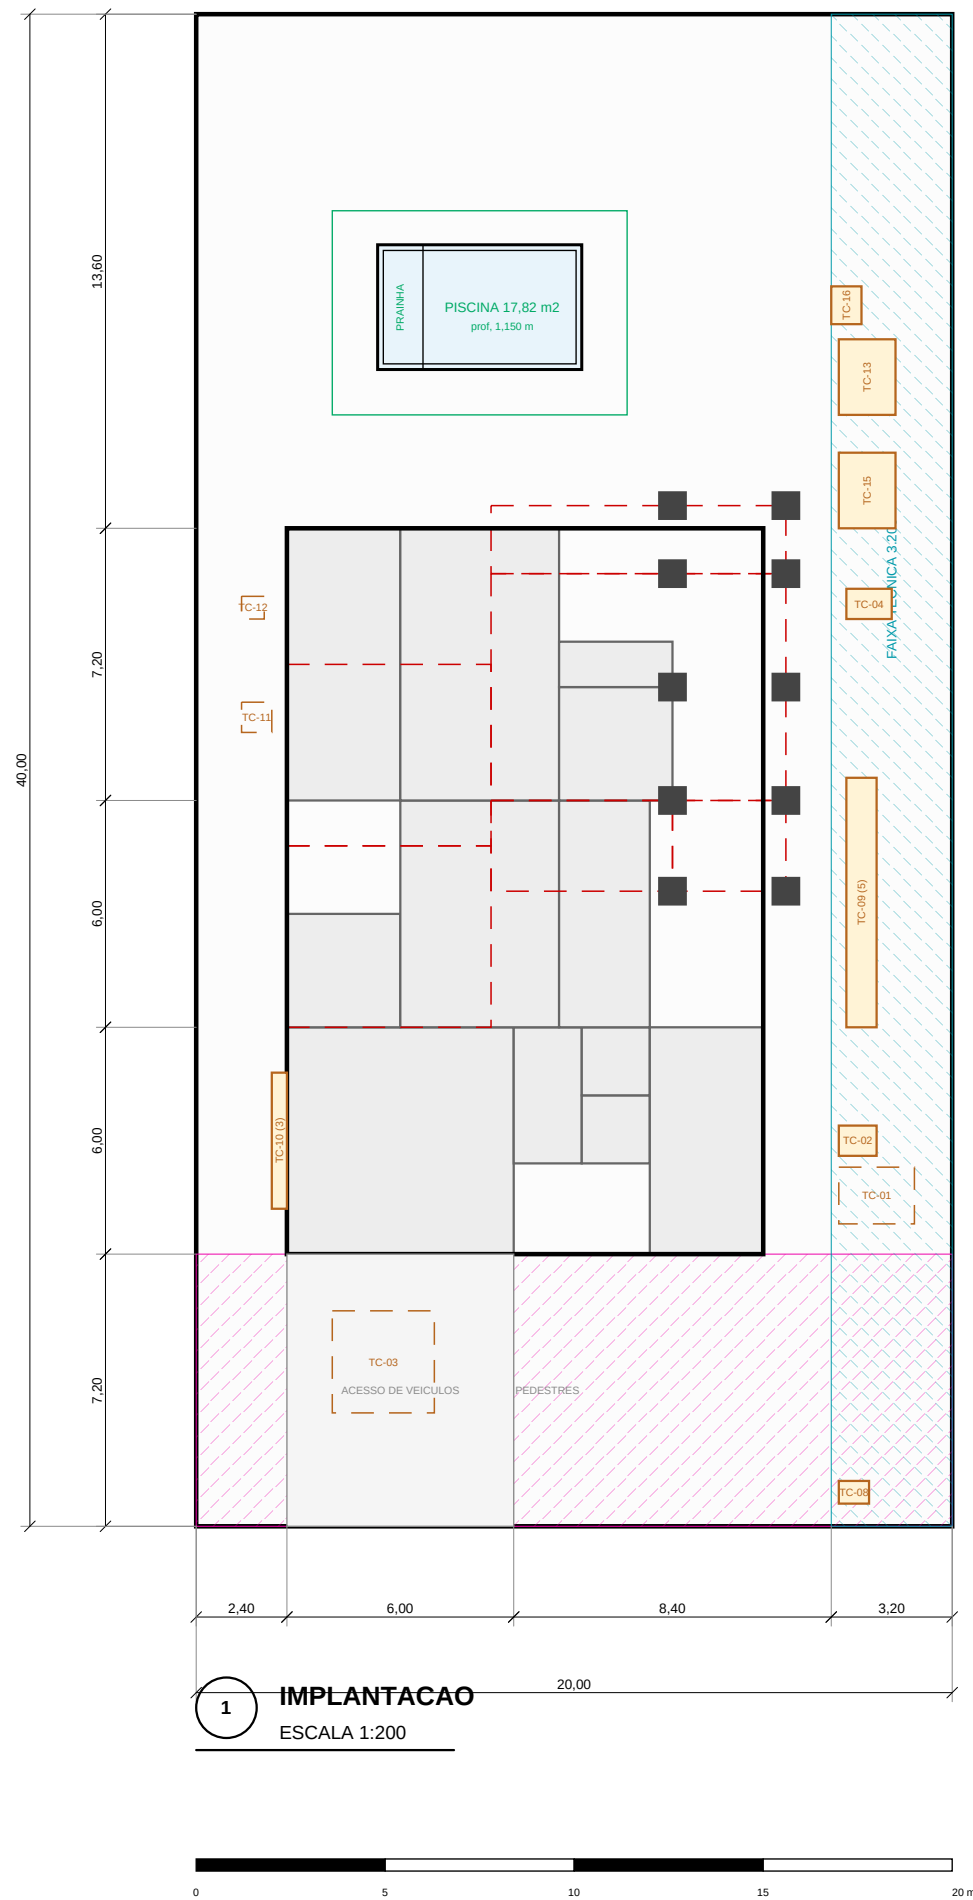

VERIFICACAO URBANISTICA (H)

PARAMETRO	PROJETO	LIMITE	
Taxa de ocupação	33,21 %	até 50 %	OK
Coef. de aproveitamento	0,372	até 1,00	OK
Galvao	2 pavimentos	até 4	OK
Recuo frontal	7200 mm	conforme 5000 [4]	OK
Recuo lateral esq.	2400 mm	sem limite no lado	OK
Recuo lateral dir.	3000 mm	até 3000 mm	OK
Recuo de fundo	13600 mm	até 5000 mm	OK



- NOTAS
- * Lote 25.000 x 40.000 mts = 800.00 m2.
 - * Recuo frontal 7.200 / lateral esq. 2.400 / lateral dir. 3.000 / fundo 13.600 mts.
 - * Parametro do SCSB Tatuá/Porto Real - Agua sem Regeneração [H] - pendente conforme de uso do solo.
 - * Sem muro frontal, mural lateral e de fundo 0 x 2.000 mts.

PROJETO PORTO REAL

RESIDENCIA UNIFAMILIAR (MANSÃO - AM) | SOUS TATUÁ-PR

PROJETO ARQUITETONICO

IMPLANTACAO E SITUACAO

BASE GEOMETRICA Linha Consolidada em R22 (previsão) UNIDADE: METROS - MM	ESCALA 1:200 FORMATO A1 MILHA 465/500/500	EMISSAO ESTUDO PRELIMINAR R57 LADO LIBERADO PARA OBRAS SEM ART / RNT	PROVA 01 06-48 REV R57
---	---	---	-------------------------------------