


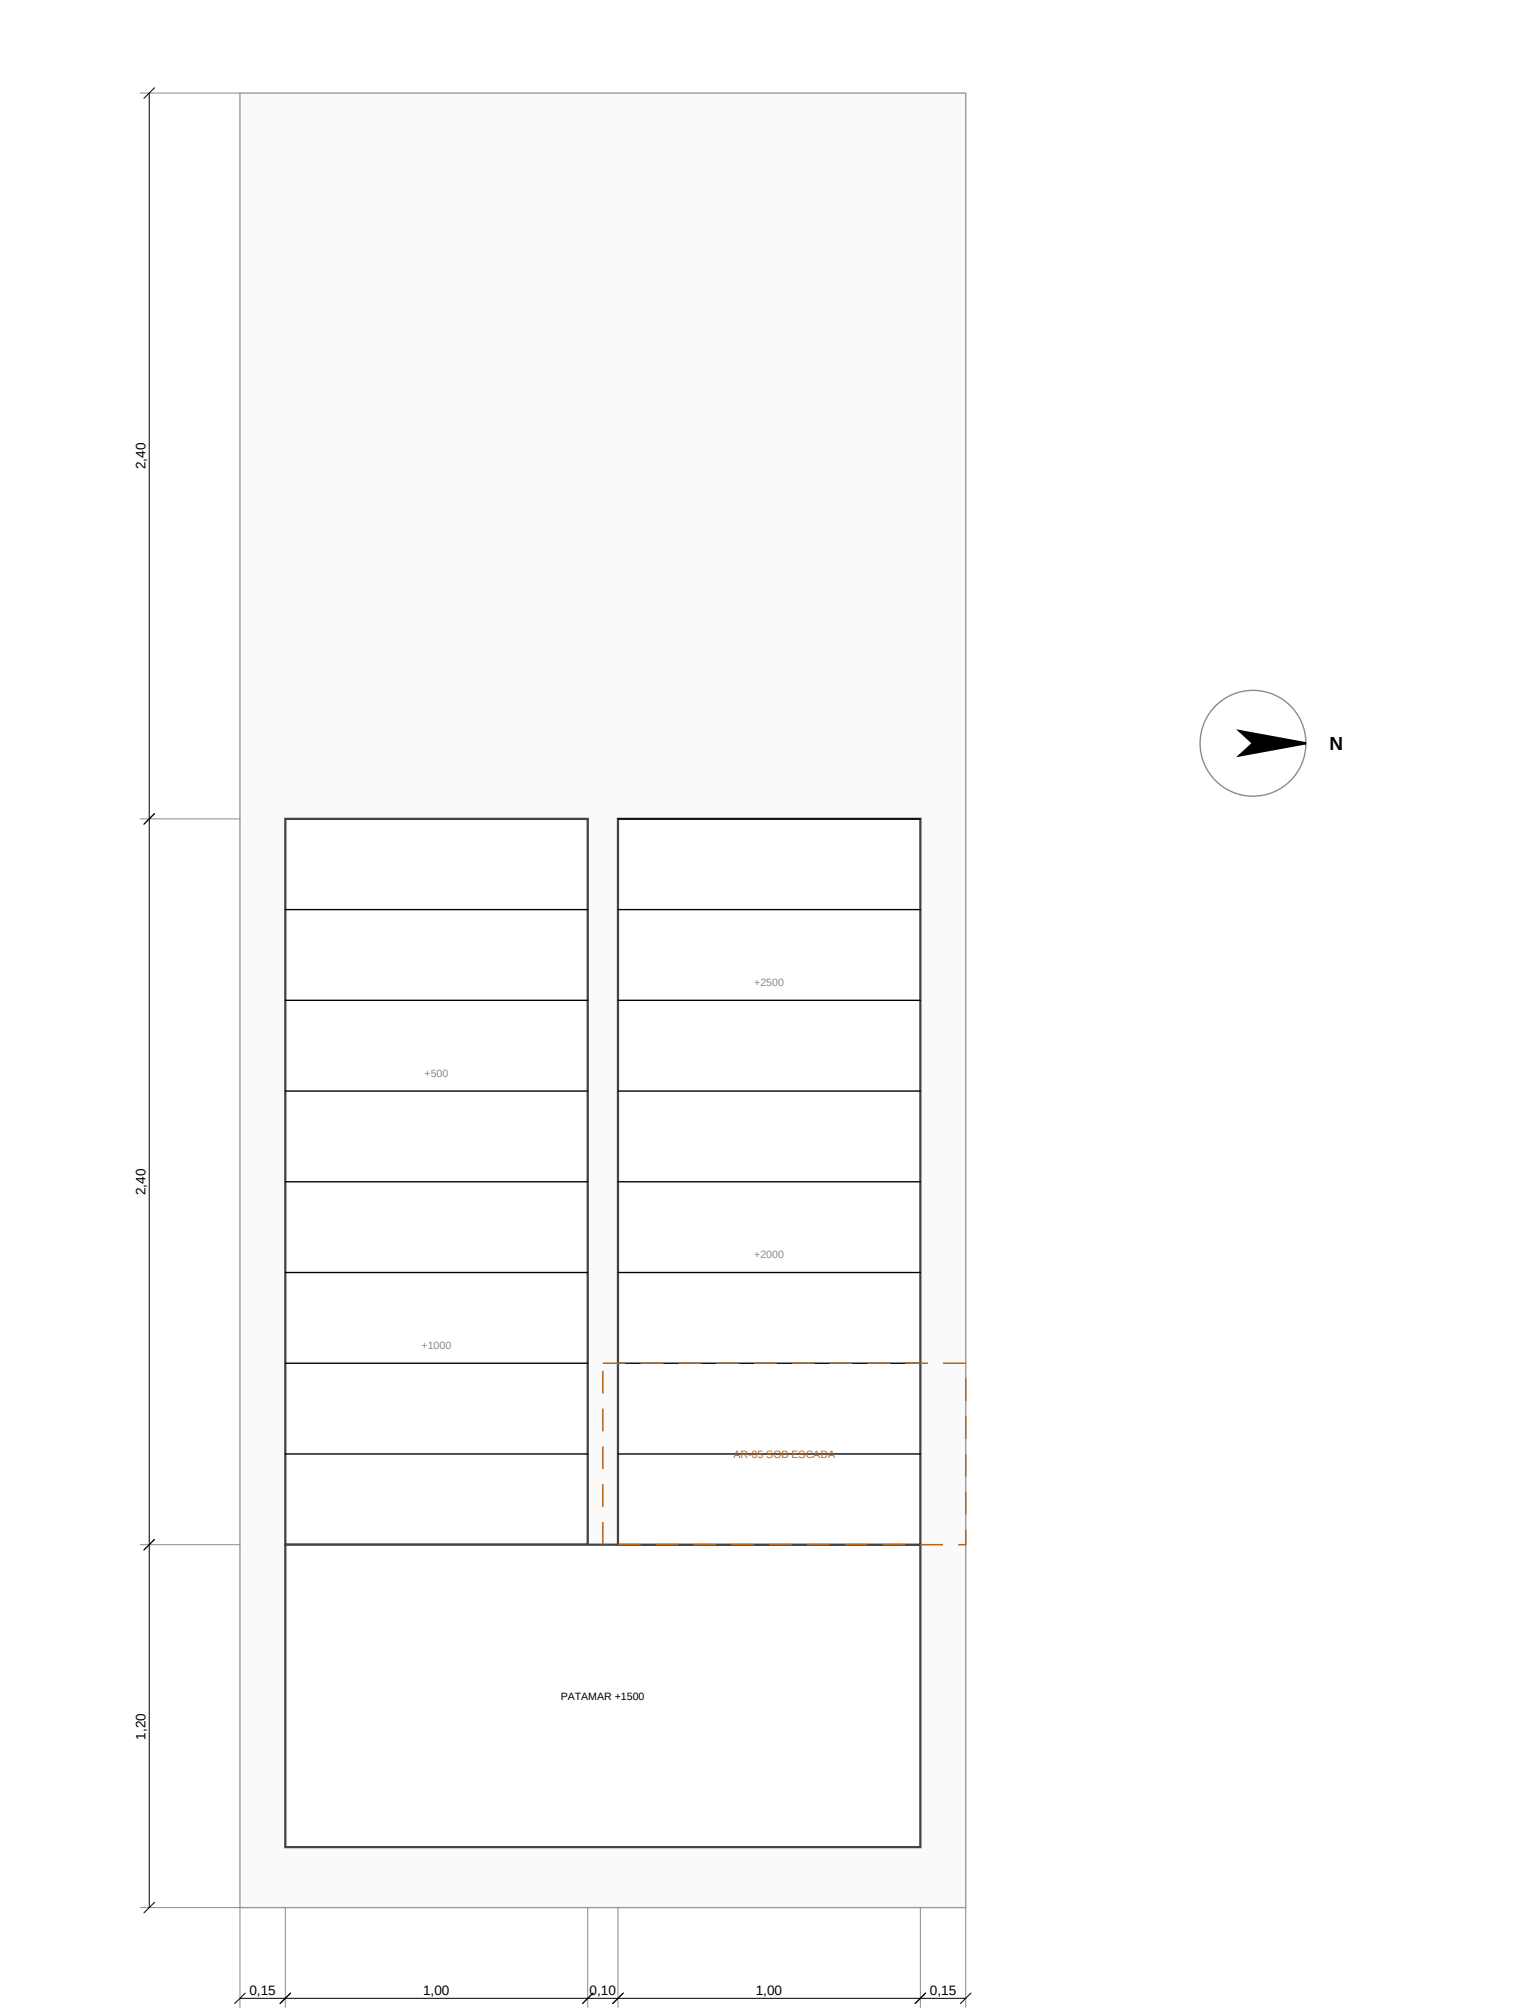


1 PLANTA DA ESCADA
ESCALA 1:25

VERIFICACAO DA ESCADA

ITEM	PROPOSTO	NORMA	
Fuste	168,67 mm	16 a 18 cm (NBR 9077)	OK
Piso	300 mm	min 28 cm	OK
Bondar (2h + g)	633,3 mm	600 a 650 mm	OK
Largura útil do lance	1000 mm	min 1.200 mm (para cobrir) e 1.300 mm (para ficar)	OK
Patamar	1000 mm	min largura do lance	OK
Altura livre mínima	0 mm	min 2300 mm	RECU
Guarda-corpo	1100 mm	min 1.200 mm (NBR 14738)	OK
Corrimão	920 a 1000 mm	Acima 92 cm e 10 cm (NBR 9050)	OK
Espelho fechado	sim	conformidade com normas	OK
Desnível vencido	3000 mm	18 a 168,67 mm	OK

O QUE A PLANTA NAO MOSTRA

QUESTAO	RESPOSTA
Por que o primeiro espelho sobe de 2 e 1,3000?	o patamar tem uma 200 mm dentro da projeção do tal espelho, com 1.000 mm de altura livre — então quanto a altura da cobertura do quem tem o primeiro lance
Por que a verificação de altura livre é bidimensional?	altura livre do espaço e o único dentro que não aparece em planta horizontal, dependendo da cor do degrau e da cor do que há acima dele
O que há sob o segundo lance?	intergap com altura útil variável, destinada como armário (até 600 mm) e circulação sem espaço morto
Por que espelho fechado?	depois vazio, prende a porta do pé de quem está longe do seu nível de circulação (NBR 9050)
Por que corrimão duplo?	920 mm para adulto e 700 mm para criança, em caso de escada aberta para a sala, o segundo corrimão é o que realmente se usa

 

2 CORTE LONGITUDINAL — ALTURA LIVRE
ESCALA 1:25

3 DETALHE DO DEGRAU
ESCALA 1:5

espelho fechado (NBR 9050)

chapa 800x400 3 mm + preenchido 900 x 300

face antiderrapante de 25 mm a 25 mm da borda

NOTAS

- 18 espelhos de 168,67 mm e piso de 300 mm. Bondar 2h + g = 633,3 mm (falso recomendado 600 a 650).
- Altura livre mínima 2300 mm (NBR 9077), verificada diagonal a degrau contra a tape e o vazio acima.
- Guarda-corpo 1100 mm, corrimão duplo em 920 e 700 mm (NBR 9050).
- dois patas 10 200 mm com degrau em chapa antiderrapante 3 mm

PROJETO PORTO REAL

RESIDENCIA UNIFAMILIAR (MARIAUS - AM) | 5000 TATAMAR-PI

PROJETO ARQUITETONICO

ESCALADA — DESENHO EXECUTIVO

BASE GEOMETRICA	ESCALA	EMISSAO	PROVA
Unidade Consolidada	indicada	ESTUDIO PRELIMINAR R57	25
Projeto (previsão)	FORMATO A1	NAO LIBERADO PARA OBRA	
Unidade (previsão)	MAQUETA 600x900	SEM ART / RNT	06-48 REV R57