


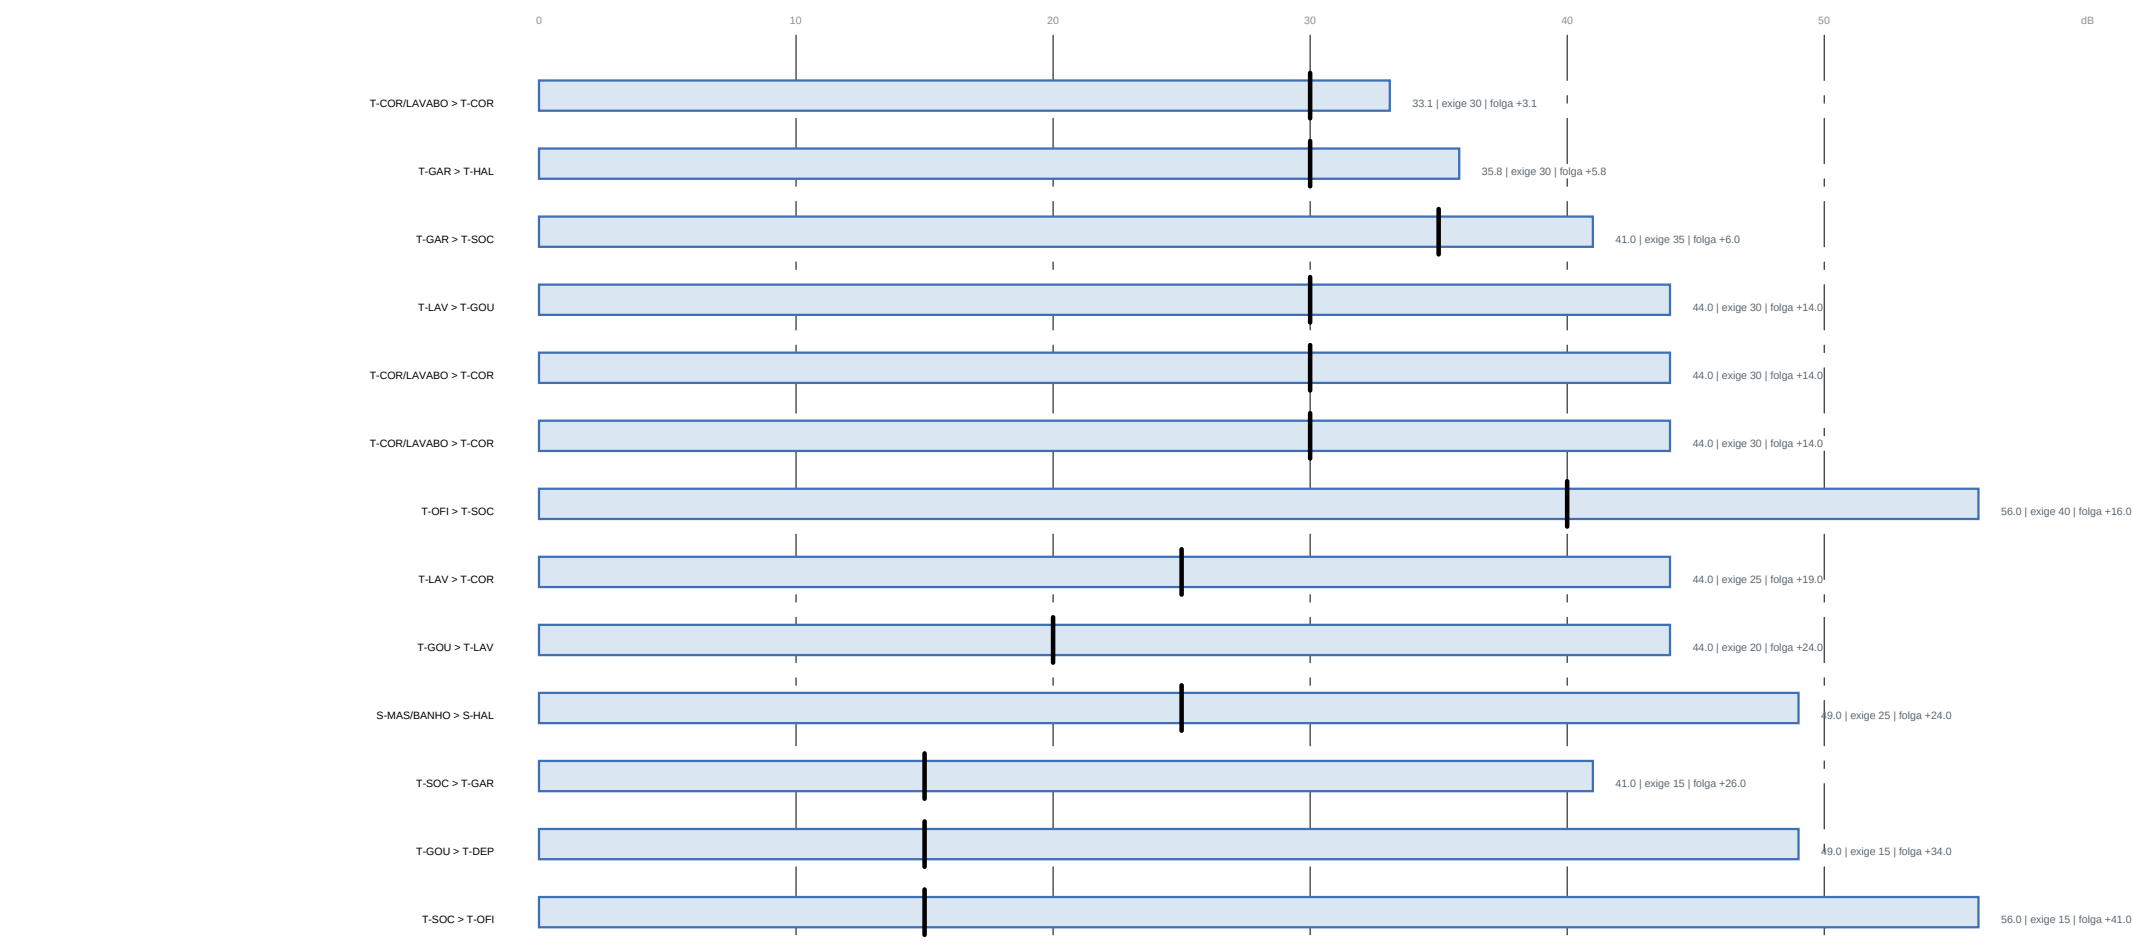

Barra = isolamento edificado; traço vertical = energia (linha da fonte menos fonte do receptor, NBR 15102)

O QUE MUDOU EM R52

| ONDE                                  | ANTES                                               | DEPOIS                                   | POR QUE                                                                            |
|---------------------------------------|-----------------------------------------------------|------------------------------------------|------------------------------------------------------------------------------------|
| Banho compartilhado + hall de entrada | porta de correr (Rw 25) — conjunto de 20,2 dB       | parede CEGSA, 44 dB                      | o acesso de volta passou para a circulação                                         |
| Banho compartilhado + quarto eventual | porta com (Rw 25) — conjunto de 25,5 dB, energia 25 | parede CEGSA, 44 dB                      | era a por passagem da casa, e não era a saída                                      |
| Hall + garagem                        | porta com — 36,9 dB, energia 35                     | PDS isolada vedada — 36,9 dB             | porta entre garagem e casa tem dupla função para ser móbica                        |
| Banho compartilhado + circulação      | não havia porta                                     | PDS isolada vedada — 35,7 dB, energia 25 | único acesso do banho, e abria para fora                                           |
| Bloco do chuveiro                     | encostado na parede do hall                         | canto arredondado, toldo e janela alta   | consequência da porta nova, a regra dos 900 cm de box obrigou a primeira tentativa |

TABELAS ADOTADAS

| ITEM                            | VALOR     | FONTE                                          |
|---------------------------------|-----------|------------------------------------------------|
| Fonte: caixa sanitária          | 75 dB(A)  | prática corrente de acústica                   |
| Fonte: bloco do chuveiro        | 75 dB(A)  | prática corrente de acústica                   |
| Fonte: cozinha e gourmet        | 75 dB(A)  | prática corrente de acústica                   |
| Fonte: sala e jantar            | 75 dB(A)  | prática corrente de acústica                   |
| Fonte: garagem                  | 75 dB(A)  | prática corrente de acústica                   |
| Fonte: máquina de lavar e secar | 75 dB(A)  | prática corrente de acústica                   |
| Fonte: oficina                  | 85 dB(A)  | prática corrente de acústica                   |
| Límite: banho                   | 45 dB(A)  | NBR 15102:2017 (circulação e entrada adotadas) |
| Límite: circulação              | 45 dB(A)  | NBR 15102:2017 (circulação e entrada adotadas) |
| Límite: cozinha                 | 45 dB(A)  | NBR 15102:2017 (circulação e entrada adotadas) |
| Límite: depósito                | 55 dB(A)  | NBR 15102:2017 (circulação e entrada adotadas) |
| Límite: dormitório              | 35 dB(A)  | NBR 15102:2017 (circulação e entrada adotadas) |
| Límite: entrada                 | 45 dB(A)  | NBR 15102:2017 (circulação e entrada adotadas) |
| Límite: estar                   | 45 dB(A)  | NBR 15102:2017 (circulação e entrada adotadas) |
| Límite: garagem                 | 55 dB(A)  | NBR 15102:2017 (circulação e entrada adotadas) |
| Límite: office                  | 45 dB(A)  | NBR 15102:2017 (circulação e entrada adotadas) |
| Límite: oficina                 | 55 dB(A)  | NBR 15102:2017 (circulação e entrada adotadas) |
| Límite: serviço                 | 55 dB(A)  | NBR 15102:2017 (circulação e entrada adotadas) |
| Fonte: academia                 | Pin 25 dB | Nota de mercado declarada                      |
| Fonte: cinema                   | Pin 25 dB | Nota de mercado declarada                      |
| Fonte: sala                     | Pin 25 dB | Nota de mercado declarada                      |
| Fonte: sala de                  | Pin 25 dB | Nota de mercado declarada                      |
| Fonte: sala de visita           | Pin 30 dB | Nota de mercado declarada                      |

NOTAS

1 Esta planilha existe porque o proprietário perguntou o que 100 verificações não sabem responder: quem entra na casa ouve o chuveiro do banho da entrada?

2 Ouviu. A parede era box (Pin 1, Pin 44) e a porta era de correr (Rw 25), o conjunto entregava 20 dB. Em acústica o eixo físico DOMINA — não se faz média aritmética do isolamento, se soma energia que passa.

3 Isolamento ou se engei ENTRE, mas... Dentro da file social o ruído não é definido, é o programa.

4 O adotado igual ao R52 (comprimento declarado), não o pre-verificação de projeto, não erro do corpo da NBR 15107-3.

PROJETO PORTO REAL

RESIDENCIA UNIFAMILIAR (MANSÃO - AM) | SOBR TATIANA-PS

PROJETO ARQUITETÔNICO

DESEMPENHO ACUSTICO ENTRE AMBIENTES

|                     |                       |                        |               |
|---------------------|-----------------------|------------------------|---------------|
| BASE GEOMÉTRICA     | ESCALA                | EMISSÃO                | PROVA         |
| Lista Consolidada   | s/ escala             | ESTUDO PRELIMINAR R52  |               |
| Pin R52 (previsão)  | FORMATO A1            | NAO LIBERADO PARA OBRA | 39            |
| UNIDADE MÉTRICA: mm | MILIMETROS (60/50/50) | SEM ART / RNT          | 06.48 REV R52 |