


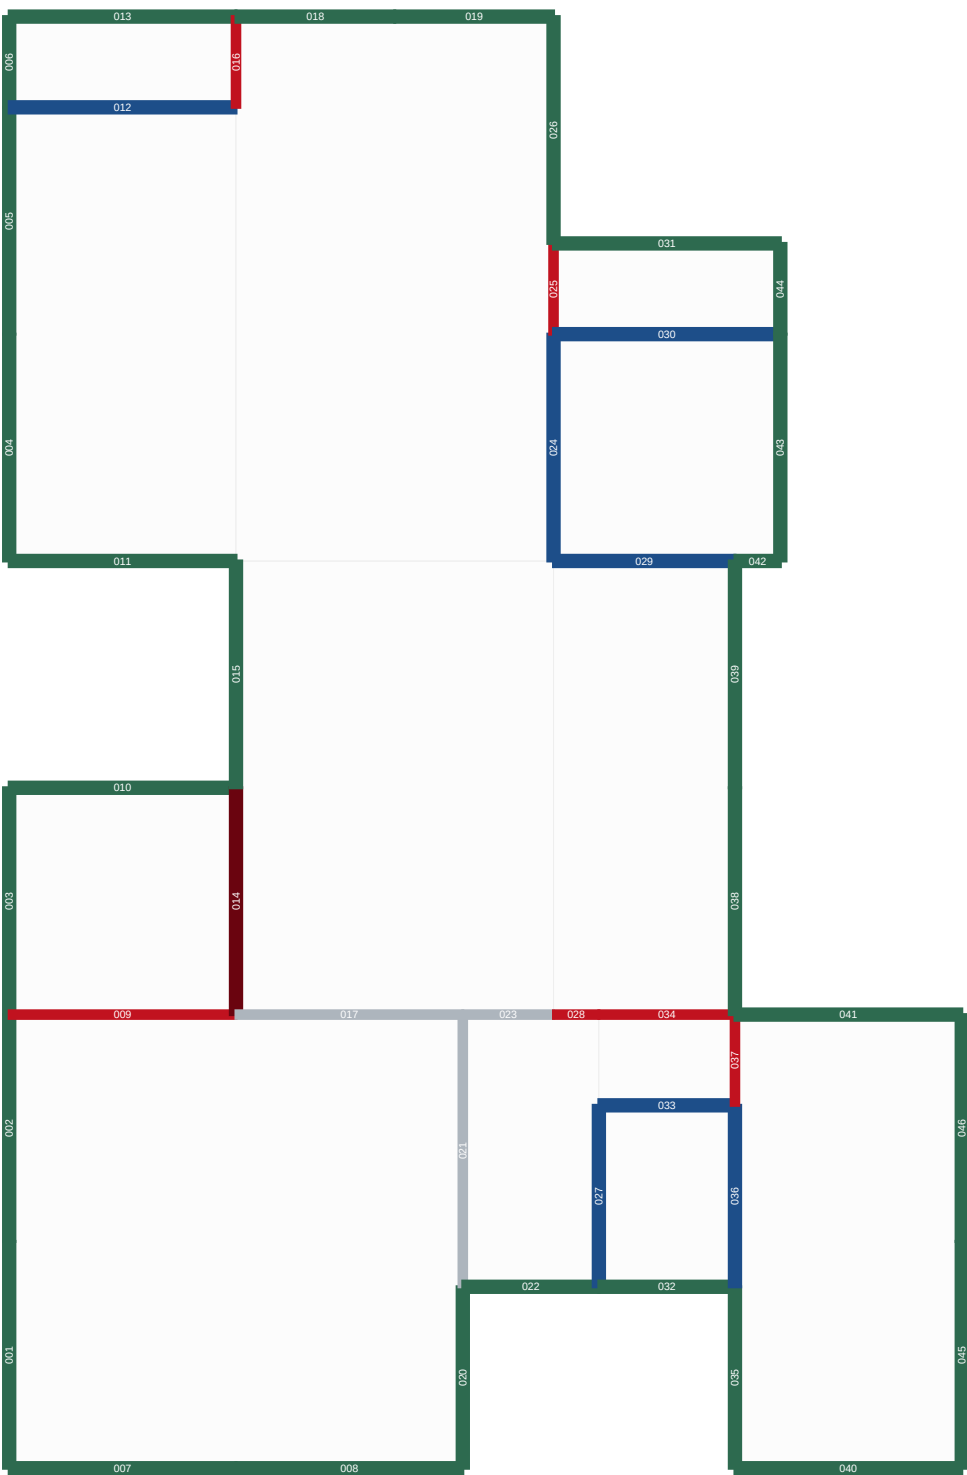

1 PAGINACAO — TERREO
ESCALA 1:100

QUANTITATIVO DE PAINES E MONTANTES

FAMILIA	PAINES	MONTANTES	MT DE PERÍ	COMPOSICAO
PA-1	12	45	127,4	dupla chapa 12,5 + montante 45 x 14 x 60 + dupla chapa 12,5
PA-2	1	6	15,6	dupla chapa 12,5 + perfil isolante + montante 70 x 14 x 60
PE-1	46	243	631,8	linhas 32 x 30 x 50 (SD) encaixe + montante 90 x 14 x 50 +
PA-3	7	37	96,2	gesso 60 x 12,5 + montante 90 x 14 x 50 + gesso 12,5 + reboco
PA-1	3	16	41,8	gesso 12,5 + montante 70 x 14 x 50 + gesso 12,5
TOTAL	69	361	912,6	



EXTRATO DA LISTA DE PAINES (26 de 69)

CODIGO	FAMILIA	LARG (mm)	ALT (mm)	MONT.	PRV
PT-001	PE-1	3000	2000	6	T
PT-002	PE-1	3000	2000	6	T
PT-003	PE-1	3000	2000	6	T
PT-004	PE-1	3000	2000	6	T
PT-005	PE-2	3000	2000	6	T
PT-006	PE-1	1200	2000	3	T
PT-007	PE-1	3000	2000	6	T
PT-008	PE-1	3000	2000	6	T
PT-009	PA-1	3000	2000	6	T
PT-010	PE-1	3000	2000	6	T
PT-011	PE-1	3000	2000	6	T
PT-012	PA-1	3000	2000	6	T
PT-013	PE-1	3000	2000	6	T
PT-014	PA-2	3000	2000	6	T
PT-015	PE-1	3000	2000	6	T
PT-016	PA-1	1200	2000	3	T
PT-017	PA-1	3000	2000	6	T
PT-018	PE-2	2100	2000	4	T
PT-019	PE-1	2100	2000	4	T
PT-020	PE-1	2400	2000	5	T
PT-021	PA-1	3000	2000	7	T
PT-022	PE-1	1800	2000	4	T
PT-023	PA-1	1200	2000	3	T
PT-024	PA-1	3000	2000	6	T
PT-025	PA-1	1200	2000	3	T
PT-026	PE-1	3000	2000	6	T

- NOTAS
- * Painéis limitados a 3000 mm por manuseio e transporte.
 - * Montantes a cada 600 mm, 400 mm onde cabido no revestimento exigido.
 - * Não incluir peça entre em revestir sem código, largura, altura, espessura, material e revestir.
 - * Numeração por pavimento, a família define a composição interna do painel.

PROJETO PORTO REAL

RESIDENCIA UNIFAMILIAR (MANAUS - AM) | SOUZA TATIANA-PS

PROJETO ARQUITETONICO

PAGINACAO DE PAINES — LIGHT STEEL FRAME

BASE GEOMETRICA Linha Consolidada Projeto (previsão) UNIDADE: METROS (m)	ESCALA 1:100 FORMATO: A1 MILHA: 600/500/300	EMISSAO ESTUDIO PRELIMINAR Linha Libertado PARA ORCA SEM ART / RNT	PROJETO 18 05/23
---	--	---	------------------------