


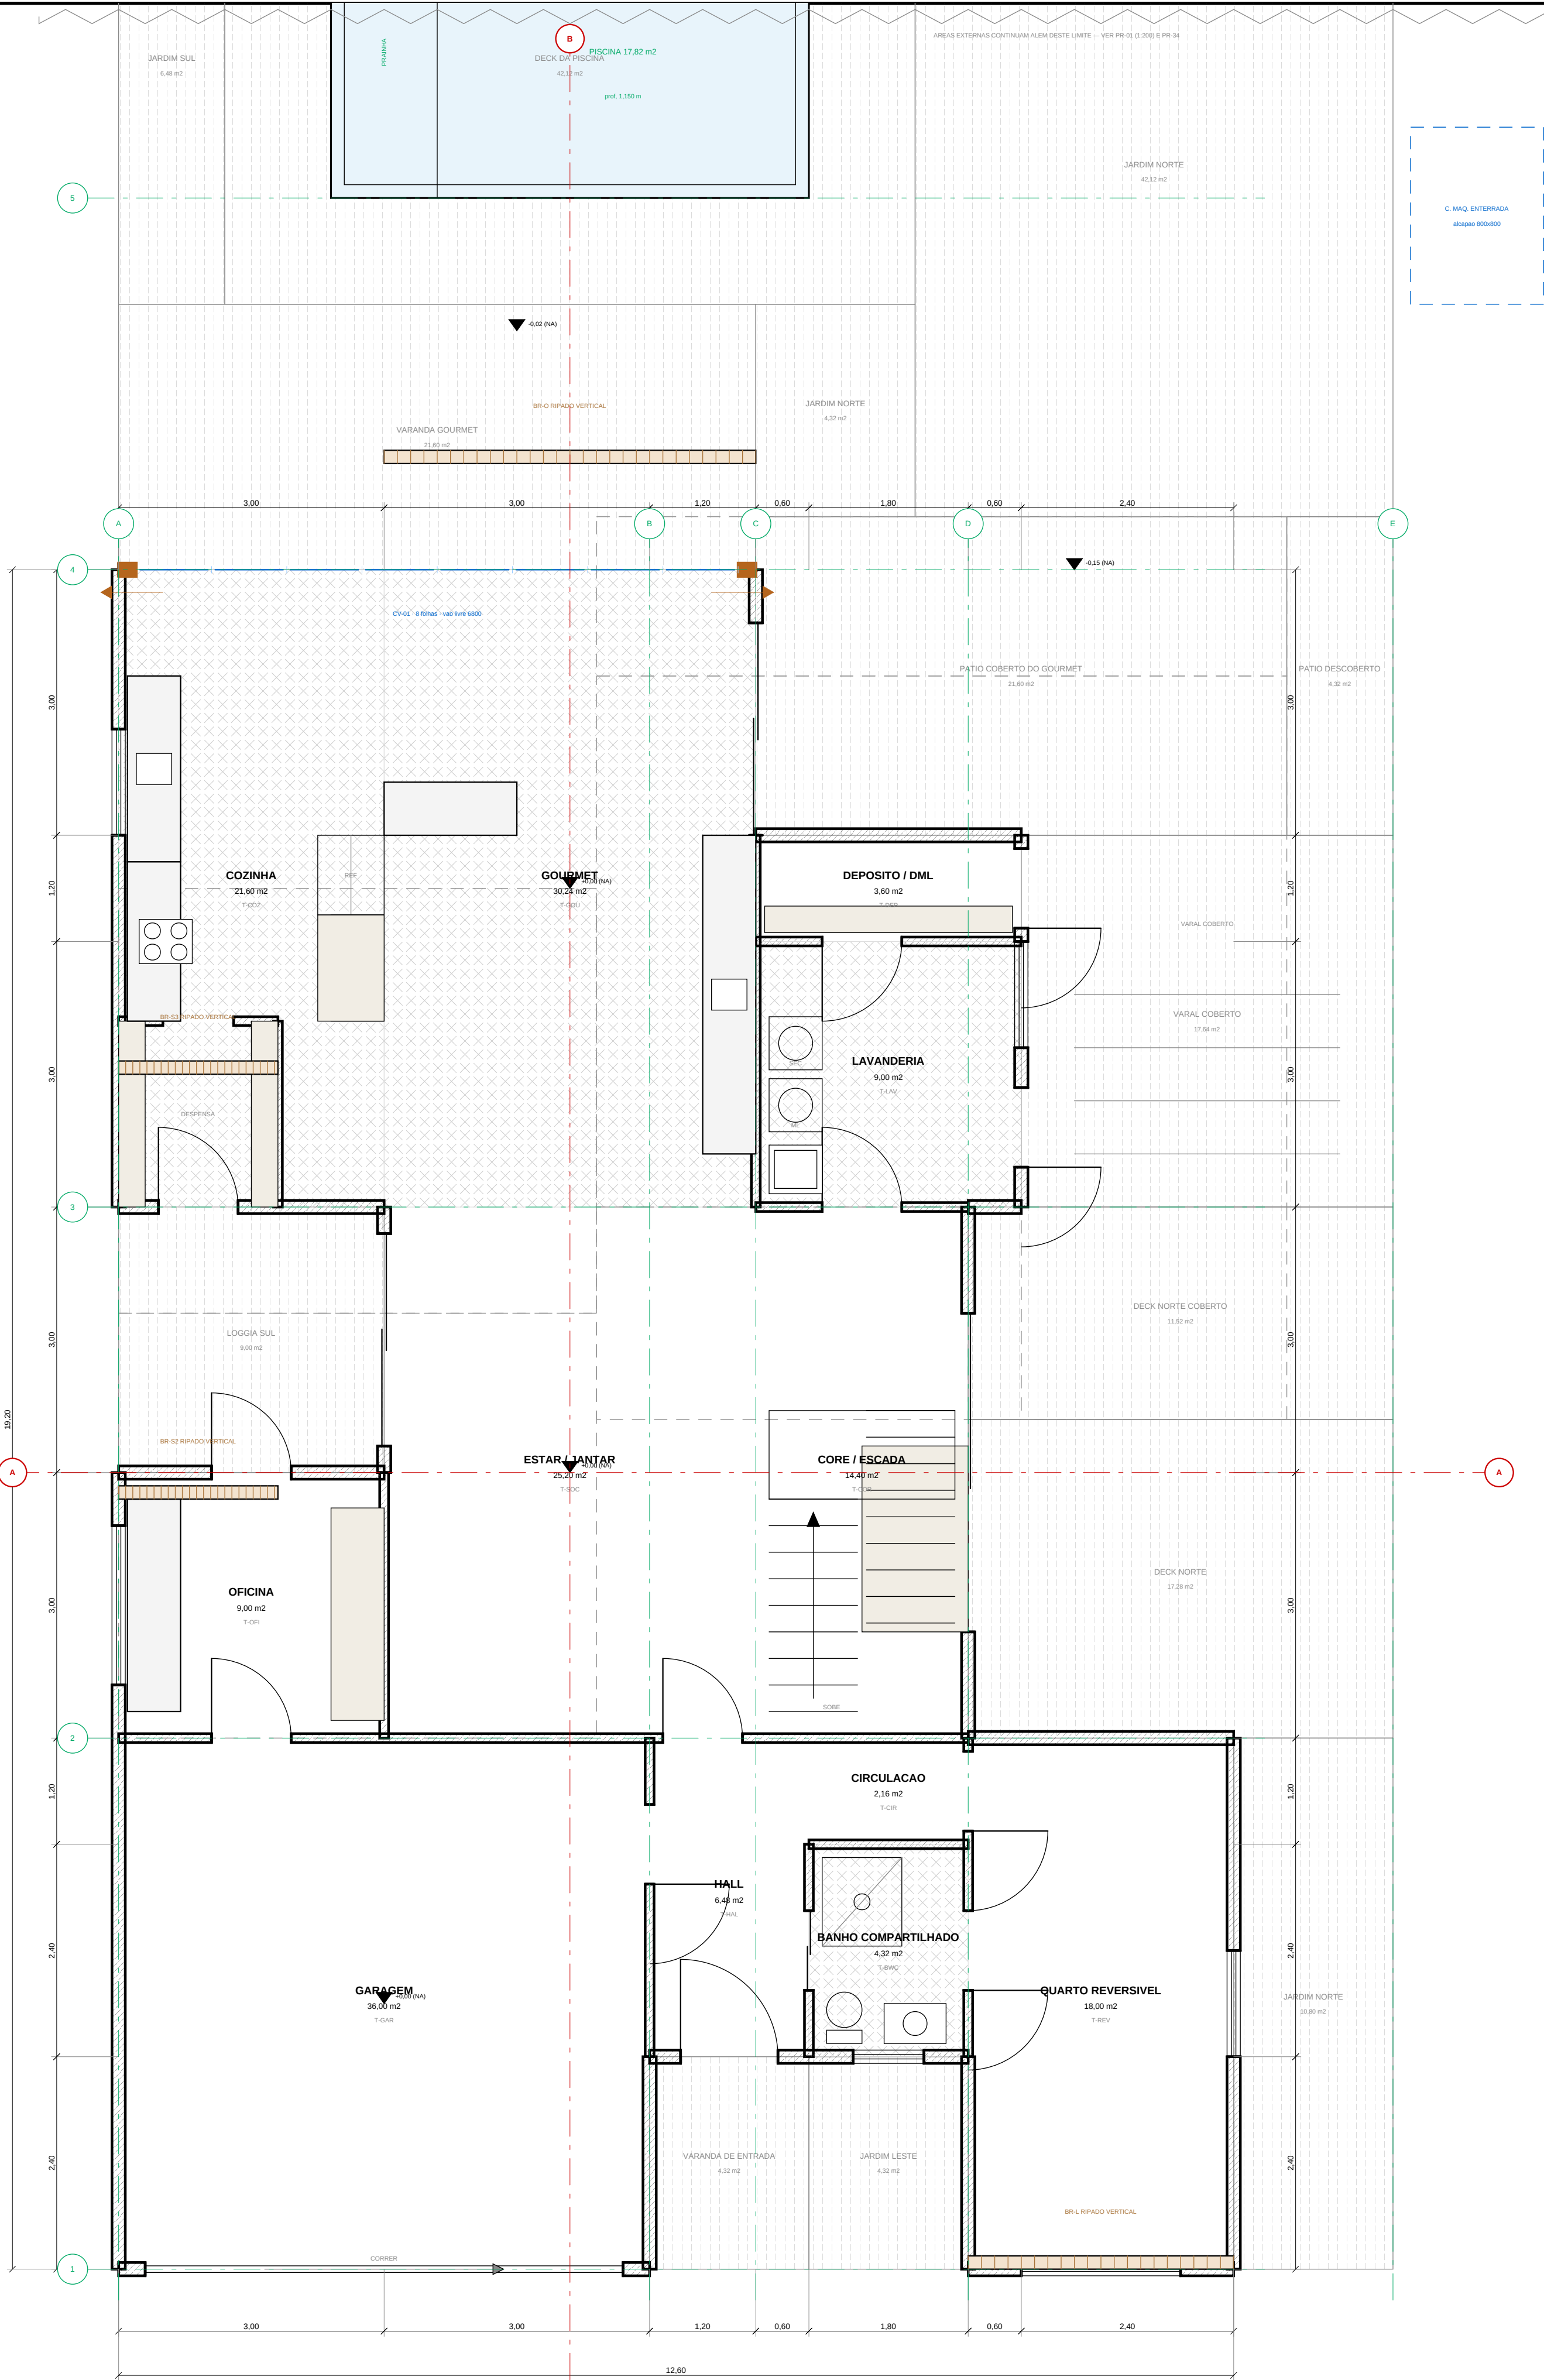

1 PAVIMENTO TERREO
ESCALA 1:50



QUADRO DE ÁREAS — PAVIMENTO TERREO

COD	AMBIENTE	MODULO (mm)	AREA (m²)
T-GAR	CARACEM	600x600	36,00
T-HAL	HALL	1800x3000	5,40
T-BNC	BANHO COMPARTILHADO	1800x2400	4,32
T-COR	CIRCULACAO	1800x1200	2,16
T-REV	QUARTO REVERSIVEL	3000x3000	9,00
T-OFI	OFICINA	3000x3000	9,00
T-SOC	ESTAR/JANTAR	4500x6000	27,00
T-COR	CORE/ESCADA	2400x6000	14,40
T-COZ	COZINHA	3000x2700	21,60
T-GOU	GOURMET	4500x2700	36,24
T-LAV	LAVANDERIA	3000x3000	9,00
T-DEP	DEPOSITO/DML	3000x1200	3,60
TOTAL FECHADO			198,00
T-VAR	VARANDA DE ENTRADA (aberta)	1800x2400	4,32
T-J-E	JARDIM LESTE (aberto)	1800x600	4,32
T-J-N	JARDIM NORTE (aberto)	1800x3000	15,00
T-LOG	LOGGIA SUL (aberto)	3000x3000	9,00
T-DML	DECK NORTE (aberto)	4800x3000	17,28
T-DNC	DECK NORTE COBERTO (aberto)	4800x2400	11,52
T-VAR	VARAL COBERTO (aberto)	4500x4500	17,64
T-PAT	PATIO COBERTO DO GOURMET (aberto)	6000x3600	21,60
T-PAT	PATIO DESCOBERTO (aberto)	1200x3000	4,32
T-VAR	VARANDA GOURMET (aberto)	7500x3600	27,00
T-DEP	DECK DA PISCINA (aberto)	7800x4500	42,12
T-J-S	JARDIM SUL (aberto)	1200x600	6,48
T-J-N	JARDIM NORTE (aberto)	1800x2400	4,32
T-J-N	JARDIM NORTE (aberto)	5400x7800	42,12
T-PAT	JARDIM DE FUNDO (aberto)	14800x4800	69,12


MAPA DE ESQUADRIAS DO PAVIMENTO

REF	VALOR (mm)	QUANT.	QTD.	TIPO
CW1	7000x2800	0	1	CORTINA DE VIDRO vertical, 0 folha de 900 mm
J1	1200x1200	1200	3	porta de banheiro, alumínio
J4	800x800	1800	1	porta de banheiro, alumínio
J5	1800x1200	1200	2	porta de banheiro, alumínio
P1	1100x2800	0	1	porta principal, vidro espelho
P2	3000x1200	0	4	porta interna (diversas aberturas)
P3	800x1200	0	7	porta de banheiro, alumínio
P4	900x1200	0	1	porta de banheiro, alumínio
P5	900x1200	0	1	porta de banheiro, alumínio
P6	1400x2400	0	1	porta de banheiro, alumínio
P7	3000x2400	0	1	porta de banheiro, alumínio
P8	3000x2400	0	2	porta de banheiro, alumínio

LEGENDA E CONVENCOES (NBR 6492 / 8403)

—	Elemento seccionado pelo plano de corte (h = 1,50 m)
—	Área útil / área de ocupação
—	Mobiliário fixo, equipamento e tecnologia
—	Propriedade do pavimento superior e da cobertura
—	Elemento móvel e linha de corte
—	Limite da sala e linha auxiliar

PERCURSO SOLAR — MANUS 1.5

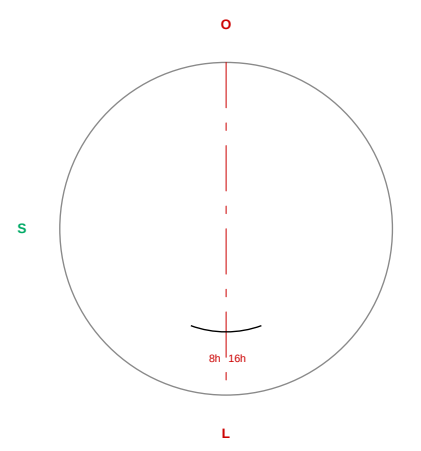

Nota: 1:50 m e 1:50 m
= escala para o projeto
Nota: 1:50 m e 1:50 m
= escala para o projeto

NOTAS

- Dimensões em milímetros, cotas de nível em metros.
- Malha modular 600 mm, cotas em 6 mm.
- Planta externa 120 mm / planta interna 120 mm (1:50).
- Modular fixo indica pontos de água e energia (NBR 6492).

PROJETO PORTO REAL

RESIDENCIA UNIFAMILIAR (MANUS - AM) (SOL TARTARUGA)

PROJETO ARQUITETONICO

PLANTA BAIXA — PAVIMENTO TERREO

BASE GEOMETRICA

União Consolidada

PROJETO (previsão)

UNIDADE METRICA: mm

ESCALA

1:50

FORMATO A1

MAQUETA 600x900mm

EMISSAO

ESTUDO PRELIMINAR R34

TRABALHO PARA OBRAS

SEM ART / RNT

PROJETO

02

06-25 REV04