


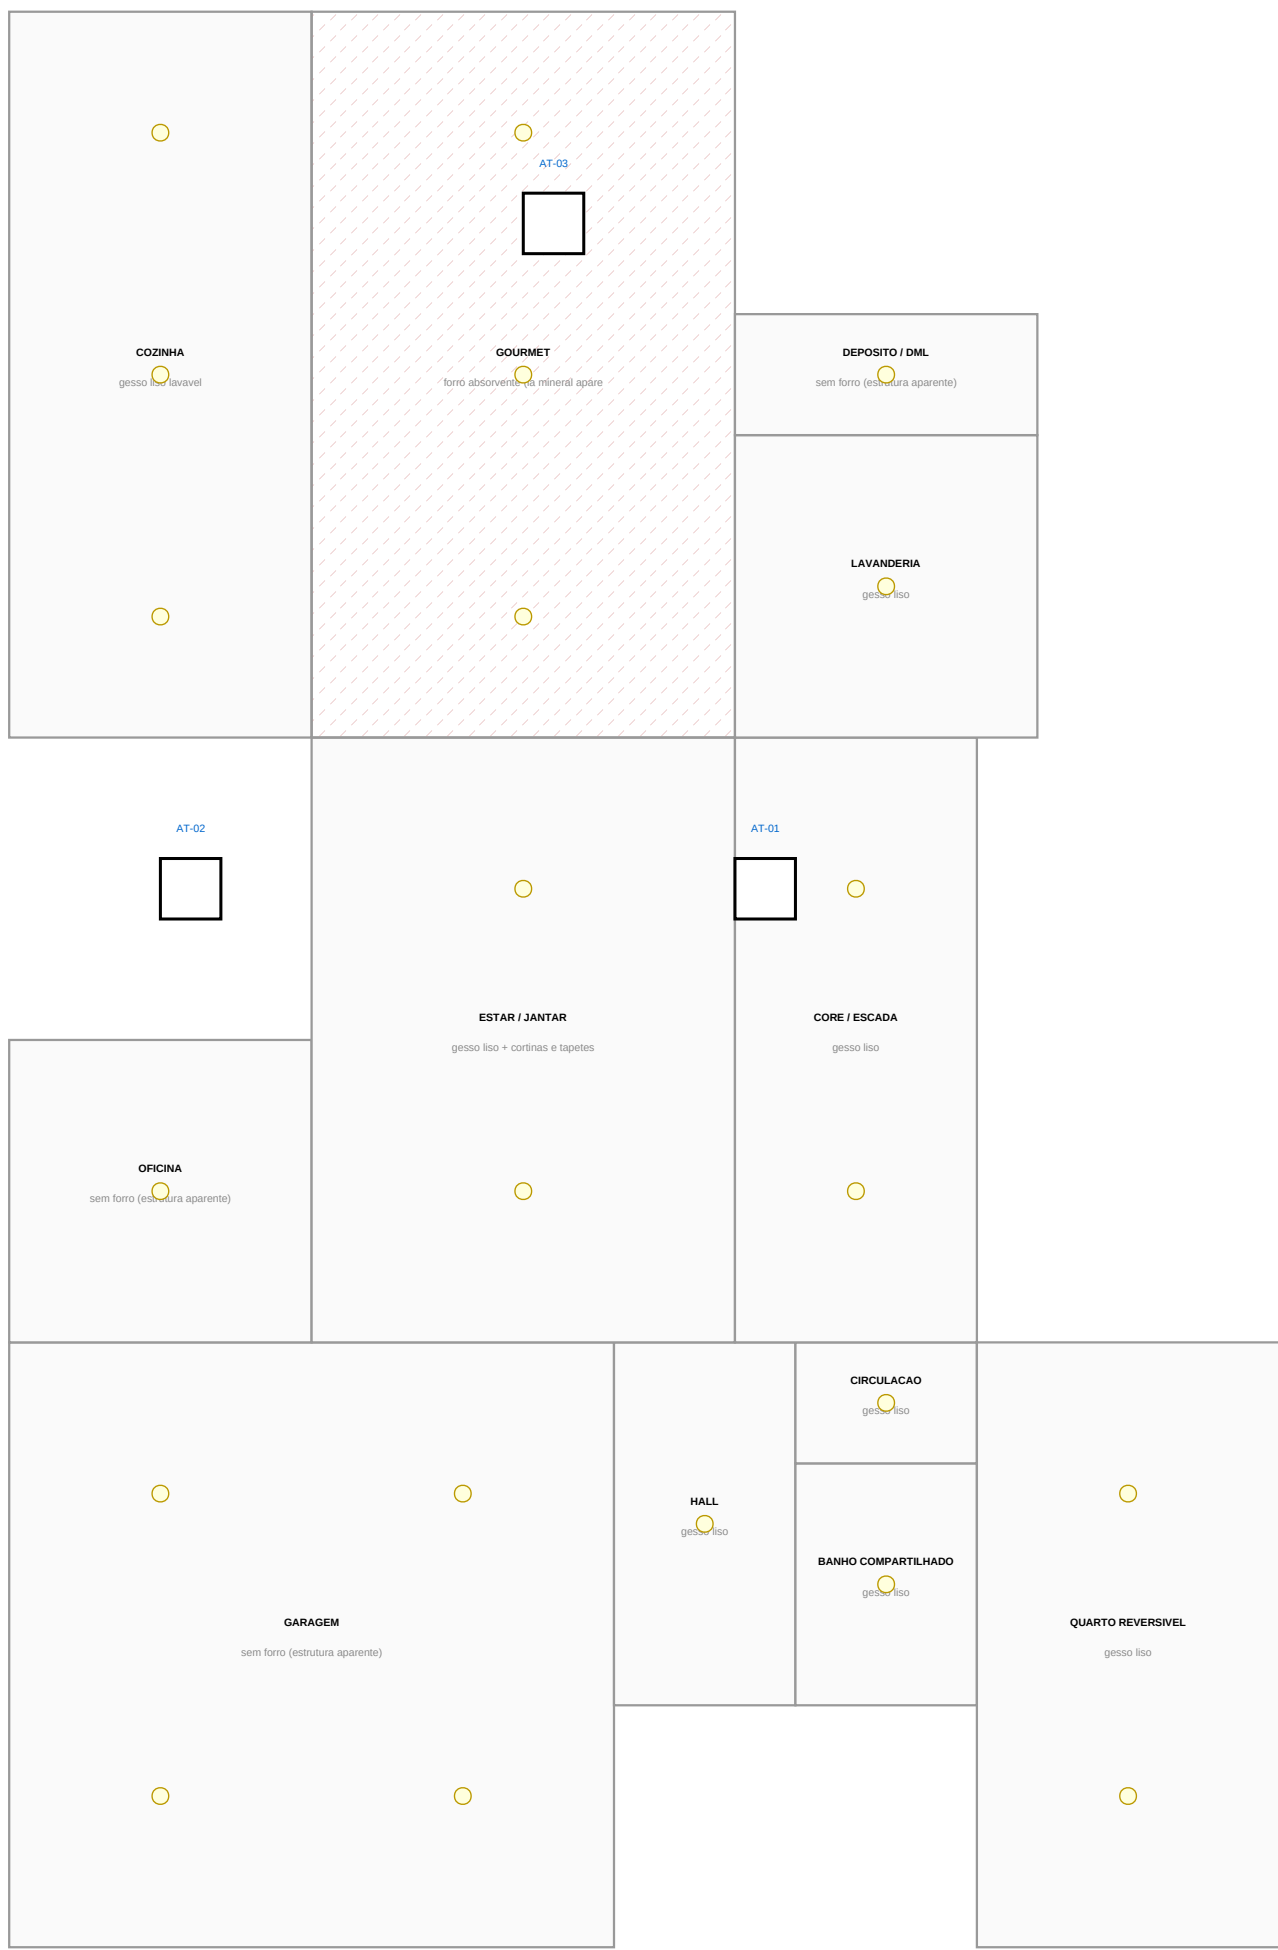

1 FORRO REFLETIDO — TERREO
ESCALA 1:75

- luminária embutida, 3.000 K, RSC 90
- luz técnica 600 x 600 mm
- forro absorvente (alfa 0,70)

FORROS POR AMBIENTE

AMBIENTE	SOLUÇÃO	ÁREA	NOTAS
T-001	forro absorvente (alfa 0,70) em todo o perímetro	36,24	único ponto que demanda a instalação de 3,20 x 3,20 m
T-002	gesso forro + pintura e iluminação	25,20	abertura para o mobiliário, forro branco e luzes
T-003	gesso forro branco	18,00	superfície de fácil limpeza sem necessidade de manutenção
T-004	gesso forro + iluminação sobre o forro	25,80	o forro e o teto devem estar de acordo com o projeto
T-005	gesso forro + iluminação sobre o forro	25,80	idem
T-006	gesso forro + iluminação sobre o forro	25,80	idem
T-007	sem forro (estrutura aparente)	36,00	ambiente com madeira escura sem forro
T-008	sem forro (estrutura aparente)	9,00	idem
T-009	sem forro (estrutura aparente)	3,00	idem

- NOTAS
- Planta refletida: vista do forro projetada no plano horizontal.
 - Forro absorvente apenas no gourmet — único ponto com necessidade crítica.
 - Alçapão técnico de 600 x 600 mm, passando de cobertura de 600 mm.
 - Luminária geral 3.000 K, RSC modelo 90.

PROJETO PORTO REAL

RESIDÊNCIA UNIFAMILIAR (MANSÃO - AM) | SOBR TATIANA-PS

PROJETO ARQUITETÔNICO

PLANTA DE FORRO E ILUMINAÇÃO

BASE GEOMÉTRICA Linha Consolidada Projeto (previsão) UNIDADE: METROS - MM	ESCALA 1:75 FORMATO: A1 MATERIAL: 600x600/300	EMISSÃO ESTUDO PRELIMINAR R34 Linha Consolidada PARA OBRAS SEM ART / RNT	PROJETO 16 06-25 REV 004
--	--	---	--------------------------------