
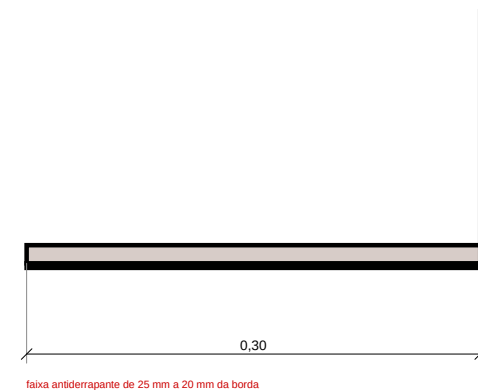
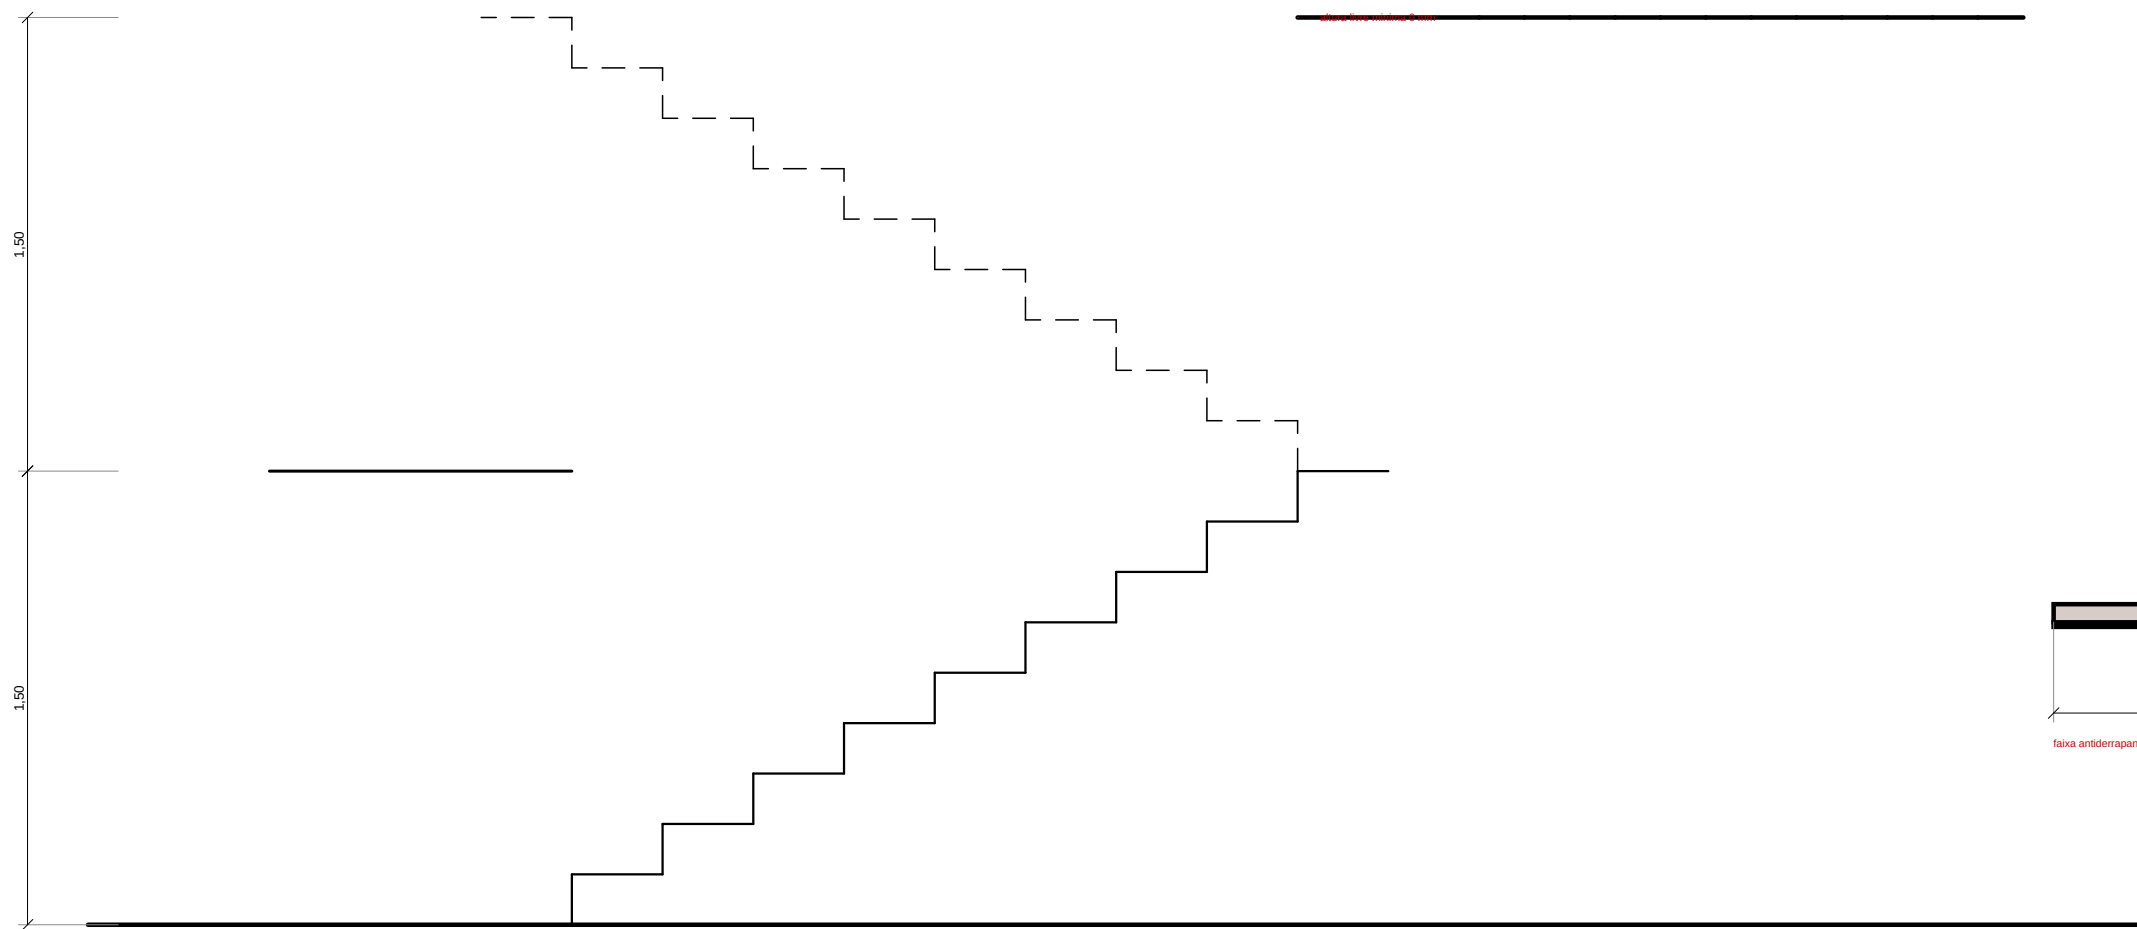
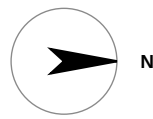


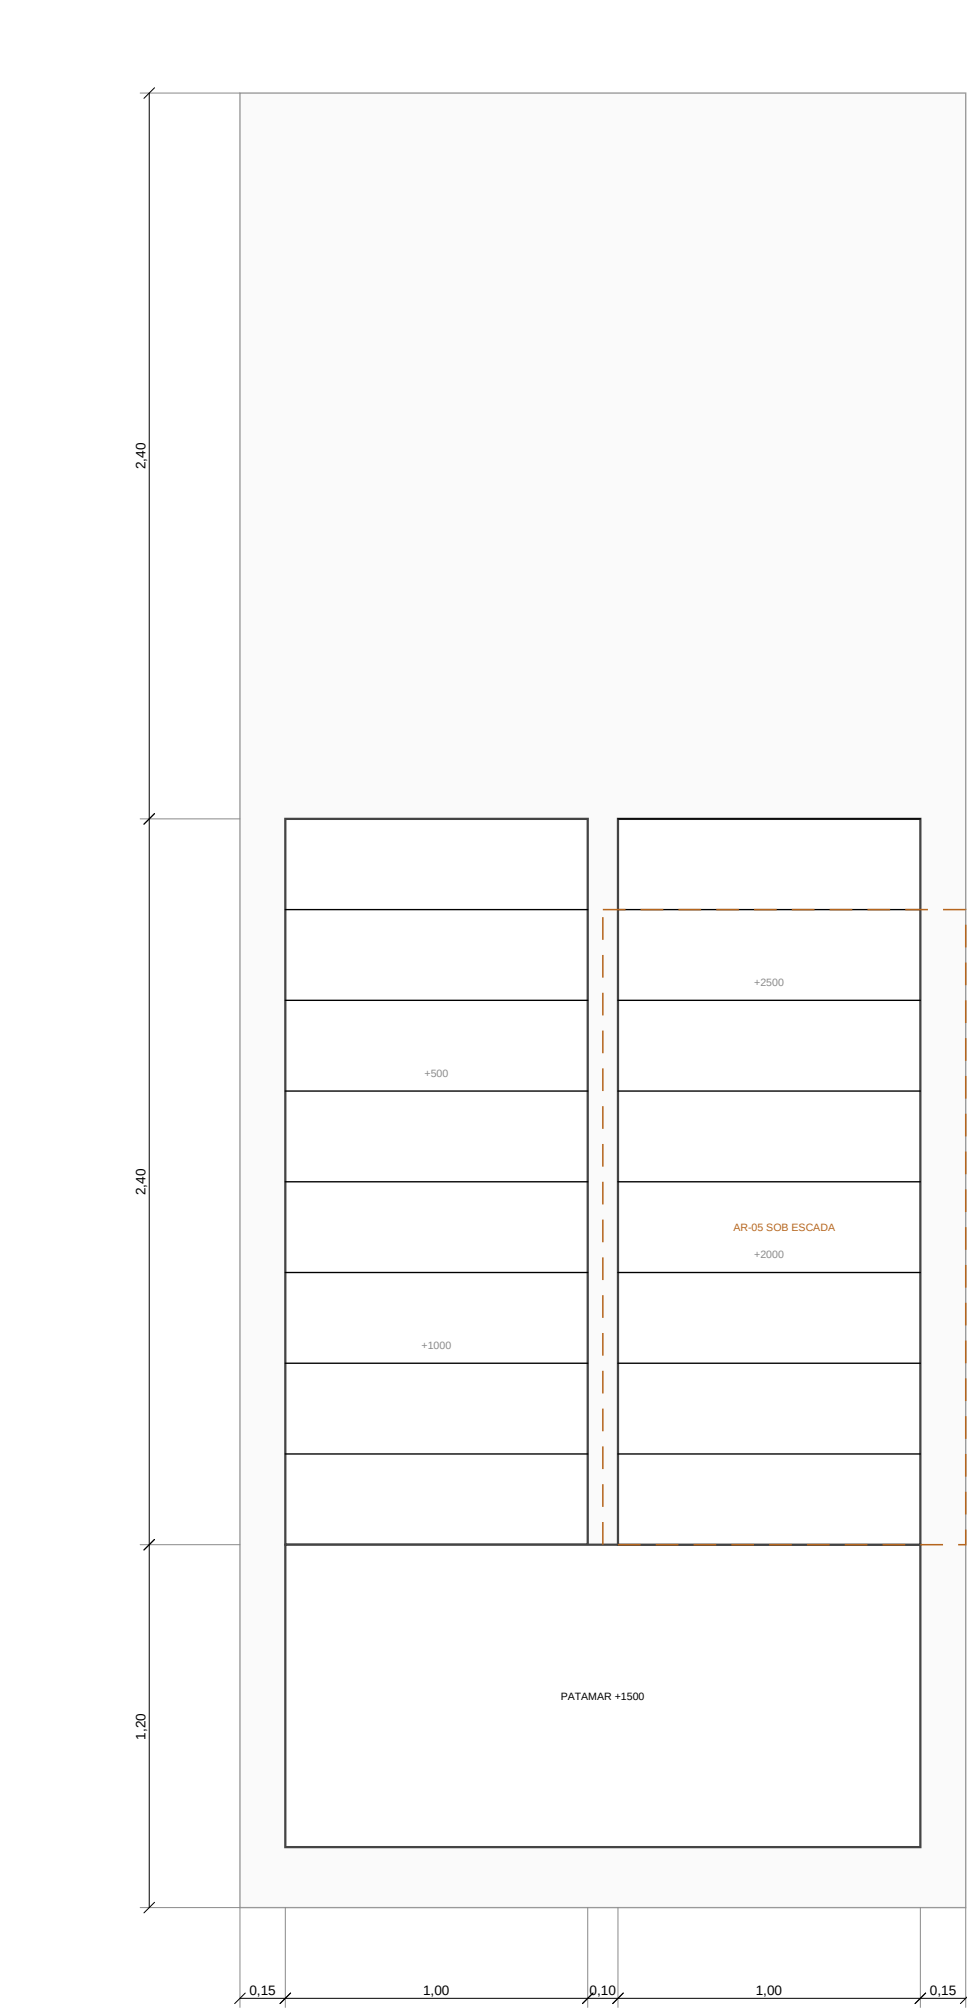

espelho fechado (NBR 9050)

chapa 800x400 3 mm + preenchido 900 x 300

1 PLANTA DA ESCADA ESCALA 1:25

VERIFICACAO DA ESCADA

ITEM	PROPOSTO	NORMA	
Espelho	186,67 mm	18 a 18 cm (NBR 9077)	OK
Piso	300 mm	mín 28 cm	OK
Bondex (2h + g)	633,3 mm	600 a 650 mm	OK
Largura útil do lance	1000 mm	mín 1.200 mm (para edifícios) e 1.000 mm (para vilas)	OK
Platamar	1000 mm	— largura do lance	OK
Altura livre mínima	0 mm	mín 2100 mm	RECEI
Guarda-corpo	1100 mm	mín 1.200 mm (NBR 14738)	OK
Corrimão	920 x 700 mm	Acabado 92 cm x 70 cm (NBR 9050)	OK
Espelho fechado	sem	congelamento em vidro acrílico	OK
Desnível vencido	3000 mm	18 x 186,67 mm	OK

O QUE A PLANTA NAO MOSTRA

QUESTAO	RESPOSTA
Por que o primeiro espelho sobre de y = 1,90m?	o primeiro espelho sobre de y = 1,90m, com 1.000 mm de altura livre — sobre a altura da cobertura do primeiro lance
Por que a verificação de altura livre e bidimensional?	altura livre da escada e o único critério que não aparece em planta horizontal, dependendo da cor da escada e da cor do que há acima dela
O que há sob o segundo lance?	interseção com altura útil variável, destinada como amarração (NBR 9050) — não é circulação nem espaço morto
Por que espelho fechado?	alguma vez usado para a porta do por de quem usa bengala ou tem mobilidade reduzida (NBR 9050)
Por que corrimão duplo?	920 mm para adulto e 700 mm para criança, em caso de escada aberta para a sala, o segundo corrimão é o que realmente se usa

NOTAS

- 18 espelho de 186,67 mm e piso de 300 mm. Bondex 2h + g = 633,3 mm (falso recomendado 600 a 650).
- Altura livre mínima 2100 mm (NBR 9077), verificada diagonal a degrau contra a tape e o resto acima.
- Guarda-corpo 1100 mm, corrimão duplo em 920 x 700 mm (NBR 9050).
- dois perfis U 200 laterais com degrau em chapa aluminada 3 mm.

PROJETO PORTO REAL

RESIDENCIA UNIFAMILIAR (MARIAUS - AM) | 500x700mm (P)

PROJETO ARQUITETONICO

ESCALA — DESENHO EXECUTIVO

BASE GEOMETRICA	ESCALA	EMISSAO	PROJECOA
Unidade Consolidada	indicada	ESTUDIO PRELIMINAR R34	25
Projeto (previsão)	FORMATO A1	NAO LIBERADO PARA OBRA	SEM ART / RNT
Unidade (previsão)	MAQUETA 600x900mm	SEM ART / RNT	06-25 REV 034