


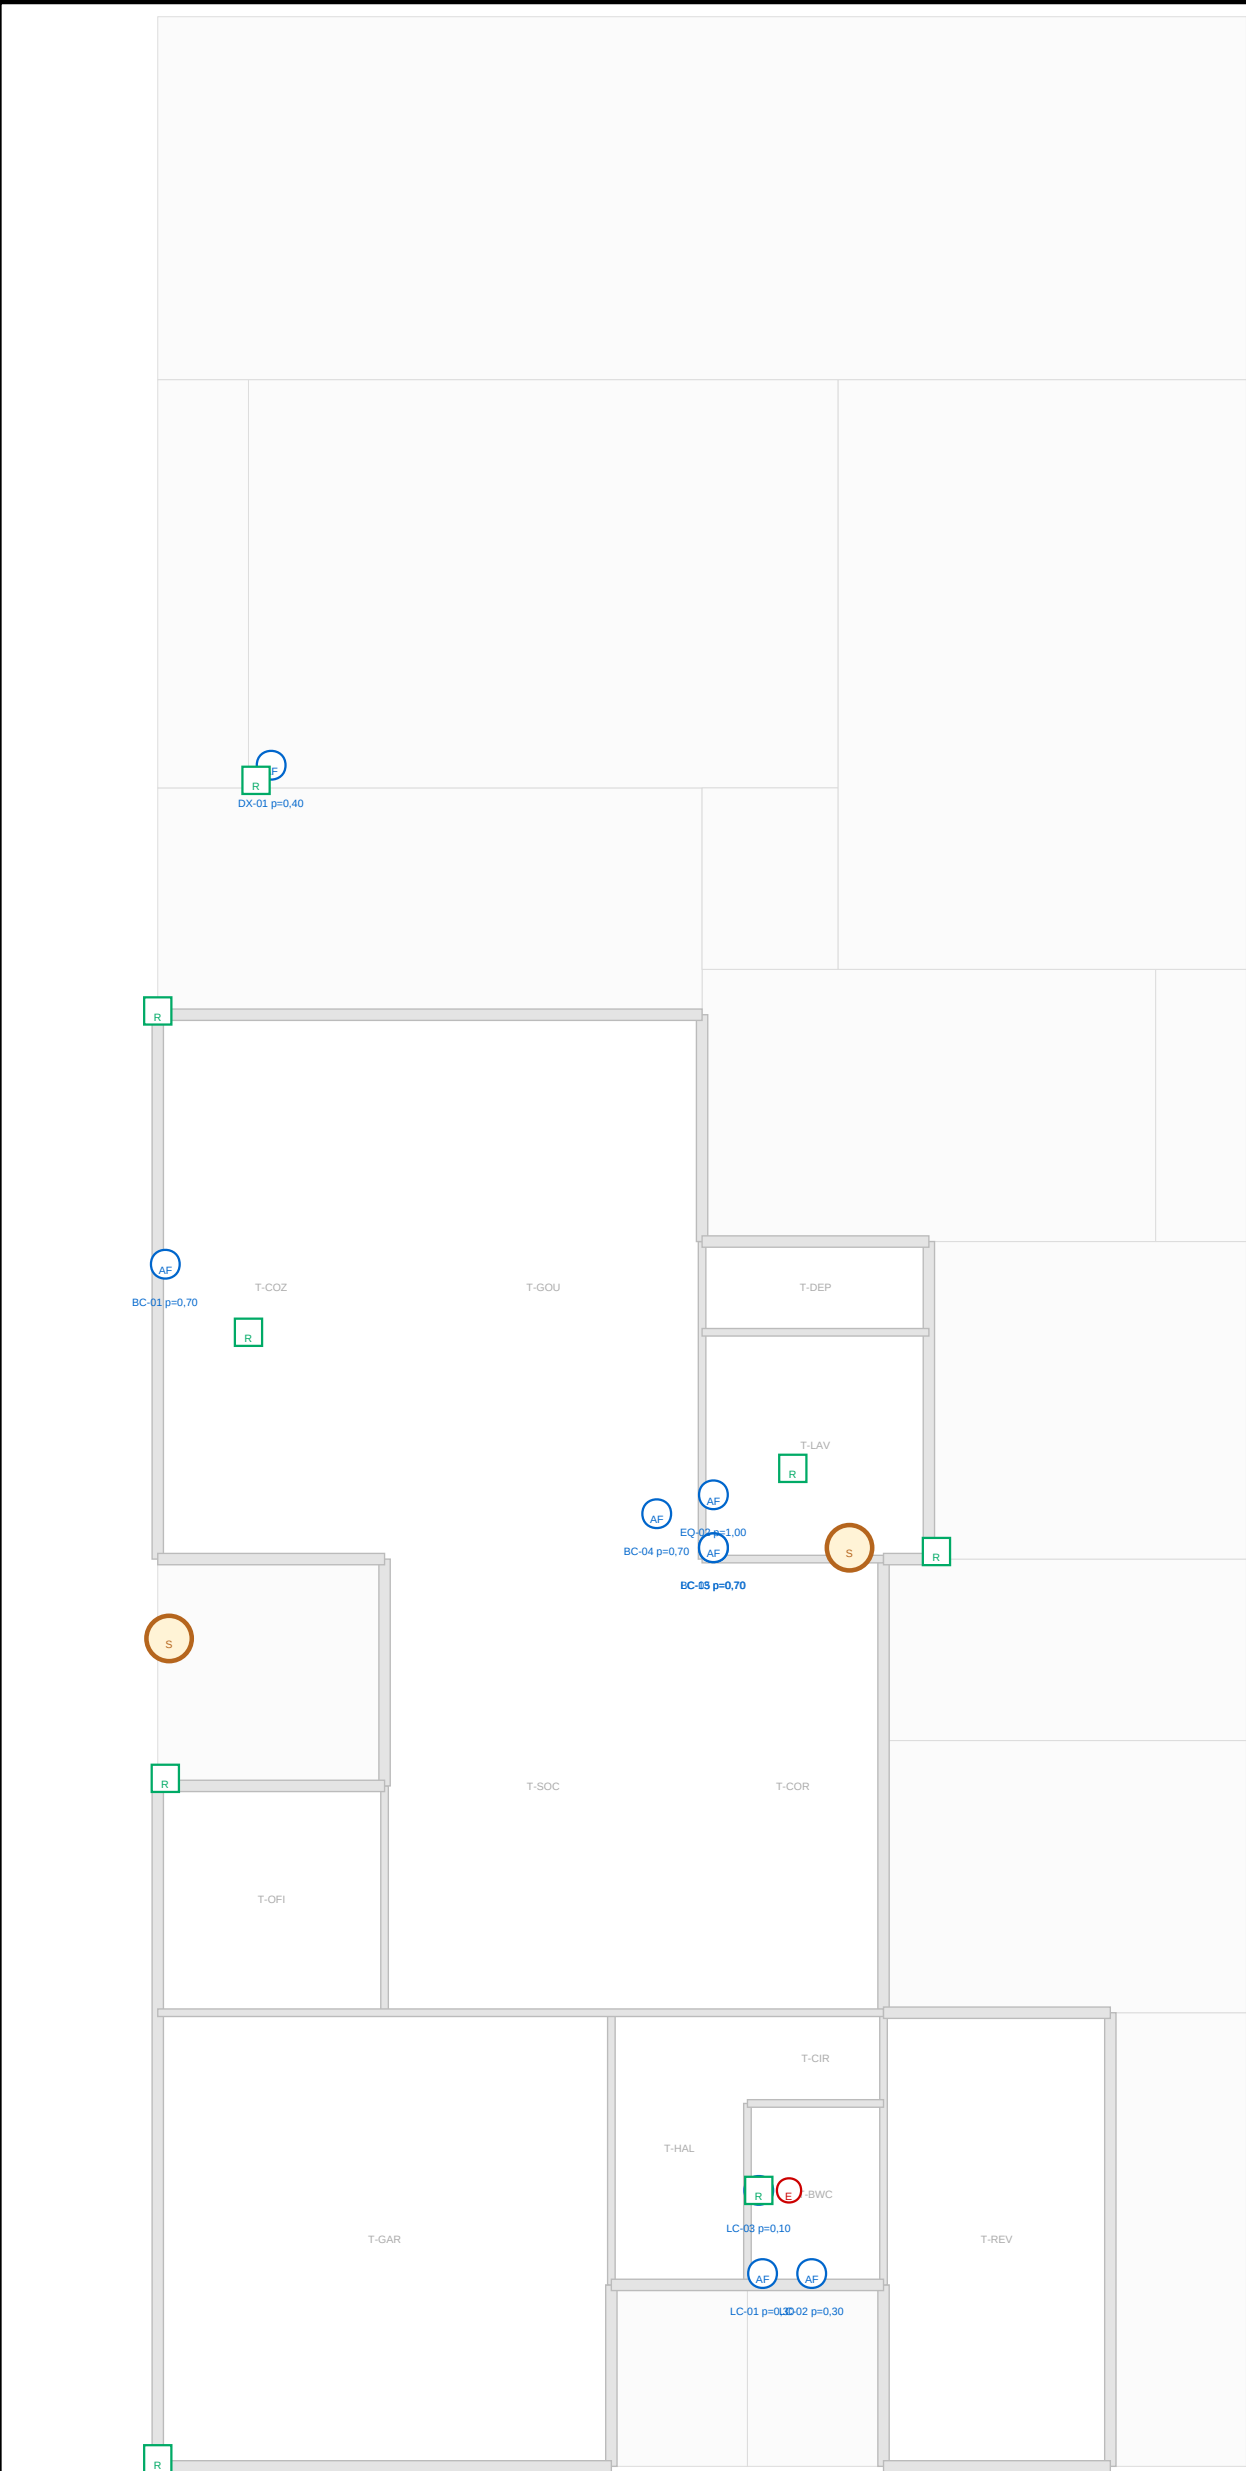


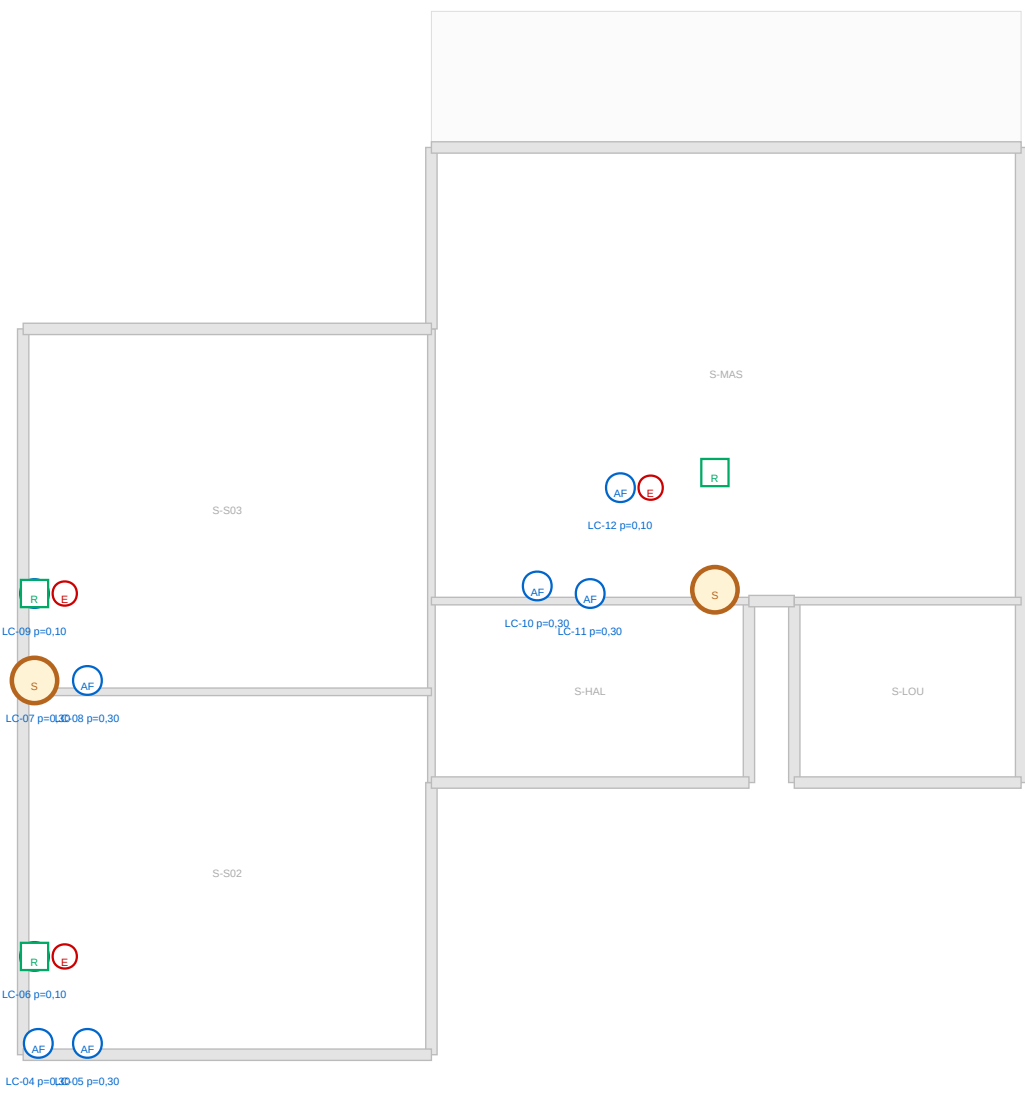

1 PONTOS HIDRAULICOS — TERREO
ESCALA 1:100

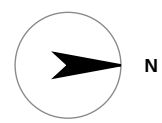

2 PONTOS HIDRAULICOS — SUPERIOR
ESCALA 1:100

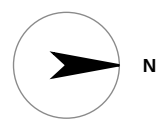

DIMENSIONAMENTO — AGUA FRIA E ESGOTO

TRECHO	PECAS	PESOS	Q (L/s)	DN AGUA	V (m/s)	UMC	DN ESGOTO	REGIME
Superior	8	2.10	0.435	DN25	1.19	27	DN100	pressurizado
Térreo	9	4.80	0.984	DN25	1.81	36	DN100	gravidade
GERAL	18	7.00	0.794	DN25	1.31	33	DN100	gravidade

DECISÖES QUE O DIAMETRO REVELA

DECISAO	CONSEQUENCIA HIDRAULICA
Chuveiro elétrico em vez de aquecimento central	pressão 0.02 por chuveiro em vez de 0.40; a soma cai de 8.2 para 7.0 pesos e o alimentador de DN60 para DN52
Limite de velocidade por conforto, não por norma	DN25 elevando a soma a 2.07 m/s a 3.0 m/s e não nas básicas. Custa alguns metros de tubo
Pressurizador no ramal superior	0.5 mca por gravidade nos setores chuveiro elétrico, TC-14 entrega 12 mca
Ramais planejados sem ligação a valas	rede de rede e flocamento separada, com cot e identificação próprias, não há pontos de conexão cruzada possíveis
Canais de grandes áreas da impasse	cota 100 + TC-11 (DN-11) > TC-12 -> rede, DN100 com cobertura de 2%

PECAS DE UTILIZACAO

COD	AMB	TIPO	PESO	UMC	DN AF	DN ESS	QUENTE
LC-01	T-BANC	vaso	0.30	6	DN25	DN40	—
LC-02	T-BANC	banheira	0.30	1	DN25	DN40	—
LC-03	T-BANC	box	0.30	2	DN25	DN40	sim
LC-04	S-SID	vaso	0.30	6	DN25	DN40	—
LC-05	S-SID	banheira	0.30	1	DN25	DN40	—
LC-06	S-SID	box	0.30	2	DN25	DN40	sim
LC-07	S-SID	vaso	0.30	6	DN25	DN40	—
LC-08	S-SID	banheira	0.30	1	DN25	DN40	—
LC-09	S-SID	box	0.30	2	DN25	DN40	sim

(continuacao)

COD	AMB	TIPO	PESO	UMC	DN AF	DN ESS	QUENTE
LC-01	S-MAS	vaso	0.30	6	DN25	DN40	—
LC-02	S-MAS	banheira	0.30	1	DN25	DN40	—
LC-03	S-MAS	box	0.30	2	DN25	DN40	sim
LC-04	T-LAV	vaso	0.70	3	DN25	DN40	—
LC-05	T-COZ	sim	0.70	3	DN25	DN40	—
LC-06	T-COZ	sim	0.70	3	DN25	DN40	—
LC-07	T-LAV	sim	0.70	3	DN25	DN40	—
LC-08	T-LAV	banheira	1.00	3	DN25	DN40	—
LC-09	T-LAV	banheira	0.40	2	DN25	DN40	—

NOTAS

- Água fria por rede de dois pesos (DN25) Q = 0.20 e rede de dois pesos = 0.70 L/s com 7.0 pesos.
- Alimentador DN25 a 1.12 m/s — limitado pelo conforto (2.0 m/s) não pela norma (3.0 m/s).
- Exigido por UMC (DN25) DN25, tubo de queda DN100, ventilação DN60.
- Chuveiro elétrica DN25 com peso 0.10, não 0.40 a decisão de aquecimento aquecer água com diâmetro menor em toda a casa.

PROJETO PORTO REAL

RESIDENCIA UNIFAMILIAR (MANSÃO - AM) (SOL. TATIANA-PS)

PROJETO ARQUITETONICO

INSTALACOES HIDROSSANITARIAS

BASE GEOMETRICA	ESCALA	EMISSAO	PROVA
União Consolidada	1:100	ESTUDO PRELIMINAR R34	26
por R32 (previsão)	FORMATO A1	NAO LIBERADO PARA OBRA	
UNIDADE MESTRE: AM	MALHA 600/600/600	SEM ART / INT	06-25 REV 034