




luminária embuída, 3.000 K, RSC 90

afcapso técnico 600 x 600 mm

forro absorvente (alfa 0,70)

FORROS POR AMBIENTE

AMBIENTE	SOLUÇÃO	ÁREA	NOTAS
T-001	forro absorvente (α=0,70) instalado no teto	36,24	único ponto que demanda a instalação de 3,20 x 3,20 x 120
T-002	gesso liso + pintura e iluminação	25,20	abertura para iluminação, forro branco e gesso
T-003	gesso liso + pintura	18,00	superfície de fácil limpeza com pintura de alto brilho
S-001	gesso liso + la mineral sobre o forro	25,80	la sobre o forro branco e la mineral sobre o forro
S-002	gesso liso + la mineral sobre o forro	25,80	la sobre o forro branco e la mineral sobre o forro
S-003	gesso liso + la mineral sobre o forro	25,80	la sobre o forro branco e la mineral sobre o forro
S-004	gesso liso + la mineral sobre o forro	25,80	la sobre o forro branco e la mineral sobre o forro
T-005	sem forro (estrutura aparente)	36,00	ambiente com estrutura aparente e la mineral
T-006	sem forro (estrutura aparente)	36,00	la sobre o forro branco e la mineral sobre o forro
T-007	sem forro (estrutura aparente)	36,00	la sobre o forro branco e la mineral sobre o forro

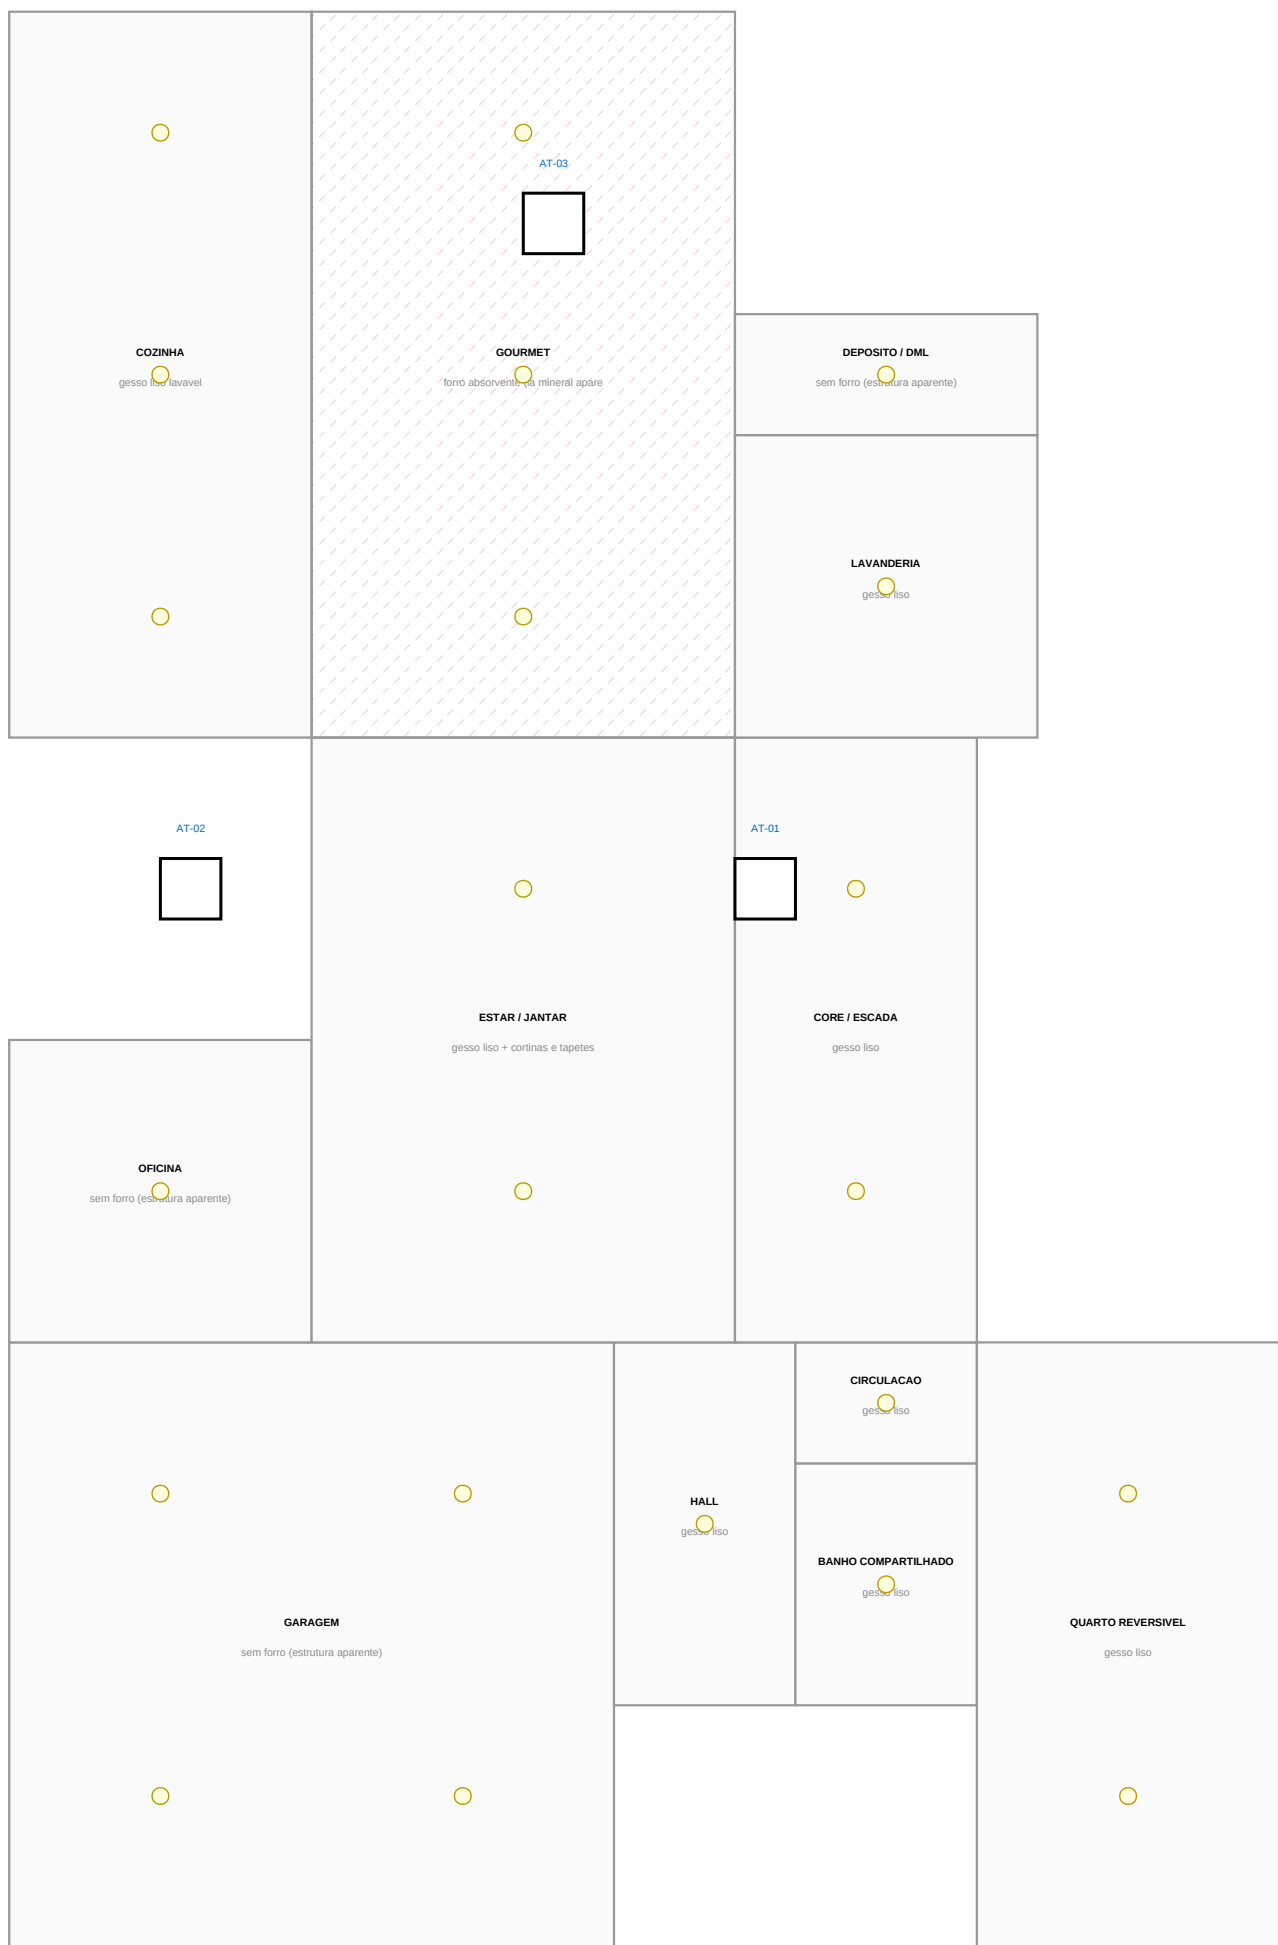

1 FORRO REFLETIDO — TERREO
ESCALA 1:75

NOTAS

1. Planta refletida: vista do forro projetada no plano horizontal.

2. Forro absorvente apenas no gourmet — único ponto com necessidade crítica.

3. Alcapças técnicas de 600 x 600 mm, passando de cobertura de 600 mm.

4. Luminárias para 3.000 K, RSC mínimo 90.

PROJETO PORTO REAL

RESIDÊNCIA UNIFAMILIAR (MANSÃO - AM) | SOBR TATIANA-PS

PROJETO ARQUITETÔNICO

PLANTA DE FORRO E ILUMINAÇÃO

BASE GEOMÉTRICA	ESCALA	EMISSÃO	PROVA
União Consolidada	1:75	ESTUDO PRELIMINAR R37	16
PM-102 (previsão)	FORMATO A1	IMÓVEL LIBERADO PARA OBRAS	
UNIDADE: METRO: MM	MILIMETRO: MM	SEM ART / RNT	06-25 REV R37