




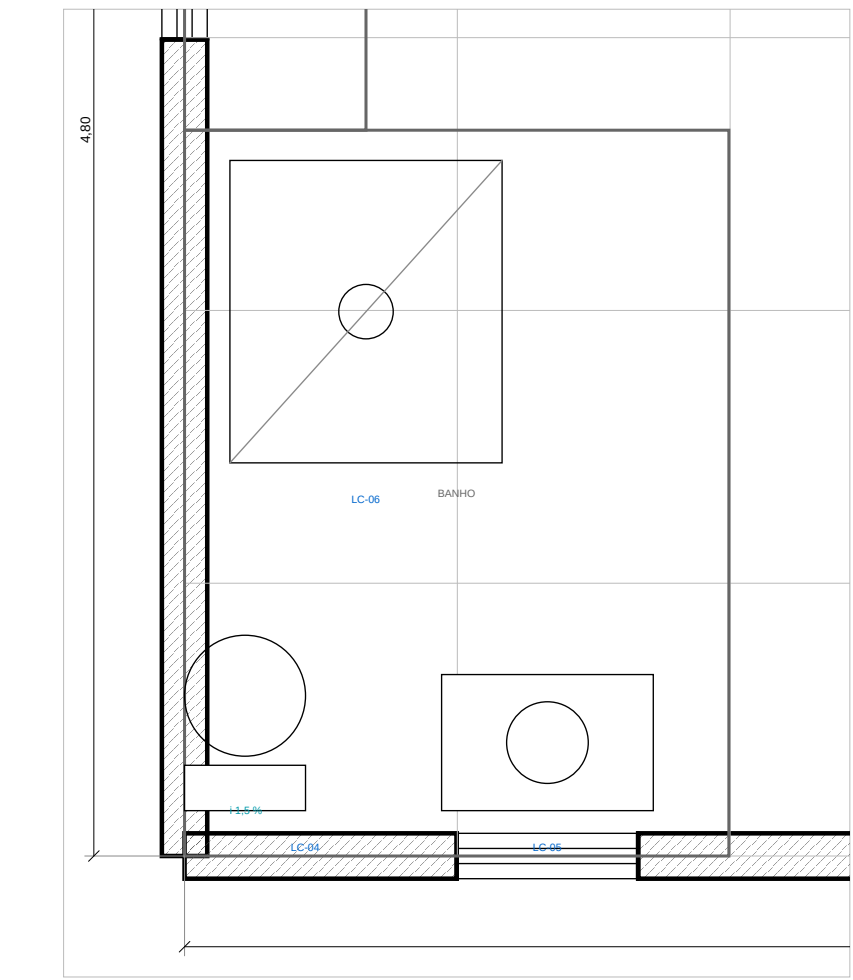


1 SUITE 02 — BANHO
ESCALA 1:25

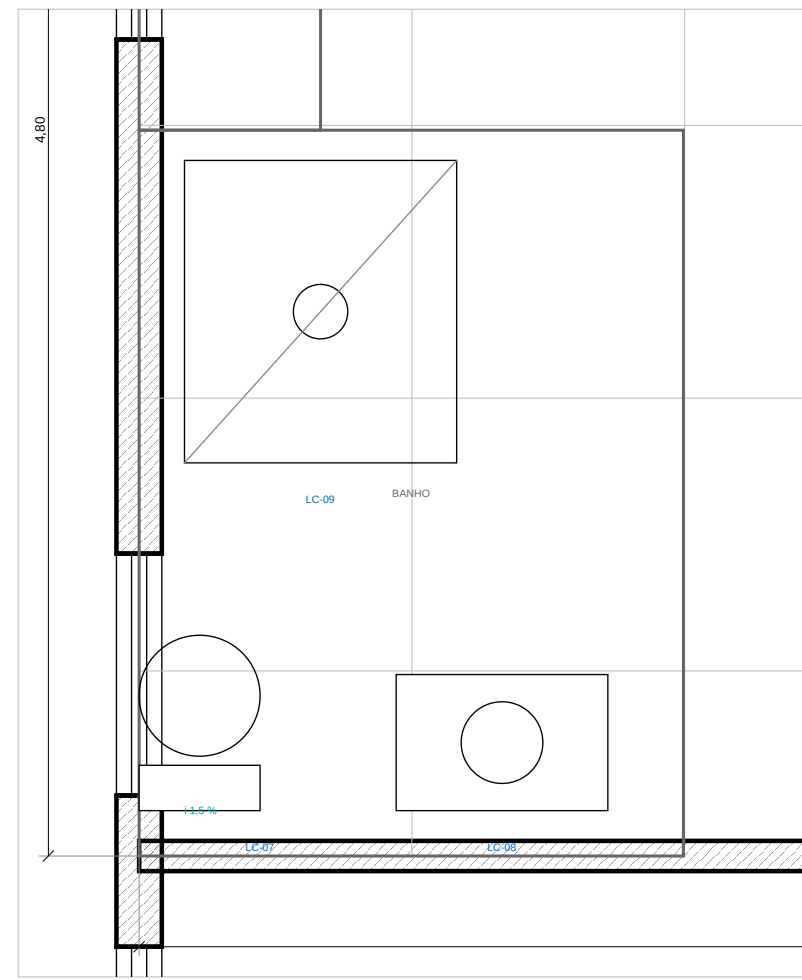

2 SUITE 03 — BANHO
ESCALA 1:25

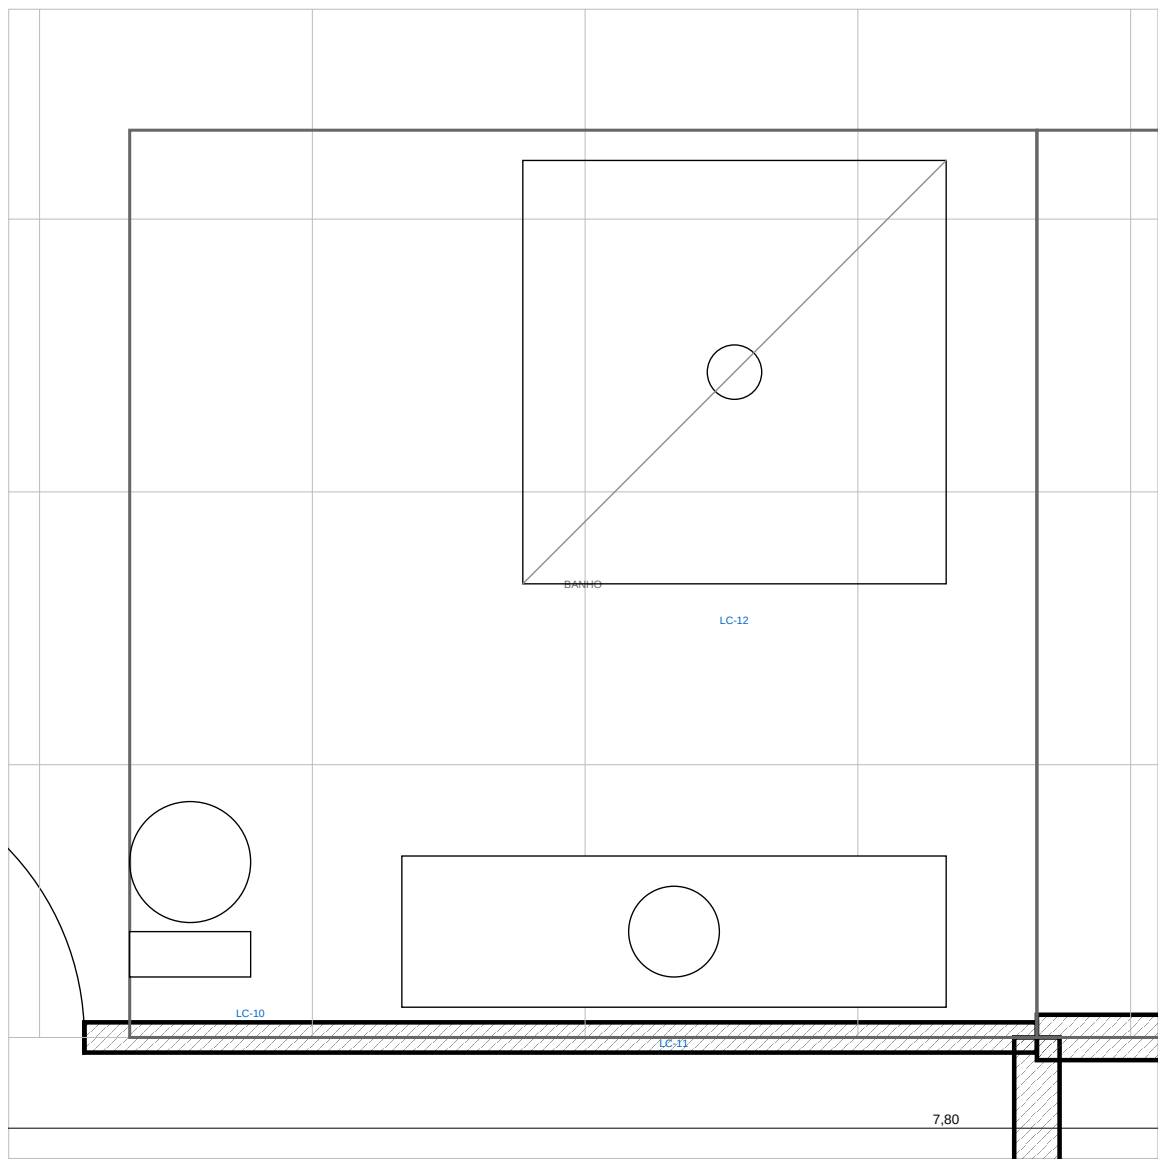

3 MASTER — BANHO
ESCALA 1:25

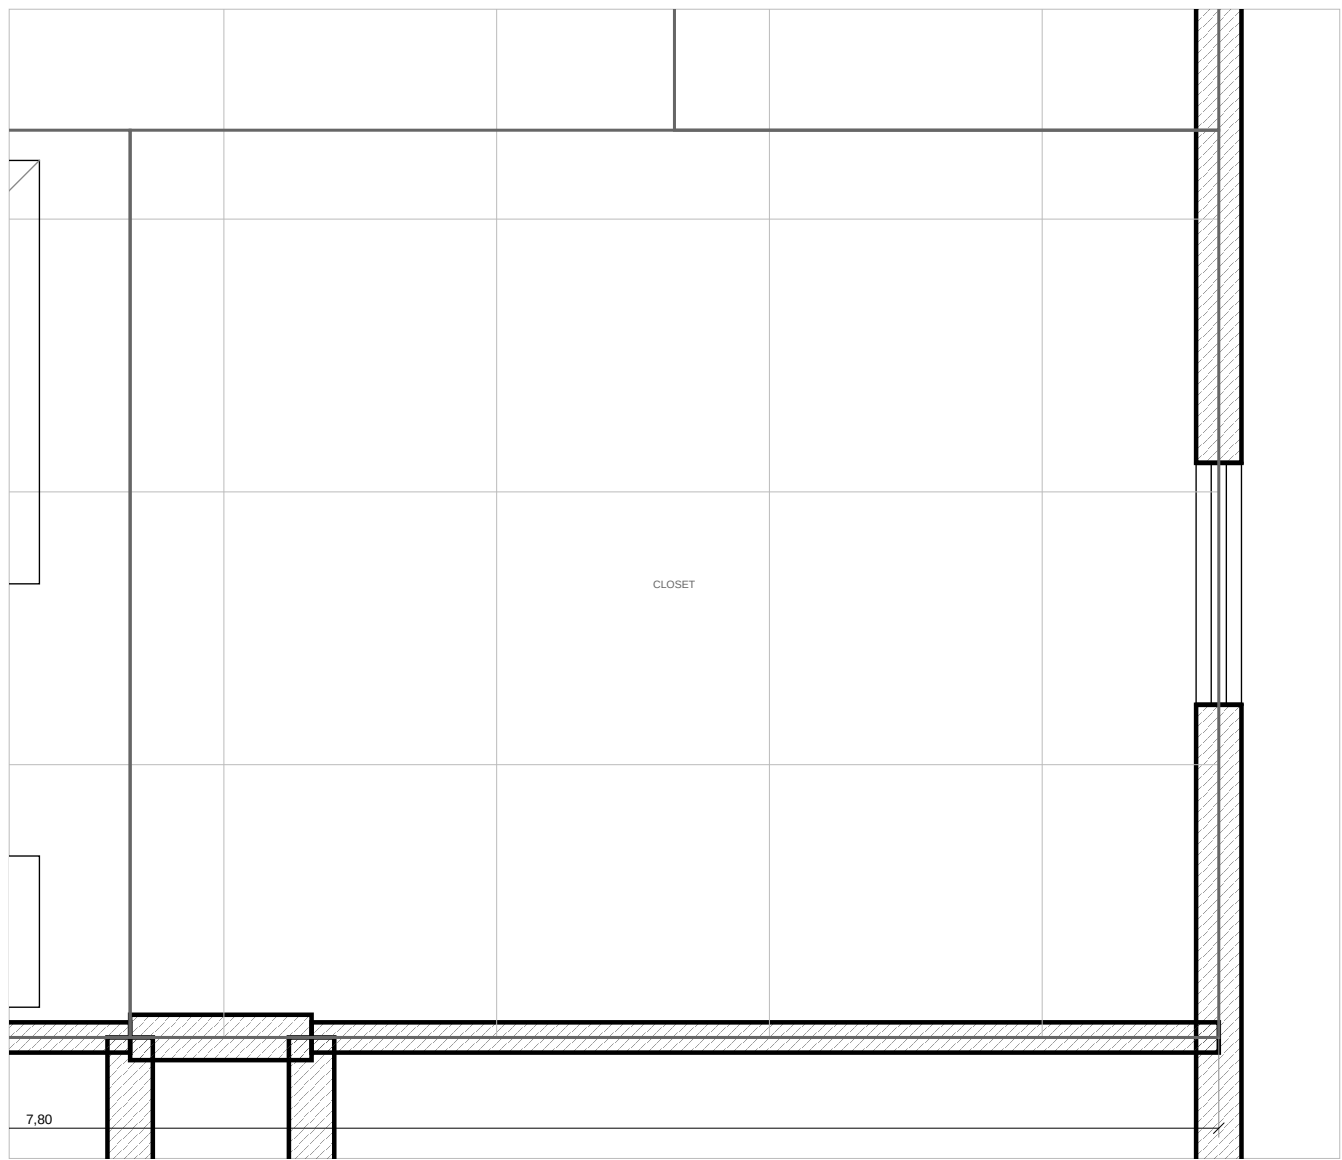

4 MASTER — CLOSET
ESCALA 1:25

PAGINACAO VERIFICADA — PECAS INTEIRAS + RECORTE EM CADA PONTA

AMB	AMBIENTE	ZONA	PEÇA	EXO X	EXO Y	ALTURA (mm)
S-002	SUITE 02 — BANHO	ZP-3	GRU	S-002B	S-002B	---
S-003	SUITE 03 — BANHO	ZP-3	GRU	S-003B	A-003D07B	---
S-005	MASTER — BANHO	ZP-2	GRU	S-005D	S-005B	---
S-006	MASTER — CLOSET	ZP-2	GRU	S-006D	S-006B	---

- NOTAS
- * Pigneticas de piso em linha fina, a malha vem da ZONA de pigneticas, não do canto do ambiente.
 - * Peca de piso porcelanado retificado 300 x 300, parede ceramico retificado 300 x 600, porta 2 mm.
 - * Cimento de 1:3 para o piso em toda area molhada, soltura elevada 15 mm nos bicos.
 - * Representacao: porta ligada em 2 dimensoes, altura 200 mm na parede e 1.800 mm nos bicos.

PROJETO PORTO REAL

RESIDENCIA UNIFAMILIAR (MANAUS - AM) | SUITE TATIANA-PS

PROJETO ARQUITETONICO

AMPLIACOES DE AREA MOLHADA — SUPERIOR

BASE GEOMETRICA Linha Consolidada Projeto (previsão) UNIDADE: METROS - MM	ESCALA 1:25 FORMATO: A1 MILHA: 600/500/300	EMISSAO ESTUDO PRELIMINAR R37 LADO LIBERADO PARA DRENA SEM ART / INT	PROJETO 23 06-25 REV R37
--	---	---	--------------------------------