


FORROS POR AMBIENTE			
ANEXO	SOLUÇÃO	ÁREA	POR QUE
T-IGOV	forro absorvente (a mineral aparente ou por	20,14	evita ponto que demanda a manutenção de 2,20 m ² por
T-60C	gesso bet - corantes e lapides	25,20	absorvem umidade do ambiente, forro tornou mais leve
T-00C	gesso bet forro limal	18,00	superfície de fácil limpeza sem necessidade de pintar
S-00C	gesso bet - la mineral sobre o forro	25,60	la sobre o forro atenua ruído de chuveiro no banheiro P01
S-00S	gesso bet - la mineral sobre o forro	25,92	não
S-00S	gesso bet - la mineral sobre o forro	28,80	não
T-04H	sem forro (pedestais aparentes)	36,00	antifonho sem exigência acústica nem técnica
T-01H	sem forro (pedestais aparentes)	9,00	não
T-02P	sem forro (pedestais aparentes)	3,60	não

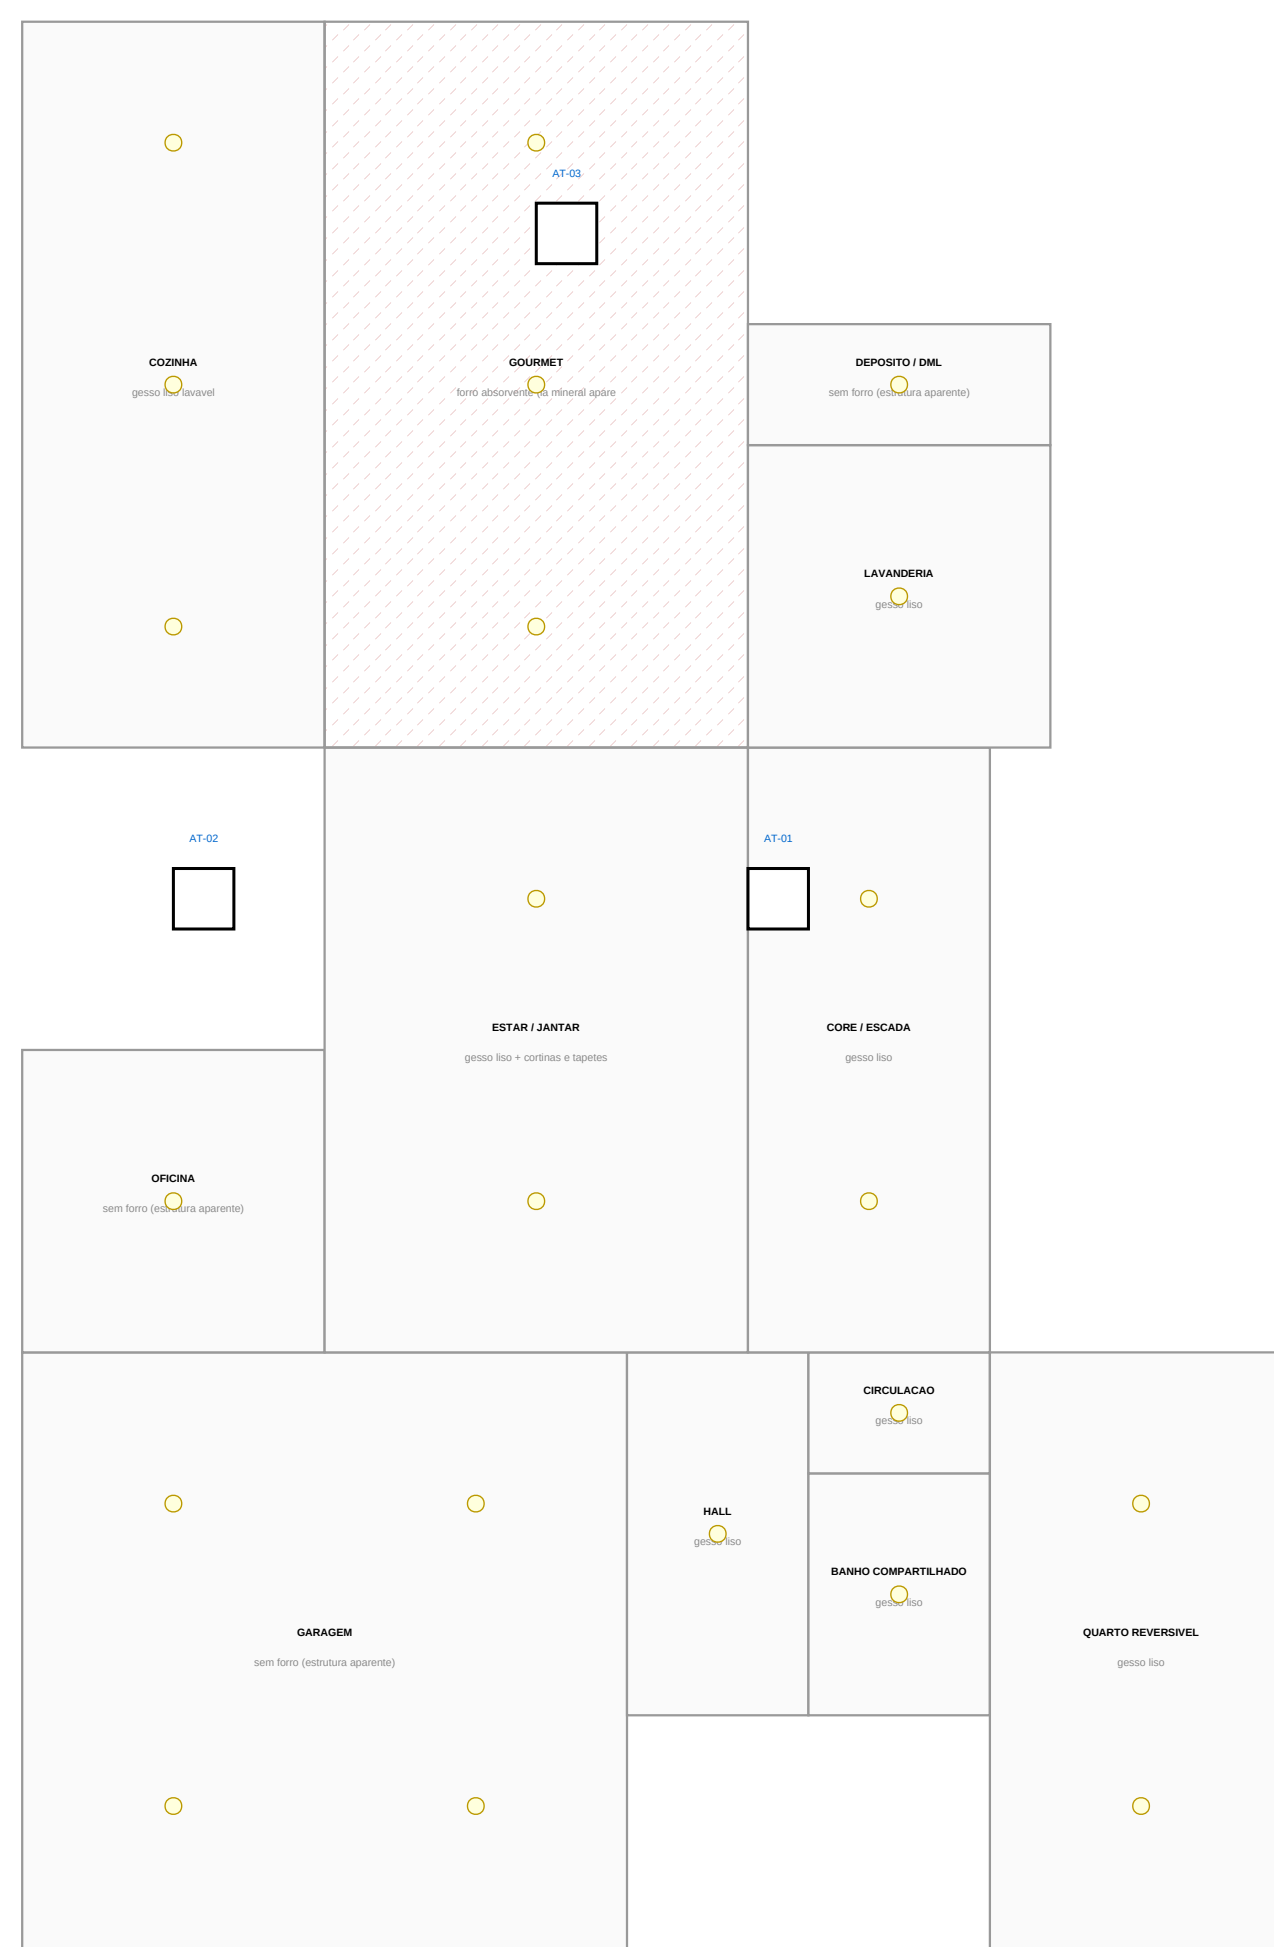

1 FORRO REFLETIDO — TERREO
ESCALA 1:75

NOTAS

- Planta refletida: vista do fôrno projetada no plano horizontal.
- Forno absorvente apenas no gourmet. — único ponto com reverbescção crítica.
- Alçapões técnicos de 600 x 600 mm; passarela de coberturas de 600 mm.
- Iluminação geral 3.000 K, IRC mínimo 90.

PROJETO PORTO REAL			
RESIDENCIA UNIFAMILIAR MANAUS - AM 5010 TAPAMA PH			
PROJETO ARQUITETONICO			
PLANTA DE FORRO E ILUMINACAO			
BASE GEOMETRICA Lista Consolidada pro-012 (privileios) PROJETO MESTRE: 000	ESCALA 1:75 FORMATO A1 MANAUS 06/09/2020	EMISSAO ESTUDO PRELIMINAR R29 NAO LIBERACAO PARA OBRA SEM ART 000	PROJECOR 16 de 35 REV 023