
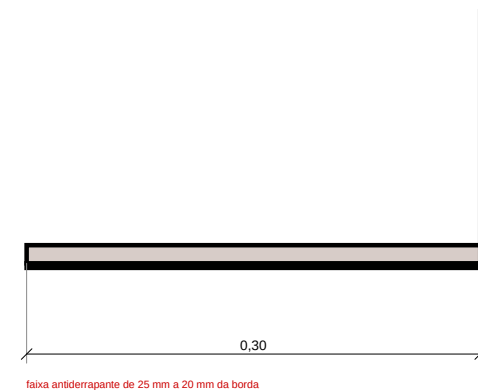
 
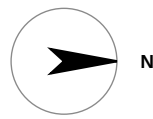


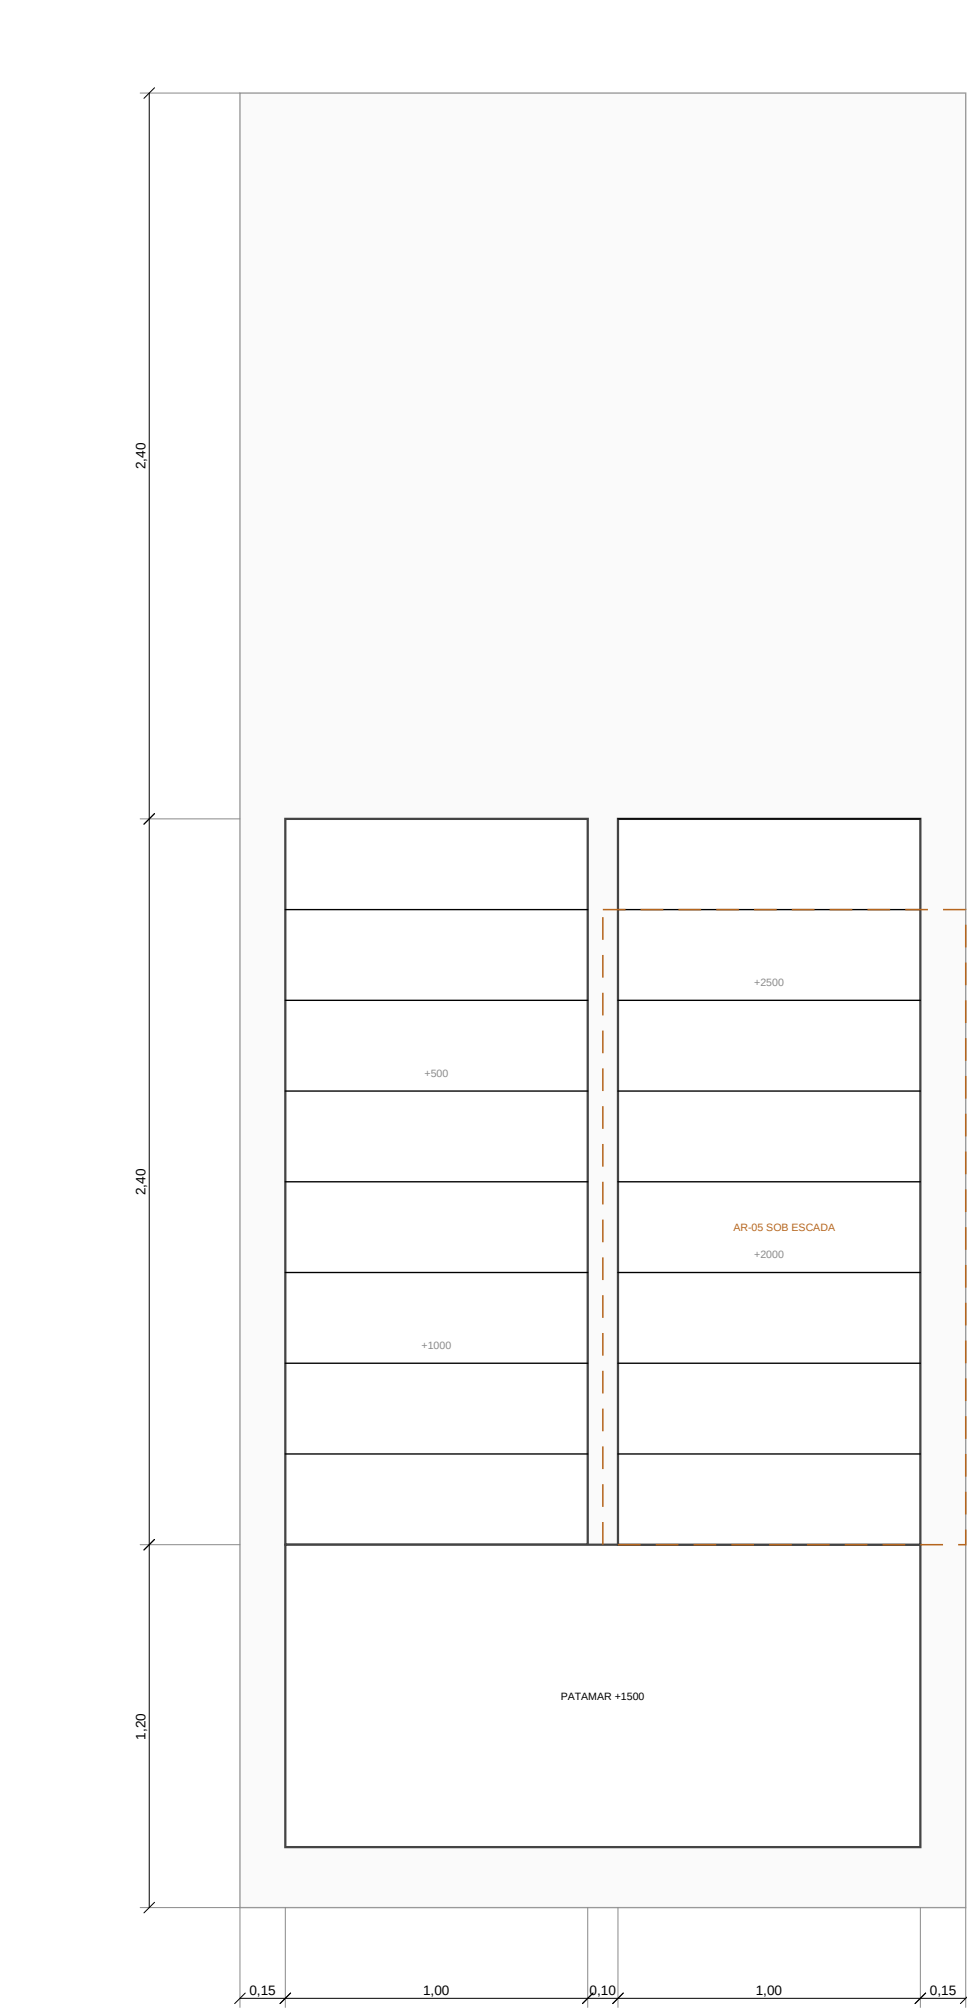

espelho fechado (NBR 9050)

chapa 80x80x3 mm - preenchido 90x x 300

1 PLANTA DA ESCADA

ESCALA 1:25

VERIFICACAO DA ESCADA

ITEM	PROPOSTO	NORMA	
Espelho	186,67 mm	18 a 18 cm (NBR 9077)	OK
Piso	300 mm	min 28 cm	OK
Bondex (2h + g)	633,3 mm	600 a 650 mm	OK
Largura útil de lance	1000 mm	min 1.200 mm (para coberturas) e 1.300 mm (para rampas)	OK
Platamar	1000 mm	min largura de lance	OK
Altura livre mínima	0 mm	min 2100 mm	EXCETO
Guarda-corpo	1100 mm	min 1.200 mm (NBR 14738)	OK
Corrimão	920 x 700 mm	Acabado 92 cm x 70 cm (NBR 9050)	OK
Espelho fechado	sem	conformidade com norma aplicável	OK
Desnível vencido	3000 mm	18 x 186,67 mm	OK

O QUE A PLANTA NAO MOSTRA

QUESTAO	RESPOSTA
Por que o primeiro espelho sobre o y é 18,67?	o patamar tem 186,67 mm de largura do lado esquerdo, com 1.000 mm de altura livre — então quanto a altura da cobertura do quem termina o primeiro lance
Por que a verificação de altura livre é bidimensional?	altura livre da escada e o único critério que não aparece em planta horizontal, dependendo da cor da degrau e da cor do que há acima dele
O que há sob o segundo lance?	intergelo com altura variável, desenhado como amarrado (NBR 9050) mas a circulação tem espaço livre
Por que espelho fechado?	degrau variado prende a porta do pé de quem está chegando ou tem mobilidade reduzida (NBR 9050)
Por que corrimão duplo?	920 mm para adulto e 700 mm para criança, em caso com escada aberta para a sala, o segundo corrimão é o que realmente se usa

NOTAS

- 18 espelho de 186,67 mm e piso de 300 mm. Bondex 2h + g = 633,3 mm (linha recomendada 600 a 650).
- Altura livre mínima 2100 mm (NBR 9077), verificada degrau a degrau contra a tape e o vazio acima.
- Guarda-corpo 1100 mm, corrimão duplo em 920 x 700 mm (NBR 9050).
- dois patas 1.200 mm com degrau em chapa de 3 mm.

PROJETO PORTO REAL

RESIDENCIA UNIFAMILIAR (MARAUAS - AM) | SUELE TATIANA PI

PROJETO ARQUITETONICO

ESCADA — DESENHO EXECUTIVO

BASE GEOMETRICA	ESCALA	EMISSAO	PROJECION
União Consolidada	indicada	ESTUDIO PRELIMINAR R20	
ISO A1 (vertical)	FORMATO A1	NAO LIBERADO PARA OBRA	
UNIDADE: METROS - MM	MILIMETROS (1:25)	SEM ART / RNT	25