


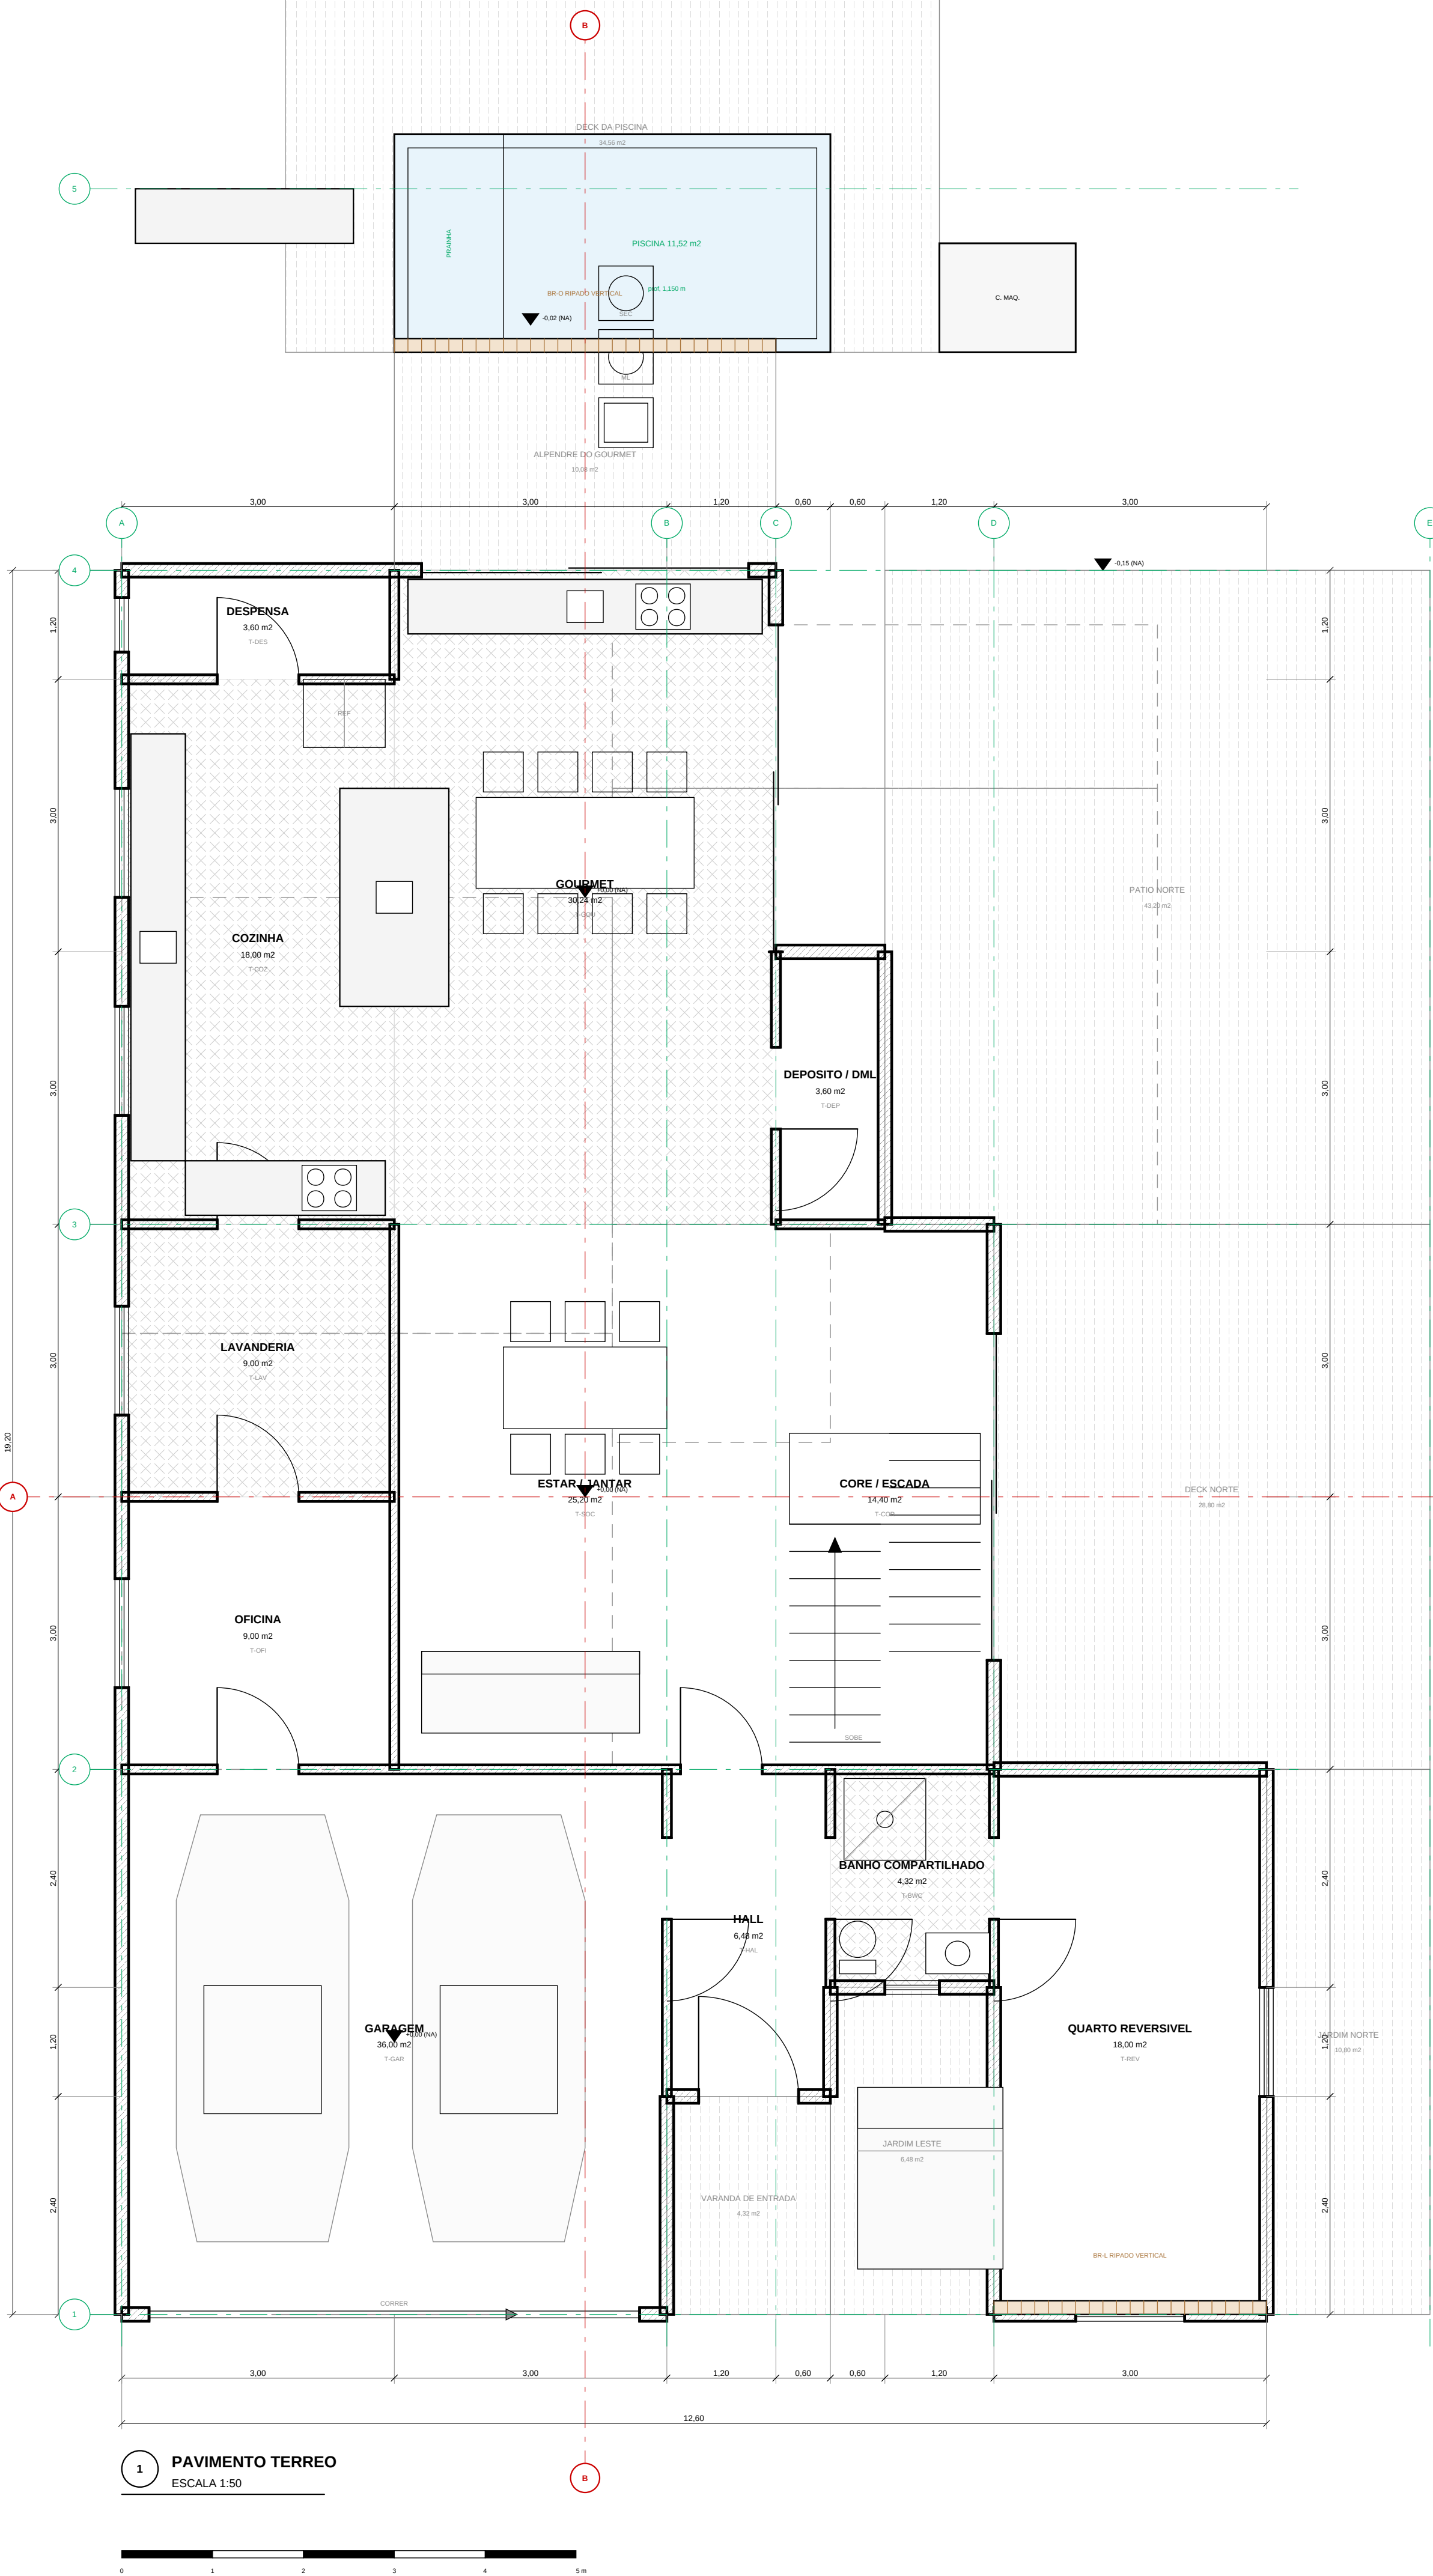

QUADRO DE ÁREAS — PAVIMENTO TERREO			
COD	AMBIENTE	MÓDULO (mm)	ÁREA (m²)
T-GAR	CARACEM	600x600	36,00
T-HAL	HALL	1800x3000	5,40
T-BNC	BANHO COMPARTILHADO	1800x400	4,32
T-REV	QUARTO REVERSIVEL	3600x600	21,60
T-OFI	OFICINA	3000x3000	9,00
T-LAV	LAVANDERIA	3000x3000	9,00
T-COZ	COZINHA	3600x6000	18,00
T-DES	DESPENSA	3000x1500	3,60
T-SOC	ESTAR / JANTAR	4500x6000	27,00
T-COR	CORE / ESCADA	2400x6000	14,40
T-GOU	GOURMET	4200x7200	30,24
T-DEP	DEPOSITO / DML	1200x3000	3,60
TOTAL FECHADO			177,84
T-VAR	VARRANDA DE ENTRADA (aberta)	1800x2400	4,32
T-J.E	JARDIM LESTE (aberto)	1800x3000	5,40
T-J.N	JARDIM NORTE (aberto)	1800x6000	10,80
T-DEK	DECK NORTE (aberto)	4800x6000	28,80
T-PAT	PATIO NORTE (aberto)	6000x7200	43,20
T-ALP	ALFENDEIRO DO GOURMET (aberto)	4200x2400	10,08
T-DEP	DECK DA PISCINA (aberto)	7200x600	4,32

MAPA DE ESQUADRIAS DO PAVIMENTO				
REF	WAD (mm)	REF.	QTD	TIPO
J01	1200x1200	1200	6	paredes de divisórias, externas
J02	600x600	1200	2	paredes de divisórias, sala transição
P01	1100x2800	0	1	porta principal, sala ampla
P02	900x1200	0	6	porta interna (divisórias unificadas)
P04	900x1200	0	4	porta de serviço, residência e unidade
P05	6600x8400	0	1	portão de corte, alumínio esquadado
P06	3600x1400	0	3	vão social posterior

LEGENDA E CONVENCOES (NBR 6492 / 8403)

- Elemento seccionado pelo plano de corte (h = 1,50 m)
- Área coberta / telhado de esquadro
- Mobiliário fixo, equipamentos e simbologia
- Projeto de pavimento superior e da cobertura
- Elemento modular e linha de corte
- Linha de corte e linha auxiliar

- NOTAS
- Dimensões em milímetros; cotas de nível em metros.
 - Malha modular 600 mm; cotas mín. a 600.
 - Paredes externas 150 mm / divisórias internas 100 mm (p).
 - Mobiliário fixo indica pontos de água e energia (NBR 6492).

PROJETO PORTO REAL

RESIDENCIA UNIFAMILIAR (MANAUS - AM) | SOUZA TATIANA-PS

PROJETO ARQUITETONICO

PLANTA DE LAYOUT — PAVIMENTO TERREO

BASE GEOMETRICA Linha Consolidada VIA P122 (previsível) UNIDADE: METRO (m)	ESCALA 1:50 FORMATO: A1 MALHA: 600/600 (mm)	ENTRADA ESTUDO PRELIMINAR VIA LIBERADO PARA OBRA SEM ART / RNT	PROJETA 04 06.13
---	--	---	------------------------