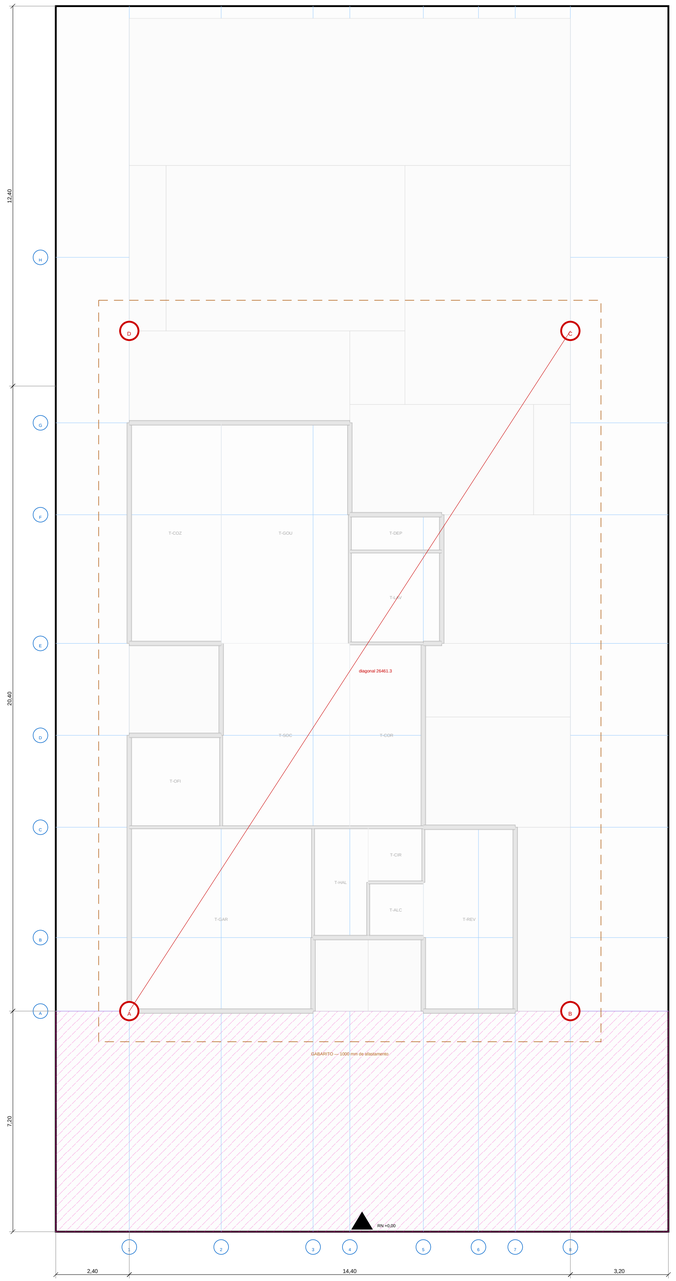


1 **LOCACAO — EIXOS E COORDENADAS**
ESCALA 1:100

N

COORDENADAS DOS CANTOS (mm)

CANTO	X	Y	DIVISA SUL	DIVISA NORTE	TESTADA	FUNDO	DIAGONAL
A	2400	7200	2400	17600	7200	32800	26461,3
B	16800	7200	16800	3200	7200	32800	26461,3
C	16800	29400	16800	3200	29400	10800	26461,3
D	2400	29400	2400	17600	29400	10800	26461,3

PROCEDIMENTO DE LOCACAO

#	PASSO	CRITERIO DE ACEITE
1	Conferir as divisas com a matrícula e o memorial do lote	divergencia acima de 50 mm interrompe a locacao
2	Implantar o RN: marco de concreto 200 x 200 x 500 mm, fora da area de obra	fora da area de obra
3	Montar o gabarito a 1000 mm do contorno	pontaletes 75 x 75 e tabua 25 x 150
4	Marcar os eixos X (1 a 8) e Y (A a H) no gabarito	toda coordenada multipla de 300 mm
5	Cotar cada canto das DUAS divisas	nunca em cadeia: erro de cadeia soma
6	Conferir a diagonal A-C	26461.3 mm com tolerancia de 10 mm
7	Conferir esquadro por 3-4-5 em cada canto	antes de qualquer concretagem
8	Registrar em ata com foto e medida	gabarito continuo nos dois lados da obra, conferenci

EIXOS MODULARES

DIRECAO	EIXOS (mm)
X (1 a 8)	2400 · 5400 · 8400 · 9600 · 12000 · 13800 · 15000 · 16800
Y (A a H)	7200 · 9600 · 13200 · 16200 · 19200 · 23400 · 29400 · 31800
Malha	principal 600 mm · subgrid 300 mm
Origem	canto frontal esquerdo do lote
Unidade	milimetro

NOTAS

- Locacao e o unico desenho em que o eixo nao tem consento barato: a casa sai do lugar.
- Cada canto e cotado das DUAS divisas, nunca em cadeia acumulada — erro de cadeia soma, erro de referencia independente nao.
- Conferencia obrigatoria pela diagonal: 26461.3 mm entre A e C antes de concretar o radier.
- RN no eixo da testada, alinhado ao medidor TC-08; cota 0,00 = piso acabado do terreo

PROJETO PORTO REAL

RESIDENCIA UNIFAMILIAR | MANAUS - AM | SUB3 TARUMA (H)

PROJETO ARQUITETONICO

LOCACAO DE OBRA E GABARITO

BASE GEOMETRICA	ESCALA	EMISSAO	PRANCHA
Lista Consolidada pos-R32 (prevalece)	**1:100** FORMATO A1	ESTUDO PRELIMINAR R86 NAO LIBERADO PARA OBRA	**31** de 76 REV R86
UNIDADE MESTRE: mm	MALHA 600/200/100	SEM ART / RRT	