
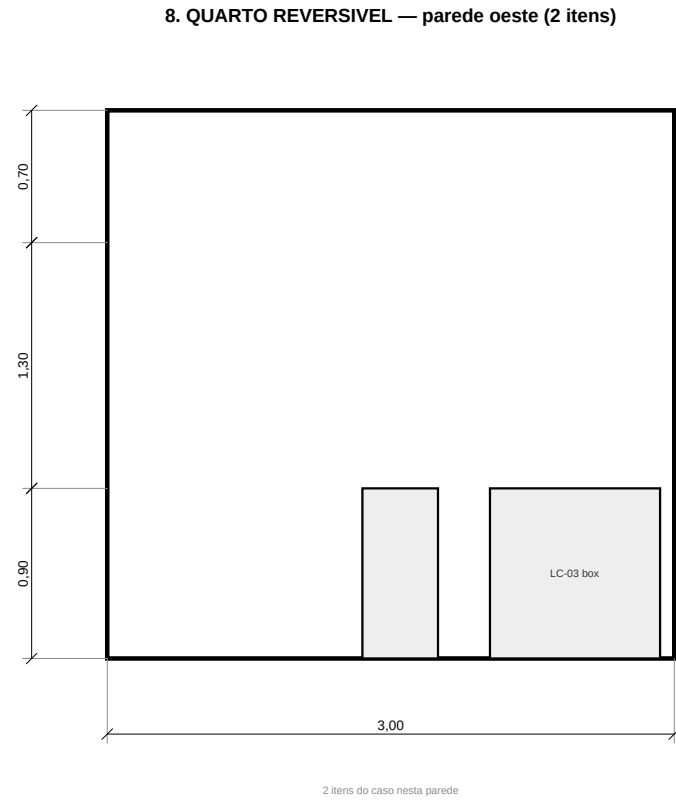
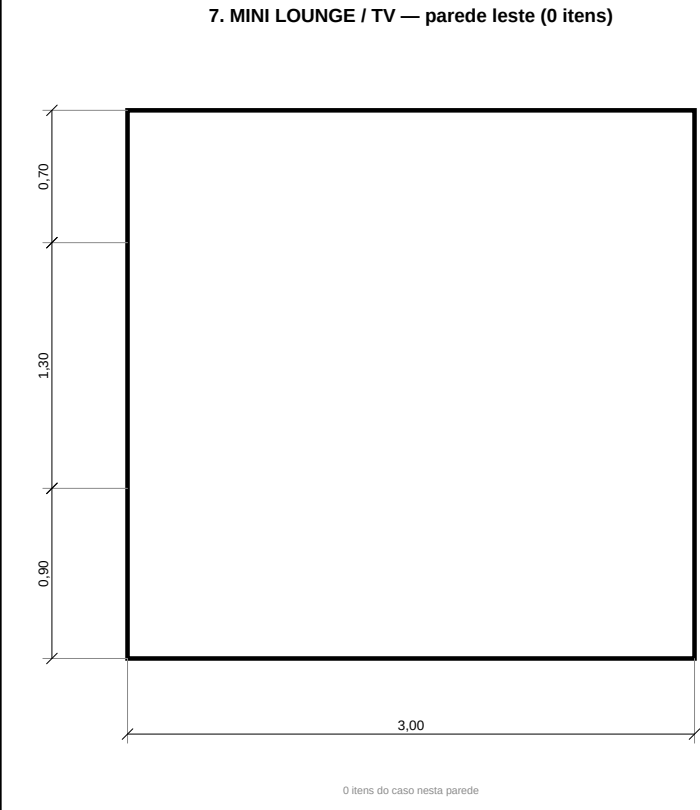
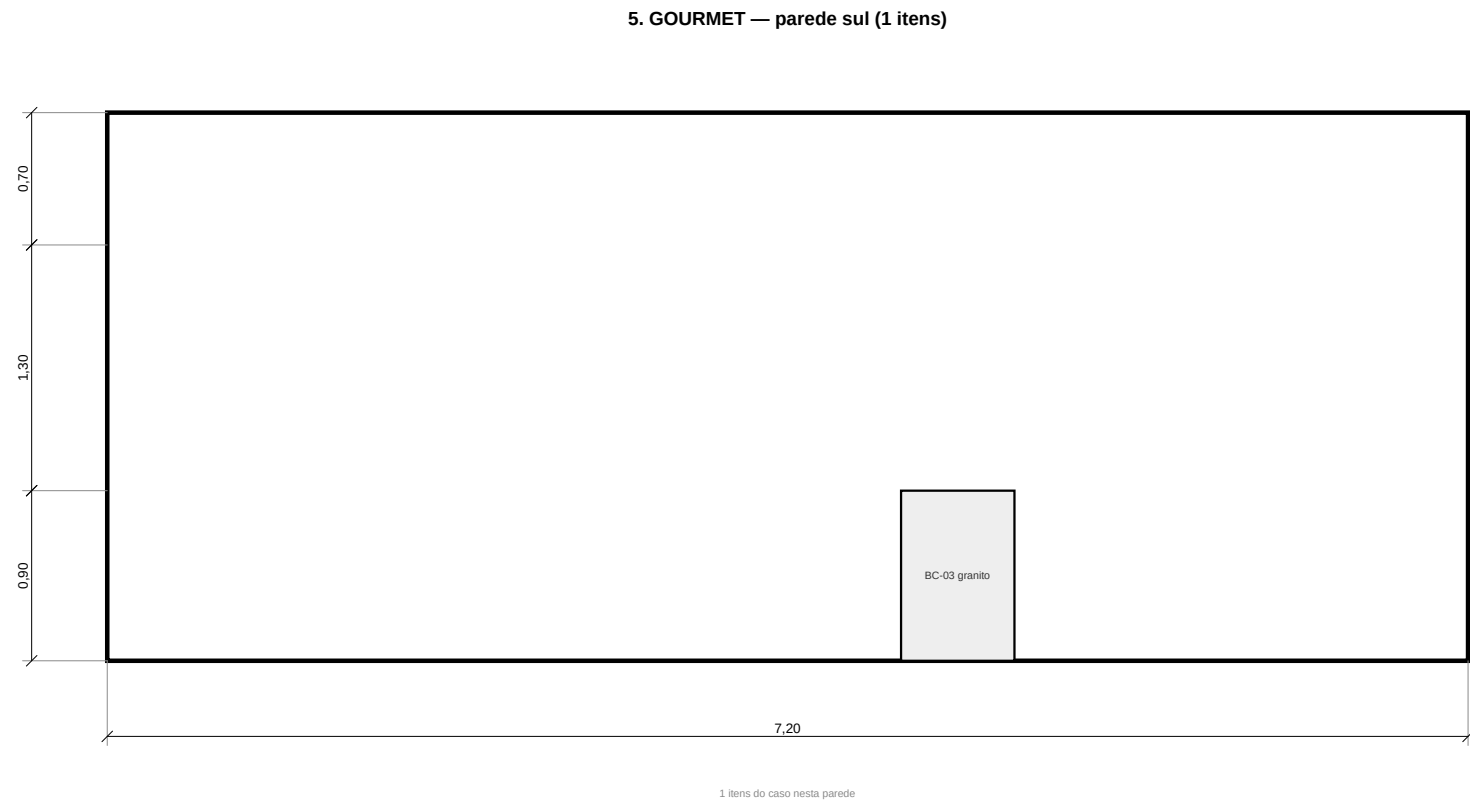
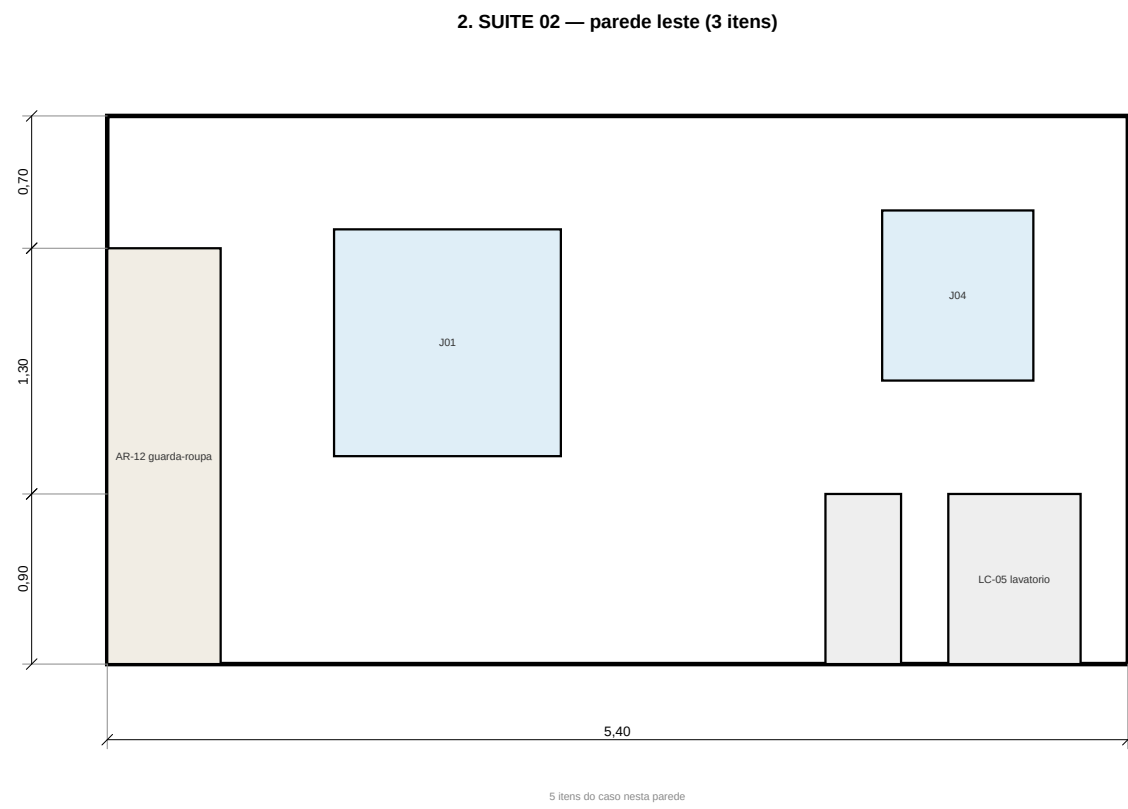


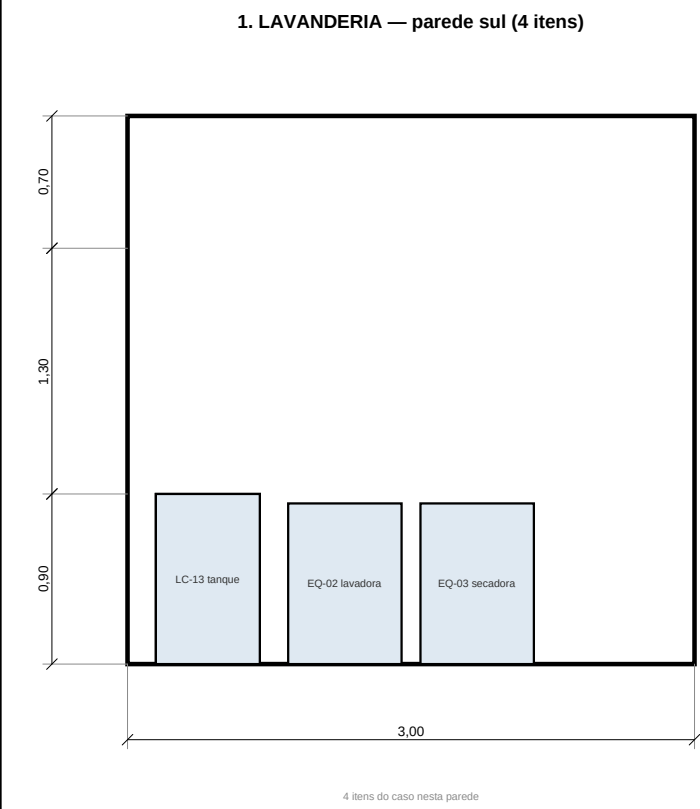

- NOTAS
- Cada item desenvolvido vem de ARMAZENOS, BANCADAS, LOUCAS, EQUIPAMENTOS ou LAYOUT do caso, pelo código, nenhum modular foi digitado nesta planilha.
 - Um item está na parede quando encosta nela a menos de 200 mm. Abaixo por família (F).
 - Janelas e portas da parede vem de VAOCL, com perfil e altura da esquadra.
 - Complementos a PR-10 (piscina, gourmet, barista, banheiro master, oficina, lavanderia).

PROJETO PORTO REAL

RESIDENCIA UNIFAMILIAR (MANAUS - AM) | SUITE TATIANA-PR

PROJETO ARQUITETONICO

ELEVACOES INTERNAS II — DERIVADAS DO MODELO

BASE GEOMETRICA	ESCALA	EMISSAO	PROJECION
União Consolidada	1:40	ESTUDO PRELIMINAR RIB	51
PR-102 (previsão)	FORMATO A1	IMAG. LIBERADO PARA OBRA	SEM ART / INT
UNIDADE METRICA: MM	MILHA 465/500/500	SEM ART / INT	DE-TE REVIEW