

EQUIPAMENTOS

COD	AMB	ITEM
EXT-01	T-GAR	extintor ABC 4 kg, a 1,80 m do piso, sinalizado (garagem)
EXT-02	T-COZ	extintor ABC 4 kg, a 1,80 m do piso, sinalizado (cozinha)
EXT-03	S-HAL	extintor ABC 4 kg, a 1,80 m do piso, sinalizado (hall superi
DF-T-HAL	T-HAL	detector de fumaca autonomo a bateria com interligacao sem f
DF-T-ALC	T-ALC	detector de fumaca autonomo a bateria com interligacao sem f
DF-T-CIR	T-CIR	detector de fumaca autonomo a bateria com interligacao sem f
DF-T-REV	T-REV	detector de fumaca autonomo a bateria com interligacao sem f
DF-T-COR	T-COR	detector de fumaca autonomo a bateria com interligacao sem f
DF-S-SI2	S-SI2	detector de fumaca autonomo a bateria com interligacao sem f
DF-S-SI3	S-SI3	detector de fumaca autonomo a bateria com interligacao sem f
DF-S-CIR	S-CIR	detector de fumaca autonomo a bateria com interligacao sem f
DF-S-CI2	S-CI2	detector de fumaca autonomo a bateria com interligacao sem f
DF-S-HAL	S-HAL	detector de fumaca autonomo a bateria com interligacao sem f
DF-S-MAS	S-MAS	detector de fumaca autonomo a bateria com interligacao sem f
DC-T-COZ	T-COZ	detector de calor (a fumaca da cocciao daria alarme falso)
MT-01	T-COZ	manta antichamas 1,2 x 1,2 m
MT-02	T-GOU	manta antichamas 1,2 x 1,2 m
GAS	T-COZ	detector de GLP a 300 mm do piso, junto ao cooktop, com cort

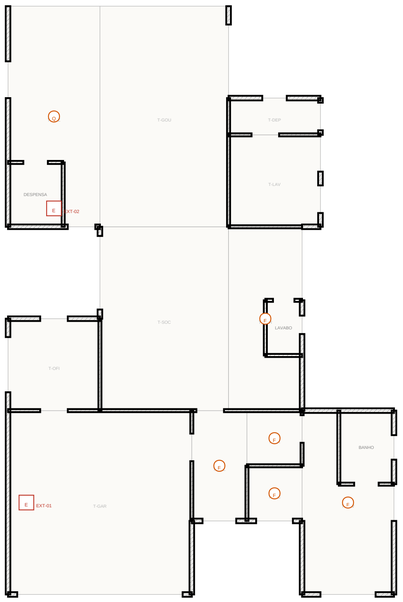

1 **INCENDIO — TERREO**
ESCALA 1:100

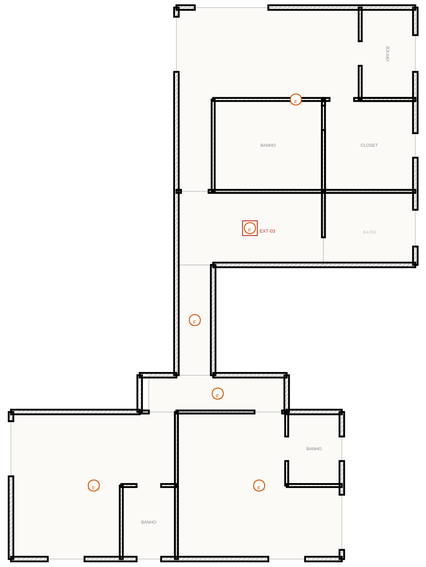

2 **INCENDIO — SUPERIOR**
ESCALA 1:100

NOTAS

- residencia unifamiliar. dispensada de projeto de prevencao (CBM-AM) o que esta aqui e boa pratica, nao exigencia — e por isso e declarado assim
- 3 x extintor ABC 4 kg, a 1,80 m do piso, sinalizado: garagem, cozinha e hall superior — um por pavimento mais a garagem.
- 12 detectores: fumaca em cada dormitorio e circulacao (detector de fumaca autonomo a bateria com interligacao sem fio); calor na cozinha.
- Manta antichamas na cozinha e no gourmet; detector de GLP junto ao cooktop com corte na central (PR-64).
- Simbolos: E extintor · F detector de fumaca · Q detector de calor.

PROJETO PORTO REAL

RESIDENCIA UNIFAMILIAR | MANAUS - AM | SUS8 TARUMA (H)

PROJETO ARQUITETONICO

PREVENCAO CONTRA INCENDIO — EXTINTORES, DETECTORES E GAS

BASE GEOMETRICA	ESCALA	EMISSAO	PRANCHA
Lista Consolidada (pos-R32 (prevalece))	1:100	ESTUDO PRELIMINAR R86	66
UNIDADE MESTRE: mm	FORMATO A1	NAO LIBERADO PARA OBRA	de 76 REV R86
	MALHA 800/300/150	SEM ART / RRT	