



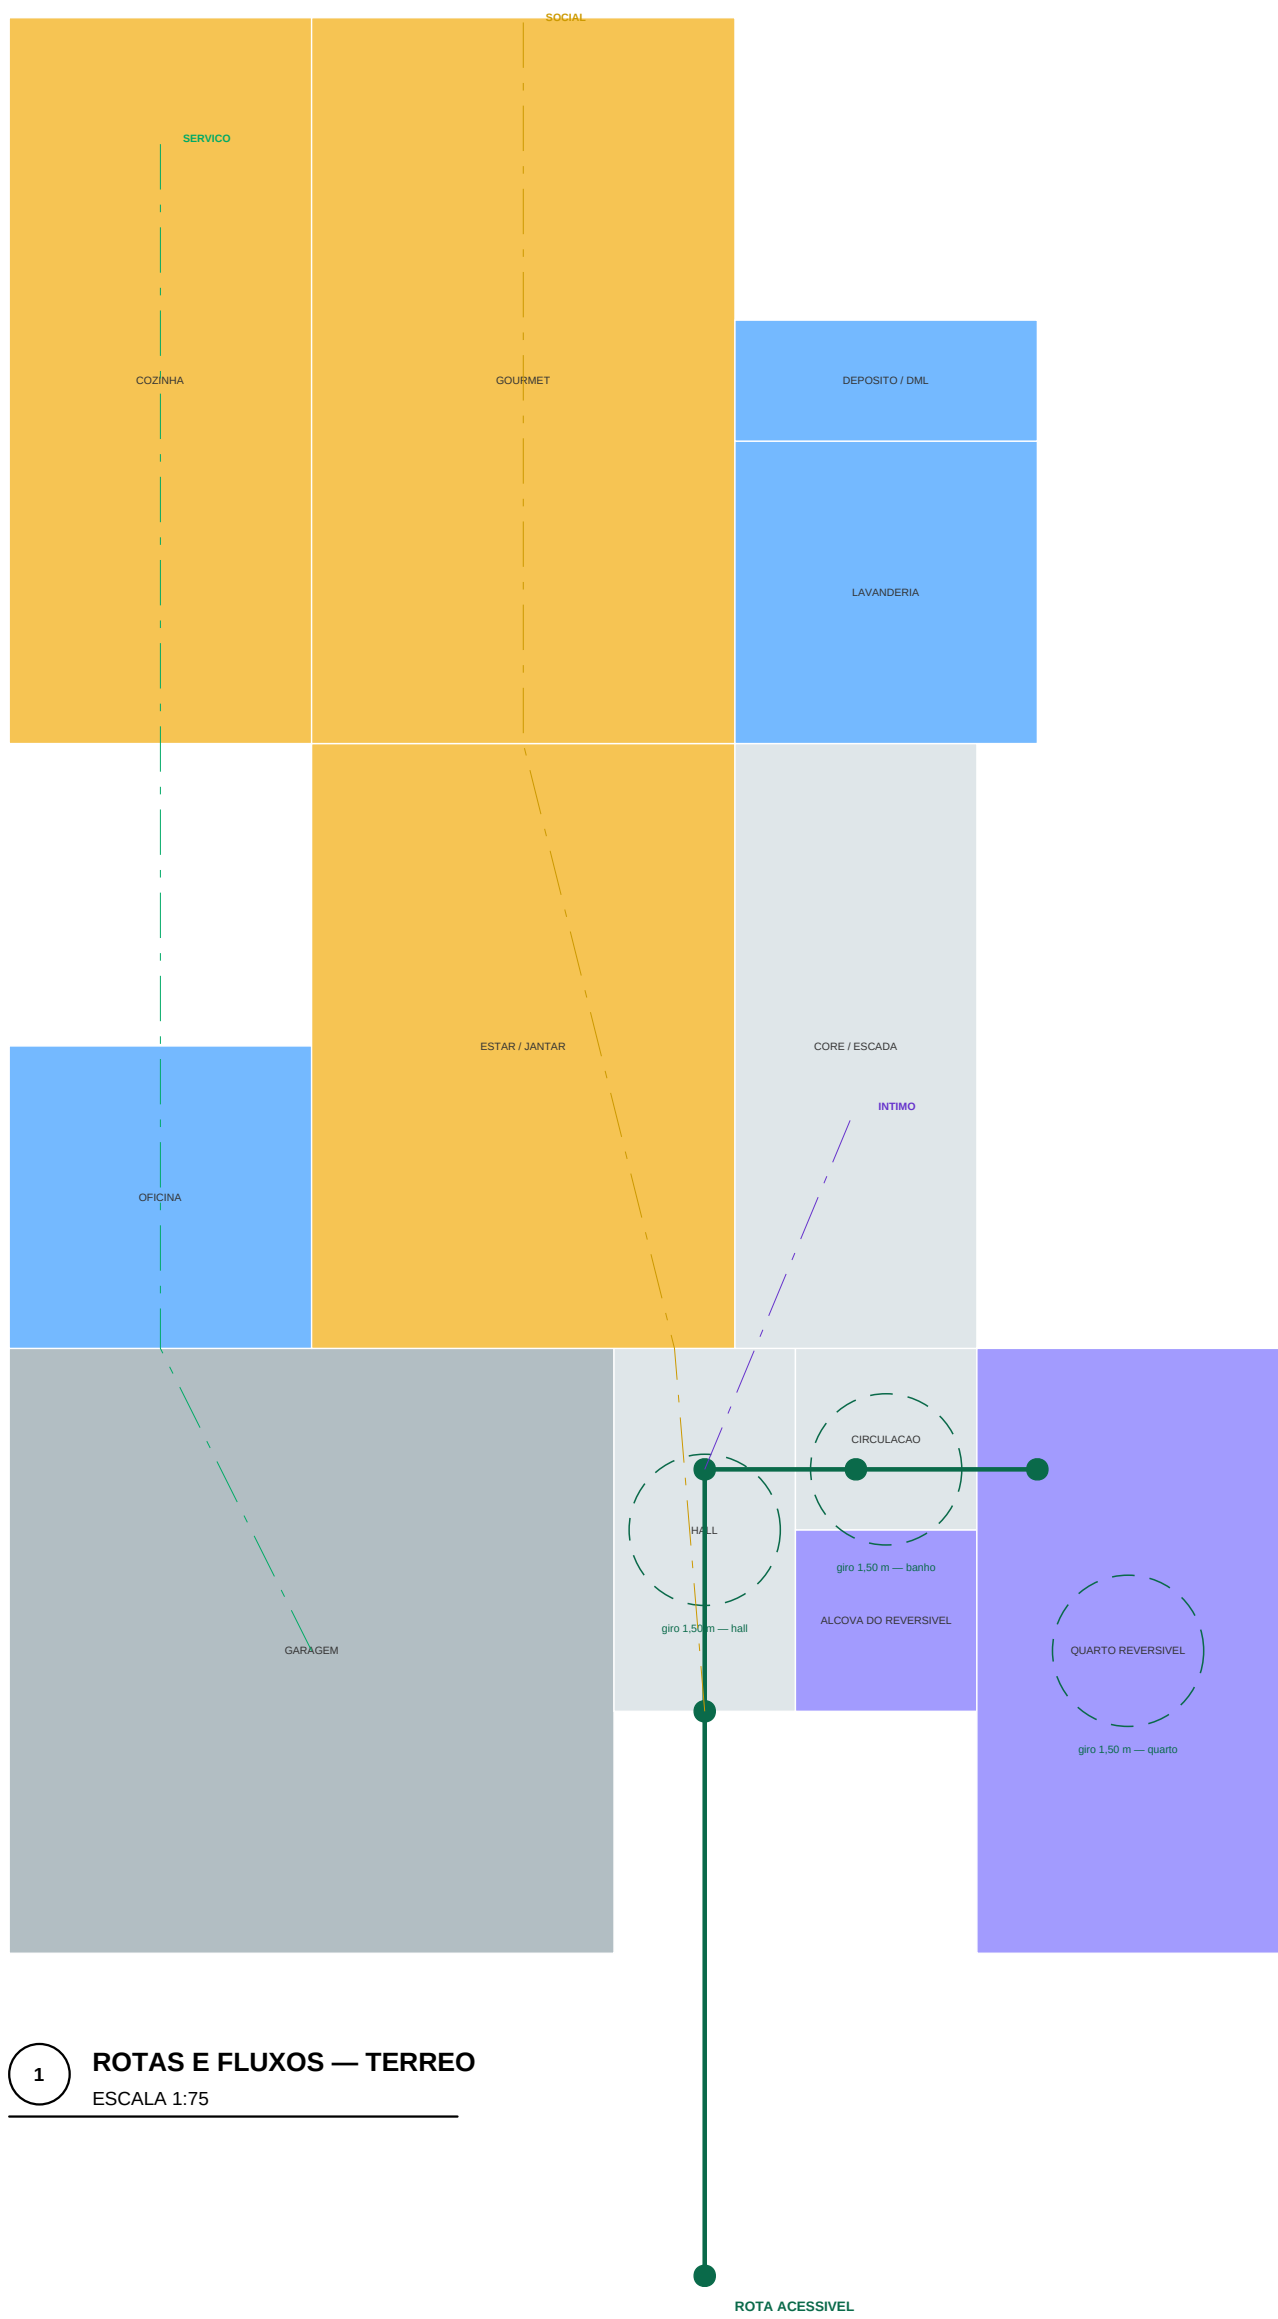

1 ROTAS E FLUXOS — TERREO
ESCALA 1:75

VERIFICACAO NBR 9050

ITEM	EXISTENTE	PROPOSTO	
Viso livre de porta	800 mm	940 mm (altura de 900)	OK
Circulo de giro 360 graus	1.500 mm	hall, banheiro e quarto	OK
Desnivel sem rampa	até 5 mm	soluções niveladas	OK
Largura de circulação	900 mm	1.800 mm no hall	OK
Barras de apoio	relevo no piso	instalação no PISO 1 e PISO 2	OK
Barras de acesso	altura livre 750 mm	sem barreiras até a altura	OK
Corrimão e interruptor	600 a 1.000 mm	a altura do usuário	pendente

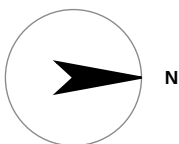

FLUXOS — SEPARACAO DE CIRCUITOS

CIRCUITO	PERCURSO	CRUZAR O SOCIAL?
Serviço	garagem -> estufa -> lavanderia -> cozinha -> despensa	NÃO
Social	entrada -> hall -> estar -> gourmet -> alameda -> piscina	—
Serviço interno	hall -> circulação -> banheiro social (quarto reversível) (se não for projeto)	NÃO
Serviço superior	hall -> core -> hall superior -> suites	NÃO
Uso e carga	cozinha -> despensa -> refeitório	NÃO

- NOTAS
- * Rota acessível do passeio ao quarto reversível e ao banheiro social.
 - * Circulo de giro de 1.500 mm verificado nos pontos de manobra.
 - * Porta de correr de 900 mm no banheiro social e área de varanda.
 - * Refeitório para jantar de apoio instalado antes do fechamento das placas.

PROJETO PORTO REAL

RESIDENCIA UNIFAMILIAR (MANSÃO - AM) | SOBR TATIANA-PS

PROJETO ARQUITETONICO

ACESSIBILIDADE E FLUXOS

BASE GEOMETRICA Linha Consolidada ISO 9122 (previsão) UNIDADE MESTRE: mm	ESCALA 1:75 FORMATO A1 MILHA 955/955/955	EMISSAO ESTUDO PRELIMINAR RBO NÃO LIBERADO PARA OBRA SEM ART / RNT	PROVA 17 DE 45 REVISO
---	---	---	-----------------------------