


QUANTITATIVO DE PAINÉIS E MONTANTES

| FAMÍLIA | PAINÉIS | MONTANTES | MT DE PERÍM | COMPOSIÇÃO                                                 |
|---------|---------|-----------|-------------|------------------------------------------------------------|
| PA-1    | 16      | 71        | 184,6       | dupla chapa 12,5 + montante 48 cr 16 + dupla chapa 12,5    |
| PA-2    | 1       | 6         | 15,6        | dupla chapa 12,5 + perfil isolante + montante 70 cr 16 80  |
| PE-1    | 47      | 263       | 637,8       | linhola 32 + EPS 50 (SD 50) + montante 90 cr 16 90 +       |
| PA-3    | 3       | 17        | 44,2        | gesso 90 12,5 + montante 90 cr 16 90 + gesso 12,5 + reboco |
| PI-1    | 3       | 16        | 41,8        | gesso 12,5 + montante 70 cr 16 90 + gesso 12,5             |
| TOTAL   | 70      | 363       | 943,9       |                                                            |



EXTRATO DA LISTA DE PAINÉIS (26 de 70)

| CODIGO | FAMÍLIA | LARG (mm) | ALT (mm) | MONT. | PRV |
|--------|---------|-----------|----------|-------|-----|
| PT-001 | PE-1    | 3000      | 2000     | 6     | T   |
| PT-002 | PE-1    | 3000      | 2000     | 6     | T   |
| PT-003 | PE-1    | 3000      | 2000     | 6     | T   |
| PT-004 | PE-1    | 3000      | 2000     | 7     | T   |
| PT-005 | PE-1    | 3000      | 2000     | 7     | T   |
| PT-006 | PE-1    | 3000      | 2000     | 6     | T   |
| PT-007 | PE-1    | 3000      | 2000     | 6     | T   |
| PT-008 | PA-1    | 3000      | 2000     | 6     | T   |
| PT-009 | PE-1    | 3000      | 2000     | 6     | T   |
| PT-010 | PE-1    | 3000      | 2000     | 6     | T   |
| PT-011 | PE-1    | 3000      | 2000     | 6     | T   |
| PT-012 | PA-2    | 3000      | 2000     | 6     | T   |
| PT-013 | PE-1    | 3000      | 2000     | 6     | T   |
| PT-014 | PI-1    | 3000      | 2000     | 6     | T   |
| PT-015 | PE-1    | 2100      | 2000     | 4     | T   |
| PT-016 | PE-1    | 2100      | 2000     | 4     | T   |
| PT-017 | PE-1    | 2400      | 2000     | 5     | T   |
| PT-018 | PA-1    | 3000      | 2000     | 7     | T   |
| PT-019 | PE-1    | 1800      | 2000     | 4     | T   |
| PT-020 | PA-1    | 1200      | 2000     | 3     | T   |
| PT-021 | PA-1    | 3000      | 2000     | 6     | T   |
| PT-022 | PA-1    | 1200      | 2000     | 3     | T   |
| PT-023 | PE-1    | 3000      | 2000     | 6     | T   |
| PT-024 | PA-1    | 1800      | 2000     | 4     | T   |
| PT-025 | PA-1    | 600       | 2000     | 2     | T   |
| PT-026 | PA-1    | 2400      | 2000     | 6     | T   |

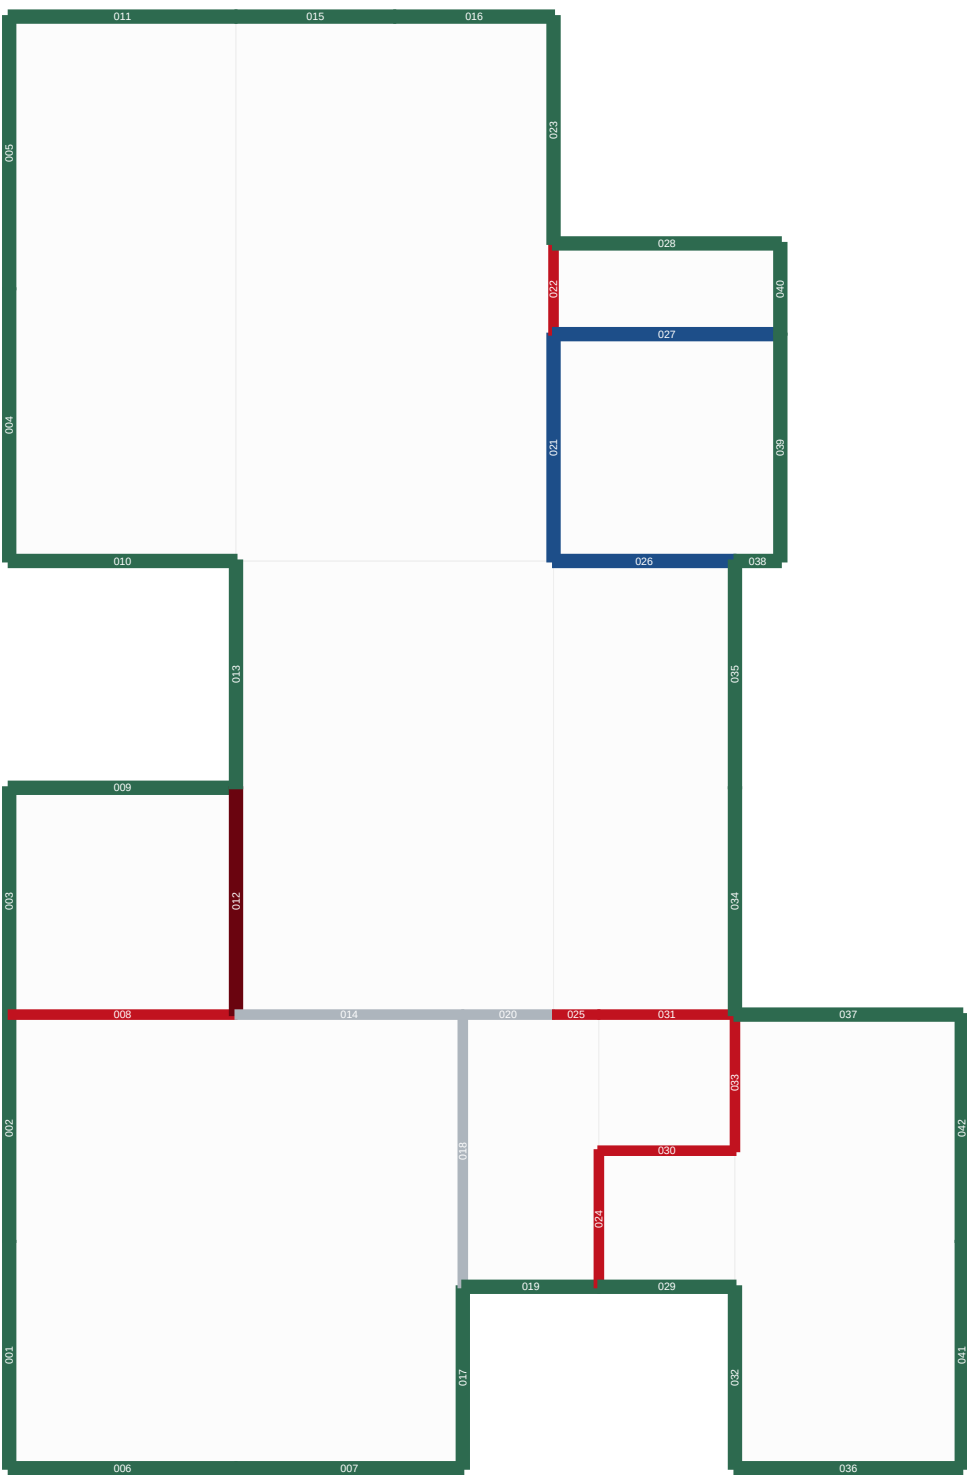

1 PAGINACAO — TERREO  
ESCALA 1:100

- NOTAS
- \* Painéis limitados a 3000 mm por manuseio e transporte.
  - \* Montantes a cada 600 mm, 400 mm onde cabido no revestimento exigir.
  - \* Não furar a peça entre em modelar sem código, largura, altura, espessura, material e revest.
  - \* Numeração por pavimento, a família define a composição interna do painel.

PROJETO PORTO REAL

RESIDENCIA UNIFAMILIAR (MANAUS - AM) | SOUZA TATIANA-PS

PROJETO ARQUITETONICO

PAGINACAO DE PAINÉIS — LIGHT STEEL FRAME

|                                                                                          |                                                             |                                                                                      |                                     |
|------------------------------------------------------------------------------------------|-------------------------------------------------------------|--------------------------------------------------------------------------------------|-------------------------------------|
| BASE GEOMETRICA<br><b>Lista Consolidada</b><br>em PDF (previsão)<br>UNIDADE: METROS - MM | ESCALA<br><b>1:100</b><br>FORMATO: A1<br>MÁQUA: 650/900/300 | EMISSAO<br><b>ESTUDIO PRELIMINAR R00</b><br>TUDO LIBERADO PARA DESA<br>SEM ART / RNT | PROVA<br><b>18</b><br>06-48 REV R00 |
|------------------------------------------------------------------------------------------|-------------------------------------------------------------|--------------------------------------------------------------------------------------|-------------------------------------|