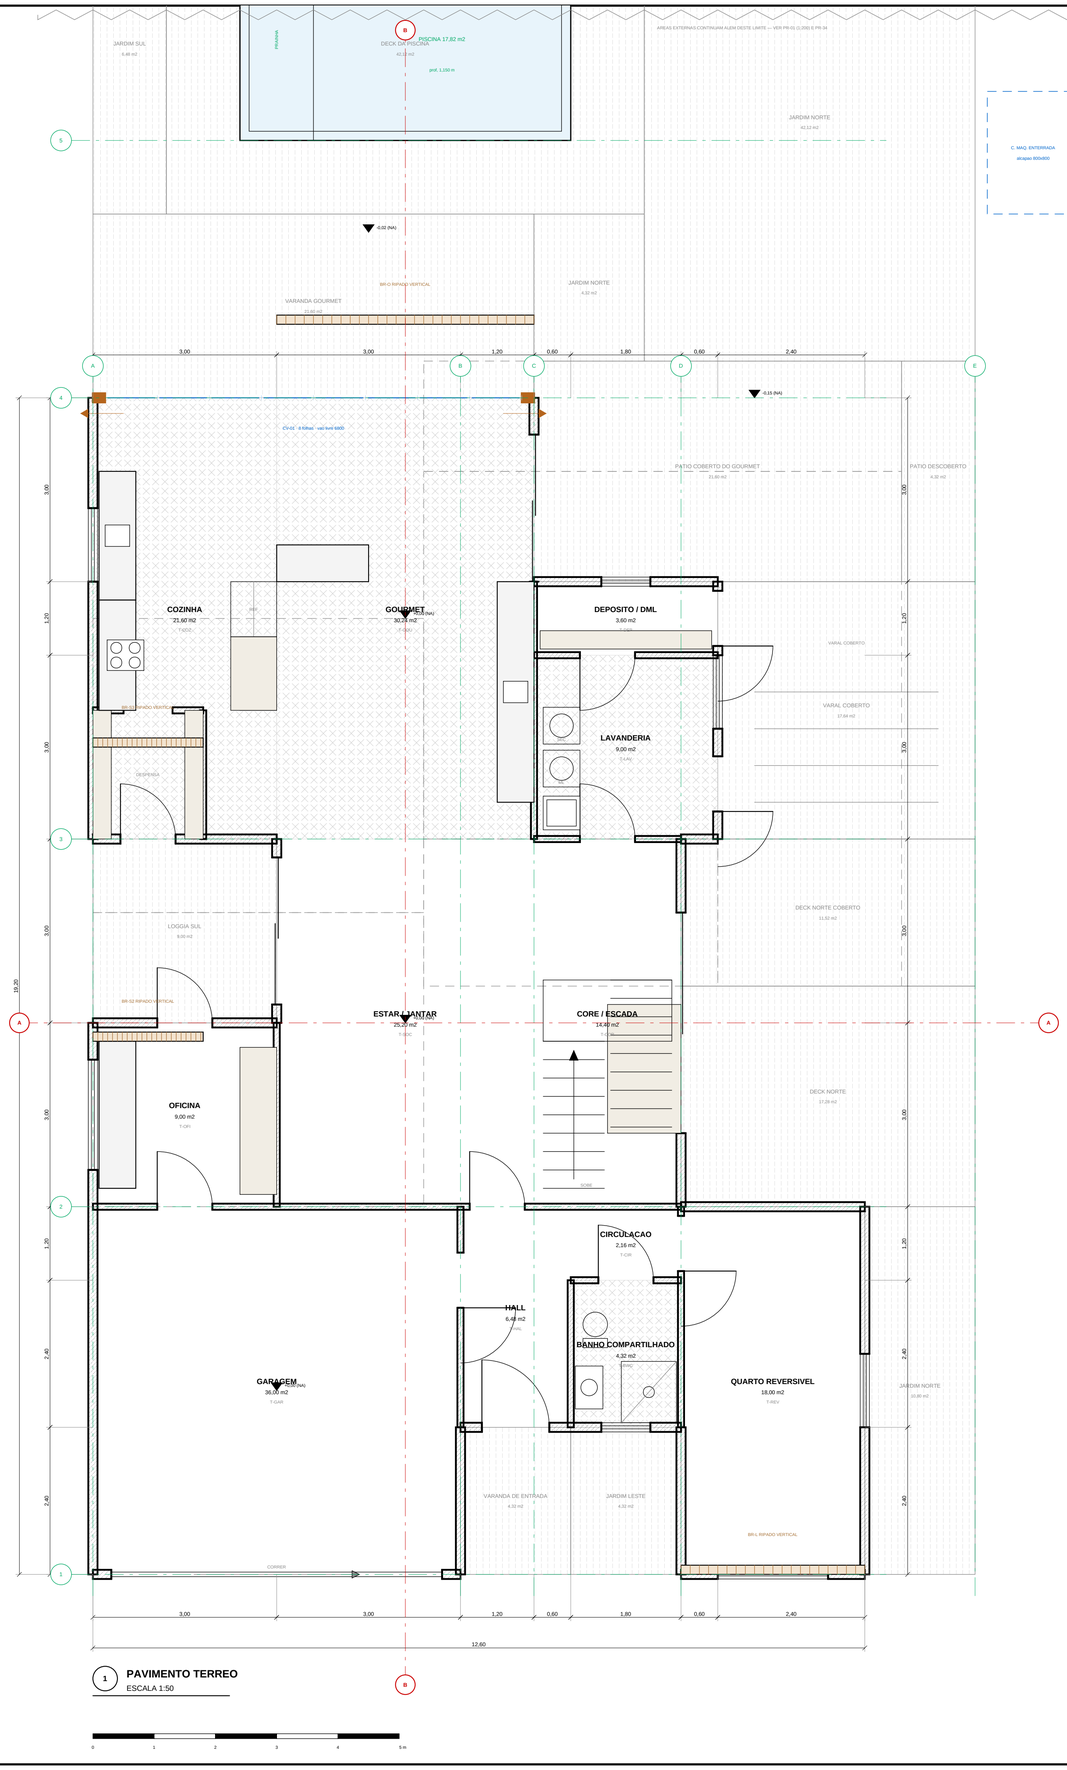


1 **PAVIMENTO TERREO**
ESCALA 1:50

QUADRO DE AREAS — PAVIMENTO TERREO

COD	AMBIENTE	MODULO (mm)	AREA (m2)
T-GAR	GARAGEM	6000x6000	36,00
T-HAL	HALL	1800x3600	6,48
T-BWC	BANHO COMPARTILHADO	1800x2400	4,32
T-CIR	CIRCULACAO	1800x1200	2,16
T-REV	QUARTO REVERSIVEL	3000x6000	18,00
T-OFI	OFICINA	3000x3000	9,00
T-SOC	ESTAR / JANTAR	4200x6000	25,20
T-COR	CORE / ESCADA	2400x6000	14,40
T-COZ	COZINHA	3000x7200	21,60
T-GOU	GOURMET	4200x7200	30,24
T-LAV	LAVANDERIA	3000x3000	9,00
T-DEP	DEPOSITO / DML	3000x1200	3,60
	TOTAL FECHADO		180,00
T-VAR	VARANDA DE ENTRADA (aberta)	1800x2400	4,32
T-JLE	JARDIM LESTE (aberta)	1800x2400	4,32
T-JNO	JARDIM NORTE (aberta)	1800x6000	10,80
T-LOG	LOGGIA SUL (aberta)	3000x3000	9,00
T-DKL	DECK NORTE (aberta)	4800x3600	17,28
T-DKC	DECK NORTE COBERTO (aberta)	4800x2400	11,52
T-VRL	VARAL COBERTO (aberta)	4200x4200	17,64
T-PAT	PATIO COBERTO DO GOURMET (aberta)	6000x3600	21,60
T-PT2	PATIO DESCOBERTO (aberta)	1200x3600	4,32
T-ALP	VARANDA GOURMET (aberta)	7200x3000	21,60
T-DKP	DECK DA PISCINA (aberta)	7800x5400	42,12
T-JS2	JARDIM SUL (aberta)	1200x5400	6,48
T-JN2	JARDIM NORTE (aberta)	1800x2400	4,32
T-JN3	JARDIM NORTE (aberta)	5400x7800	42,12
T-JFU	JARDIM DE FUNDO (aberta)	14400x4800	69,12

MAPA DE ESQUADRIAS DO PAVIMENTO


REF	VAO (mm)	PEIT.	QTD	TIPO
CVE1	7200x2600	0	1	CORTINA DE VIDRO reinstl, 8 folhas de 900 mm
JO1	1200x1200	1100	3	janela de dormitorio, aluminio
JO4	800x900	1500	2	janela alta de banheiro, basculante
JO5	1800x1200	1100	2	janela ampla de dormitorio, aluminio
PO1	1100x2800	0	1	porta principal, alta opaca
PO2	900x2100	0	2	porta interna (familia unificada)
PO4	900x2100	0	7	porta de servico, resistente a umidade
PO6	900x2100	0	2	porta interna de folha SOLIDA com vedacao peri
PGO1	5400x2400	0	1	portao de correr, aluminio ripado
PVI1	3600x2400	0	1	vao social posterior
PVI2	2400x2400	0	2	porta-balcao do estar (familia adicional — ver

LEGENDA E CONVENCOES (NBR 6492 / 8403)

- Elemento seccionado pelo plano de corte (h = 1,50 m)
- Aresta vista / folha de esquadria
- Mobiliario fixo, equipamentos e simbologia
- Projecao do pavimento superior e da cobertura
- Eixo modular e linha de corte
- Linha de cota e linha auxiliar



PERCURSO SOLAR — MANAUS 3 S

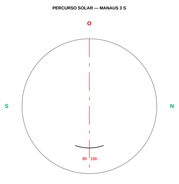

faces L e O: sol a 30 graus

-> exigem brise VERTICAL

faces N e S: sol 63 a 87 graus

-> beiral de 1.200 mm resolve

NOTAS

- Dimensoes em milimetros; cotas de nivel em metros.
- Malha modular 600 mm; cotas eixo a eixo.
- Parede externa 150 mm / divisoria interna 100 mm (H).
- Mobiliario fixo indica pontos de agua e esgoto (NBR 6492).

PROJETO PORTO REAL

RESIDENCIA UNIFAMILIAR | MANAUS - AM | SUS8 TARUMA (H)

PROJETO ARQUITETONICO

PLANTA BAIXA — PAVIMENTO TERREO

BASE GEOMETRICA	ESCALA	EMISSAO	PRANCHA
Lista Consolidada (pos-R32 (preval4ext)	1:50	ESTUDO PRELIMINAR R52	02
UNIDADE MESTRE: mm	FORMATO A1	NAO LIBERADO PARA OBRA	de 40 REV R52
	MALHA 600/300/150	SEM ART / RRT	