


VERIFICACAO NBR 9050

ITEM	EXISTENTE	PROJETO	
Vel. livre de porta	800 mm	940 mm (altura de 900)	OK
Circulo de giro 360 graus	1.500 mm	hall, banheiro e quarto	OK
Desnivel sem rampas	até 5 mm	soluções niveladas	OK
Largura de circulação	900 mm	1.800 mm no hall	OK
Barras de apoio	relívato previsto	ambulador no PTE 1 e PTE 2	OK
Barrameda acessível	altura livre 750 mm	sem gabaritos sob a calha	OK
Contraste e interruptor	600 a 1.000 mm	a definir no eletrico	pendente



FLUXOS — SEPARACAO DE CIRCUITOS

CIRCUITO	PERCURSO	CRIÇA O SOCIAL?
Servico	garagem -> oficina -> lavanderia -> cozinha -> despensa	NÃO
Social	entrada -> hall -> estar -> gourmet -> alameda -> piscina	—
Área íntima	hall -> banheiro compartilhado -> quarto compartilh	NÃO
Área superior	hall -> cora -> hall superior -> suíte	NÃO
Uso e carga	cozinha -> despensa -> reserv. sal	NÃO

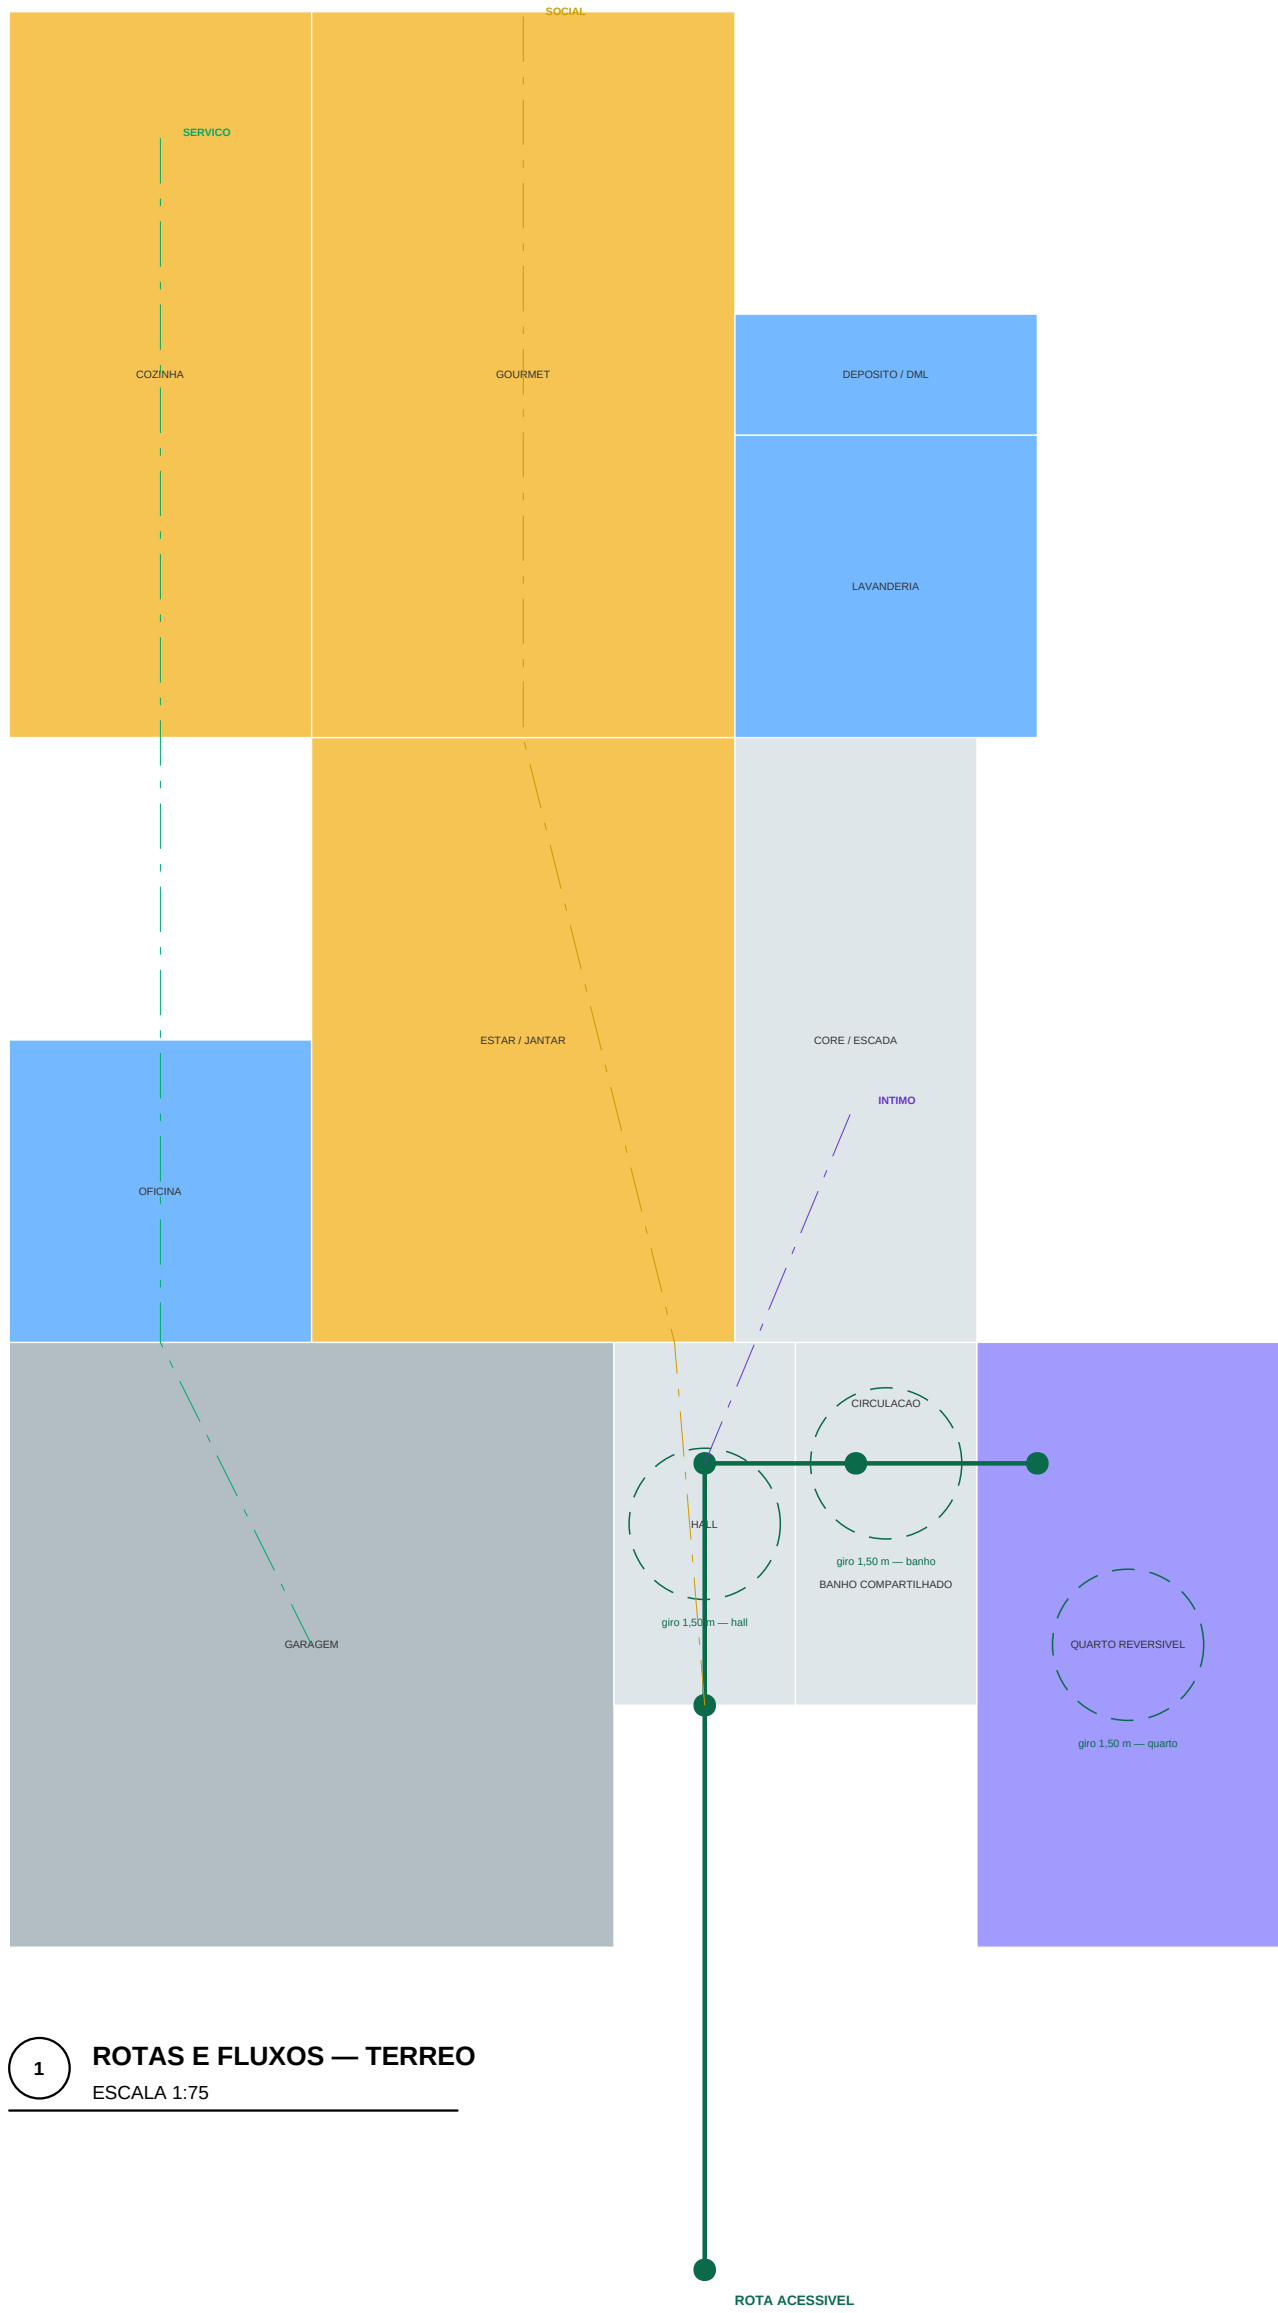

1 ROTAS E FLUXOS — TERREO
ESCALA 1:75

- NOTAS
- * Rota acessível do passeio ao quarto reservado e ao banheiro compartilhado.
 - * Circulo de giro de 1.500 mm verificado nos pontos de manobra.
 - * Porta de correr de 900 mm no banheiro libera a área de manobra.
 - * Reforço para barras de apoio embutidas antes do fechamento das placas.

PROJETO PORTO REAL

RESIDENCIA UNIFAMILIAR (MANAUS - AM) | SUELE TATIANA-PS

PROJETO ARQUITETONICO

ACESSIBILIDADE E FLUXOS

BASE GEOMETRICA	ESCALA	EMISSAO	PROJECION
União Consolidada	1:75	ESTUDO PRELIMINAR RS2	17
RS2 (previsão)	FORMATO A1	NÃO LIBERADO PARA OBRA	
UNIDADE MESTRE: 040	MALHA 600/600/300	SEM ART / RNT	06-48 REV RS2