
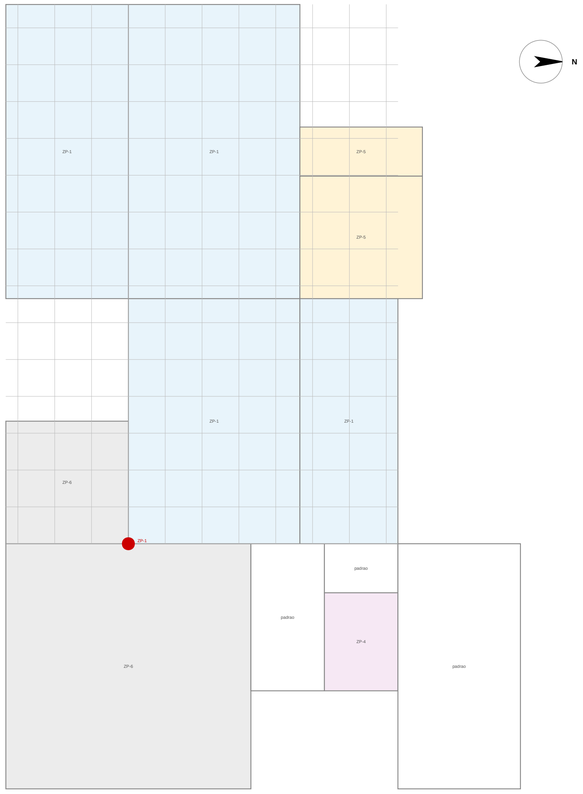


1 PAGINACAO — TERREO

ESCALA 1:75

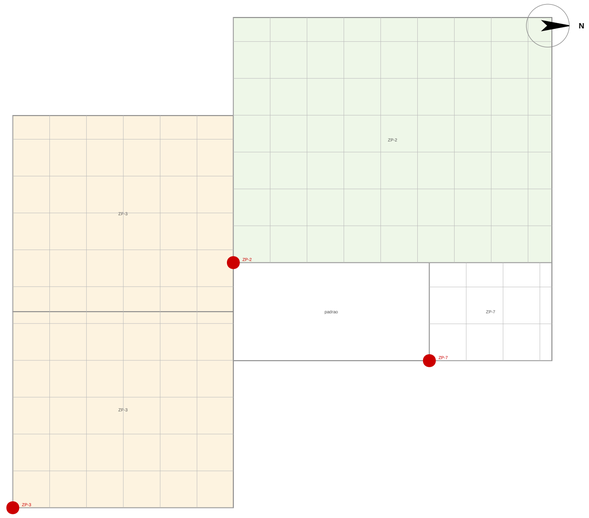

2 PAGINACAO — SUPERIOR

ESCALA 1:75

ZONAS DE PAGINACAO

ZONA	PECA	ORIGEM	AMBIENTES	PECA ESPECIFICADA	PIOR RECORTE	CRITERIO
ZP-1	piso	(5400, 13200)	T-SOC, T-COR, T-GOU, T-COZ	porcelanato retificado 900 x 900	284	lita social inteira em uma malha: origem no eixo da porta do h
ZP-2	piso	(7800, 19200)	S-MAS	porcelanato retificado 900 x 900	582	origem no eixo da porta da suite
ZP-3	piso	(2400, 13200)	S-S02, S-S03	porcelanato retificado 900 x 900	288	suites 02 e 03 na mesma malha: a parede entre elas e divisoria
ZP-7	piso	(12600, 16800)	S-LOU	porcelanato retificado 900 x 900	292	o lounge tem porta e nao e integrado a nada: pagina do proprio
ZP-4	parede	canto do ambiente	T-BWC, S-S02/BANHO, S-S03/BANHO, S-MAS/BANHO	ceramico retificado 300 x 600	280	ate o forro rebaixado de 2.400 (que ja existe para a exaustao)
ZP-5	parede	canto do ambiente	T-LAV, T-DEP	ceramico retificado 300 x 600	280	meia parede de 1.800 mm atras do tanque, das maquinas e das pr
ZP-6	monolitico	(2400, 13200)	T-OFI, T-GAR	cimentício polido	—	piso cimentício polido de alta resistencia: sem paginacao cera

NOTAS

- Paginar no projeto e decidir onde fica o corte. Nao paginar e deixar o corte aparecer no lugar mais visivel.
- Ambientes integrados recebem UMA malha: a junta desalinhada no meio da sala nao tem parede para disfarcar.
- Recorte mineiro aceito 33% da peca, abaixo de 20% o recorte descola e e reprovado.

PROJETO PORTO REAL

RESIDENCIA UNIFAMILIAR | MANAUS - AM | SUS8 TARUMA (H)

PROJETO ARQUITETONICO

PAGINACAO DE PISO E ZONAS DE REVESTIMENTO

BASE GEOMETRICA	ESCALA	EMISSAO	PRANCHA
Lista Consolidada pos-R32 (prevalece)	1:75 FORMATO A1 MALHA 600/300/150	ESTUDO PRELIMINAR RS2 NAO LIBERADO PARA OBRA SEM ART / RRT	24 de 40 REV RS2

UNIDADE MESTRE: mm