


1 PARES FONTE / RECEPTOR
ESCALA s/ escala

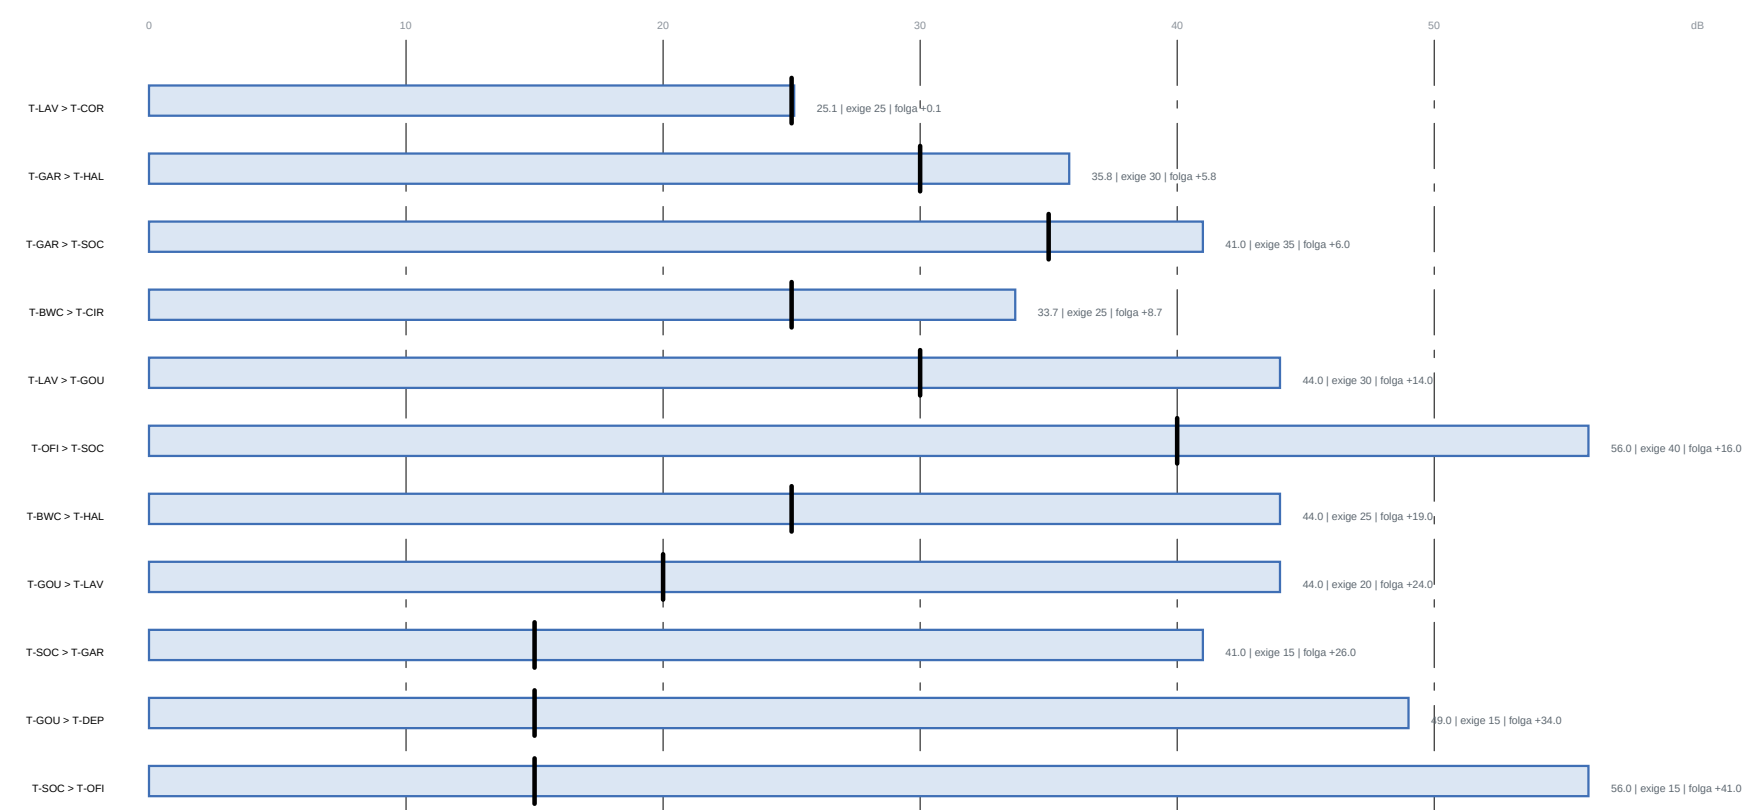

barras = isolamento obtido; traço vertical = exigido (nível da fonte menos limite do receptor, NBR 10152)

O QUE MUDOU EM R52

ONCE	ANTES	DEPOIS	POIS QUE
Bailete compartilhado - hall de entrada	porta de correr (15) — conjunto de 25,2 dB	porta CISA, 44 dB	o acesso de visita passou para a circulação
Bailete compartilhado - quarto reservado	porta cca (19-20) — conjunto de 25,1 e 25,1, média 25	porta CISA, 44 dB	era a por passageiros da sala, e não era a visita!
Hall + gangueiro	porta cca — 25,8 dB, média 30	PDS isolada vertical — 35,1 dB	porta entre gangueiro e sala não tinha nada para ser medida
Bailete compartilhado - circulação	nao havia porta	PDS isolada vertical — 33,7 dB, média 25	unico acesso do banheiro, e abria para fora
Rua do Chuveiro	encosto na parede de hall	Casco torçao, sob a janela alta	compartimento da porta nova, e regra dos 900 mm de boa respiração a primeira tentativa

TABELAS ADOTADAS

ITEM	VALOR	FONTE
Fone: sala control	15 (R\$)	prática corrente de acústica
Fone: sala de piano	15 (R\$)	prática corrente de acústica
Fone: cozinha e gourmet	15 (R\$)	prática corrente de acústica
Fone: estar e jantar	15 (R\$)	prática corrente de acústica
Fone: garagem	15 (R\$)	prática corrente de acústica
Fone: máquina de lavar e secar	15 (R\$)	prática corrente de acústica
Fone: oficina	60 (R\$)	prática corrente de acústica
Limite: banheiro	45 (R\$)	NBR 15152-2017 (circulação e entrada adjacentes)
Limite: circulação	45 (R\$)	NBR 15152-2017 (circulação e entrada adjacentes)
Limite: cozinha	45 (R\$)	NBR 15152-2017 (circulação e entrada adjacentes)
Limite: depósito	35 (R\$)	NBR 15152-2017 (circulação e entrada adjacentes)
Limite: dormitório	35 (R\$)	NBR 15152-2017 (circulação e entrada adjacentes)
Limite: entrada	45 (R\$)	NBR 15152-2017 (circulação e entrada adjacentes)
Limite: estar	45 (R\$)	NBR 15152-2017 (circulação e entrada adjacentes)
Limite: garagem	15 (R\$)	NBR 15152-2017 (circulação e entrada adjacentes)
Limite: office	45 (R\$)	NBR 15152-2017 (circulação e entrada adjacentes)
Limite: oficina	15 (R\$)	NBR 15152-2017 (circulação e entrada adjacentes)
Limite: sanário	50 (R\$)	NBR 15152-2017 (circulação e entrada adjacentes)
Porta: acústica	R\$ 25 (R\$)	taxa de mercado declarada
Porta: correr	R\$ 15 (R\$)	taxa de mercado declarada
Porta: vidro	R\$ 25 (R\$)	taxa de mercado declarada
Porta: solid	R\$ 25 (R\$)	taxa de mercado declarada
Porta: vidro+solid	R\$ 35 (R\$)	taxa de mercado declarada

NOTAS

- Esta prancha existe porque o proprietário perguntou e que 101 verificações não sabem responder: quem entra na casa ouve o chuveiro do banheiro da entrada?

* Ouvia. A parede era boa (Rw 44) e a porta era de correr (Rw 25); o conjunto entregava 20 dB. Em acústica o elo fraco DOMINA — não se faz média aritmética de isolamento, se soma energia que passa.

- Isolamento só se exige ENTRE zonas. Dentro da fita social o ruído não é defeito, é o programa.

* D adotado igual ao R composto (simplificação declarada). Isto é pre-verificação de projeto, não ensaio de campo da NBR 15575-3.

PROJETO PORTO REAL			
RESIDENCIA UNIFAMILIAR 1 MANUS - AM - 1505 TARUMÁ (P)			
PROJETO DE ARQUITETONICO			
DESEMPENHO ACUSTICO ENTRE AMBIENTES			
BASE GEOMETRICA	ESCALA	EMISSAO	RECEPCAO
Unidade Consolidada	s/ escala	ESTUDO PRELIMINAR R52	39
ISO-R52 (previsto)		NÃO LIBERADO PARA OBRA	
INDICE MEDIDA (m²)	FORMATO A1	SEM AM / RWT	
	MAQUA 600/300/300		OK 42 REV R52