
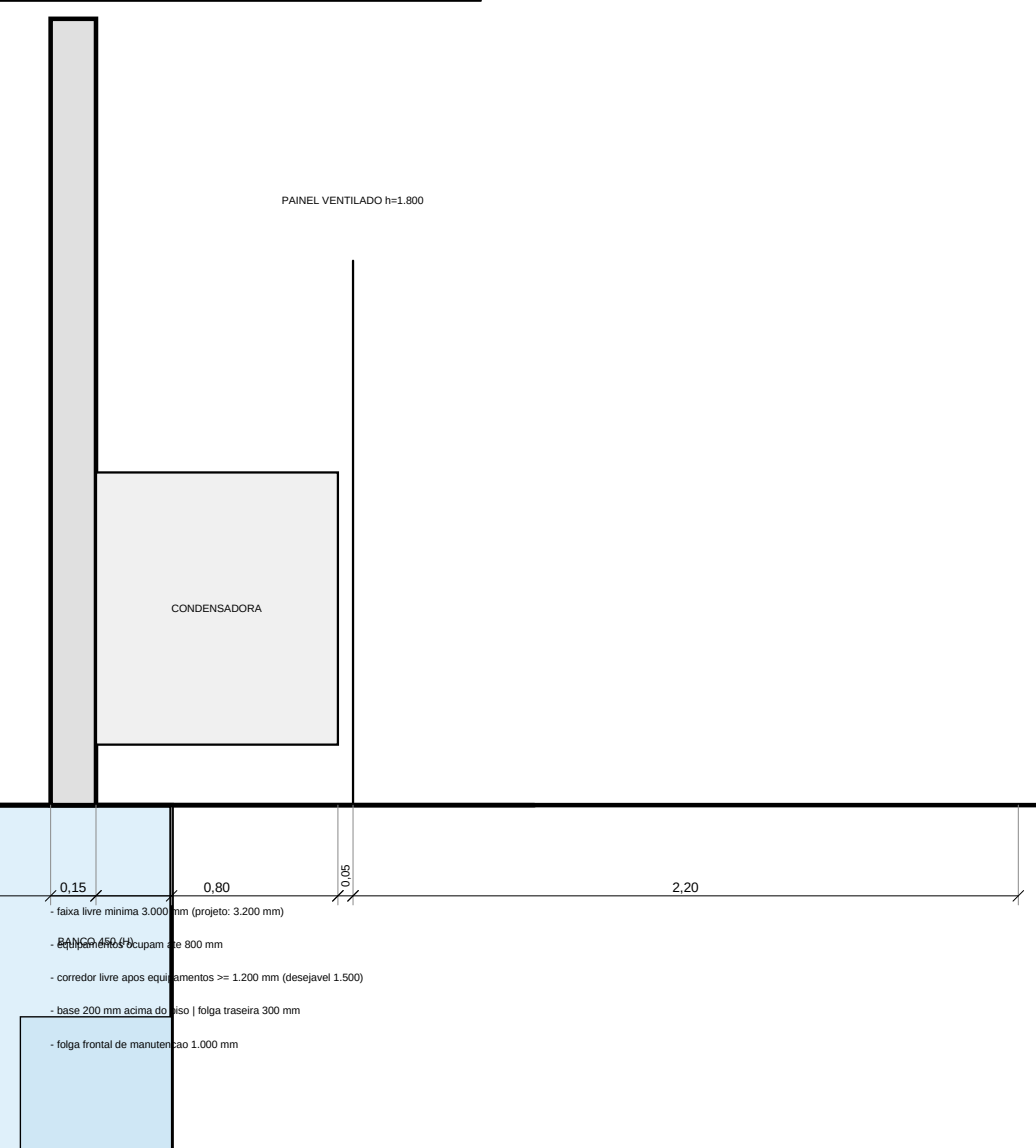


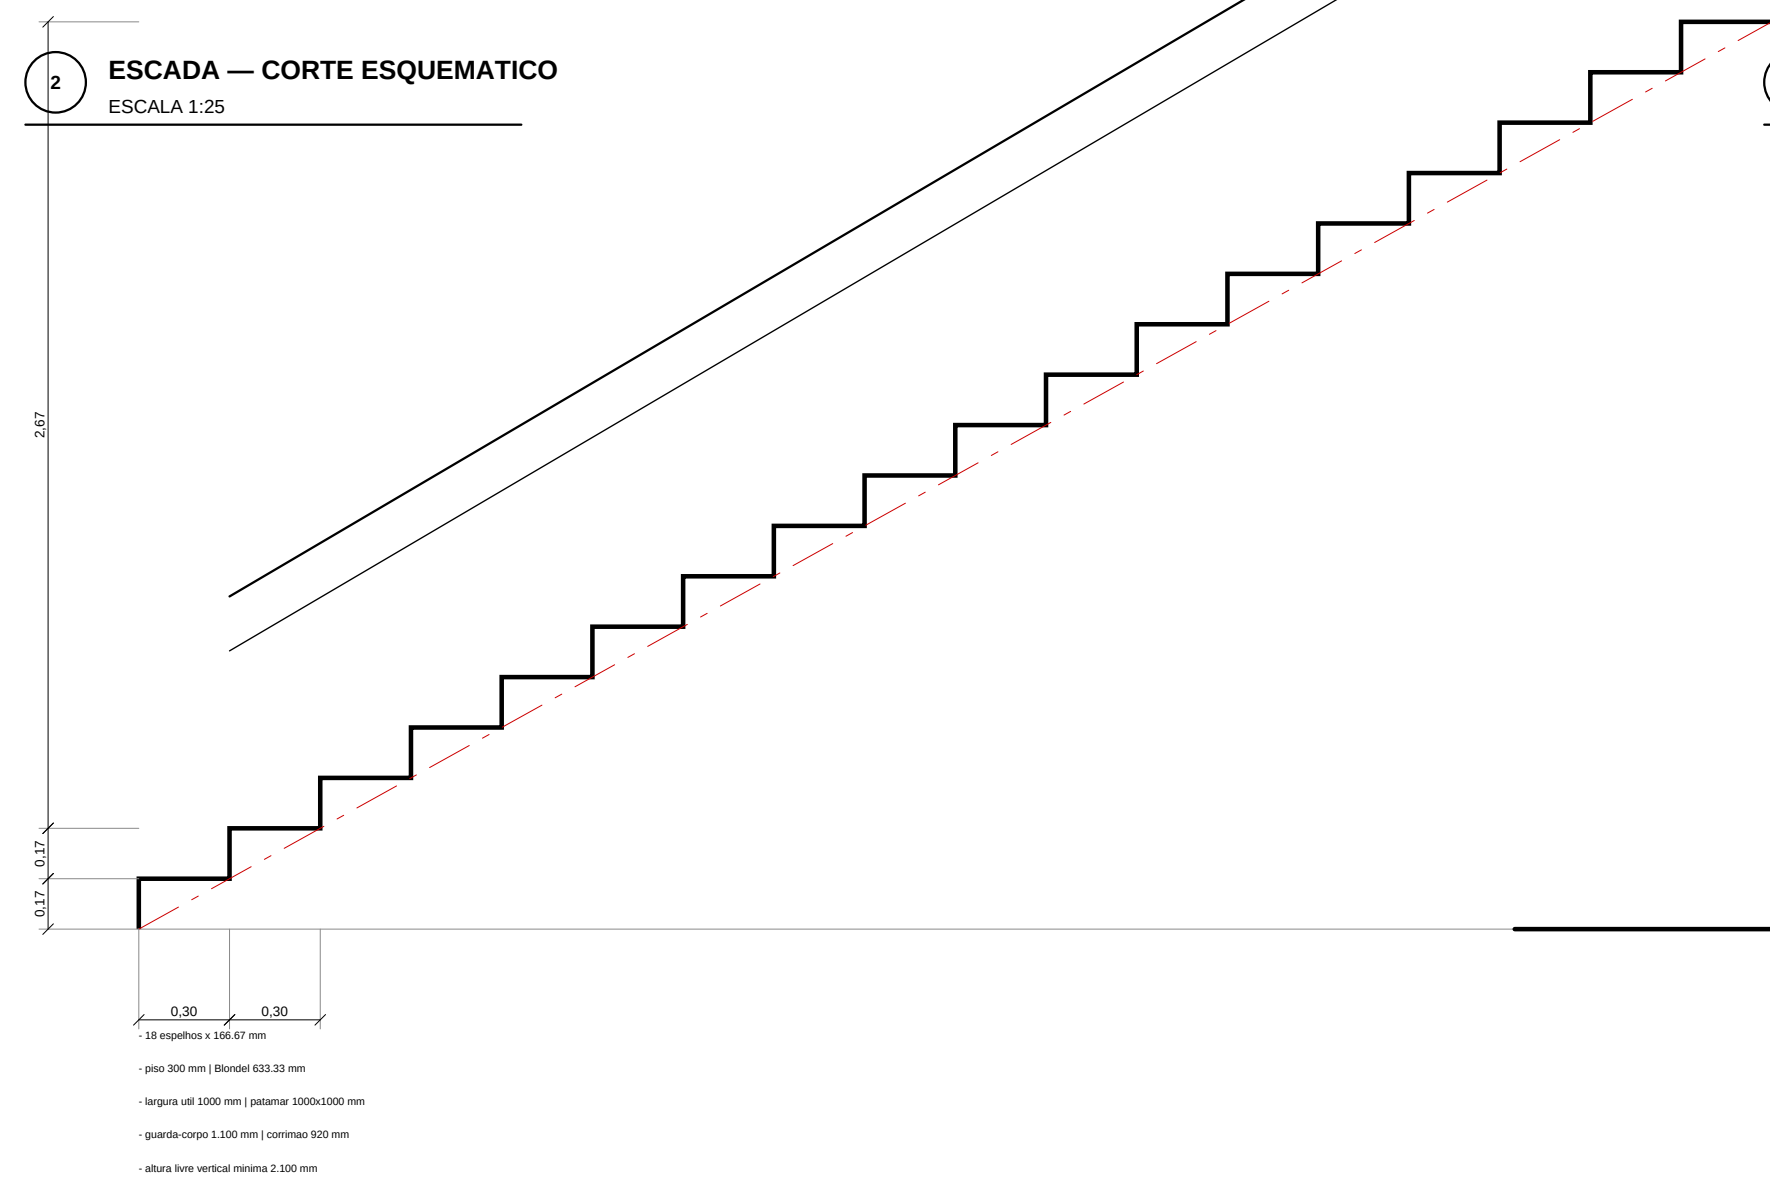

- Detalhes de estudo — não liberados para fabricação ou corte (sem nesting codificado).
- Parede externa consolidada em 150 mm; divisória interna em 100 mm (H).
- Escada reconciliar com estrutura, guarda-corpo e espessura de acabamento antes de definitiva.

PROJETO PORTO REAL			
RESIDENCIA UNIFAMILIAR (MANAUS - AM) (SOLTA TAMBORA 05)			
PROJETO ARQUITETONICO			
DETALHES CONSTRUTIVOS AMPLIADOS			
BASE GEOMETRICA Linha Consolidada proj02 (proj01c) USO: MESTRE - AM	ESCALA indicada FORMATO A1 MILIMETROS (1:100)	ENTRADA ESTUDO PRELIMINAR R-05 NÃO LIBERADO PARA OBRA SEM ART - 1997	FUNÇÃO 10 05.10.1997