



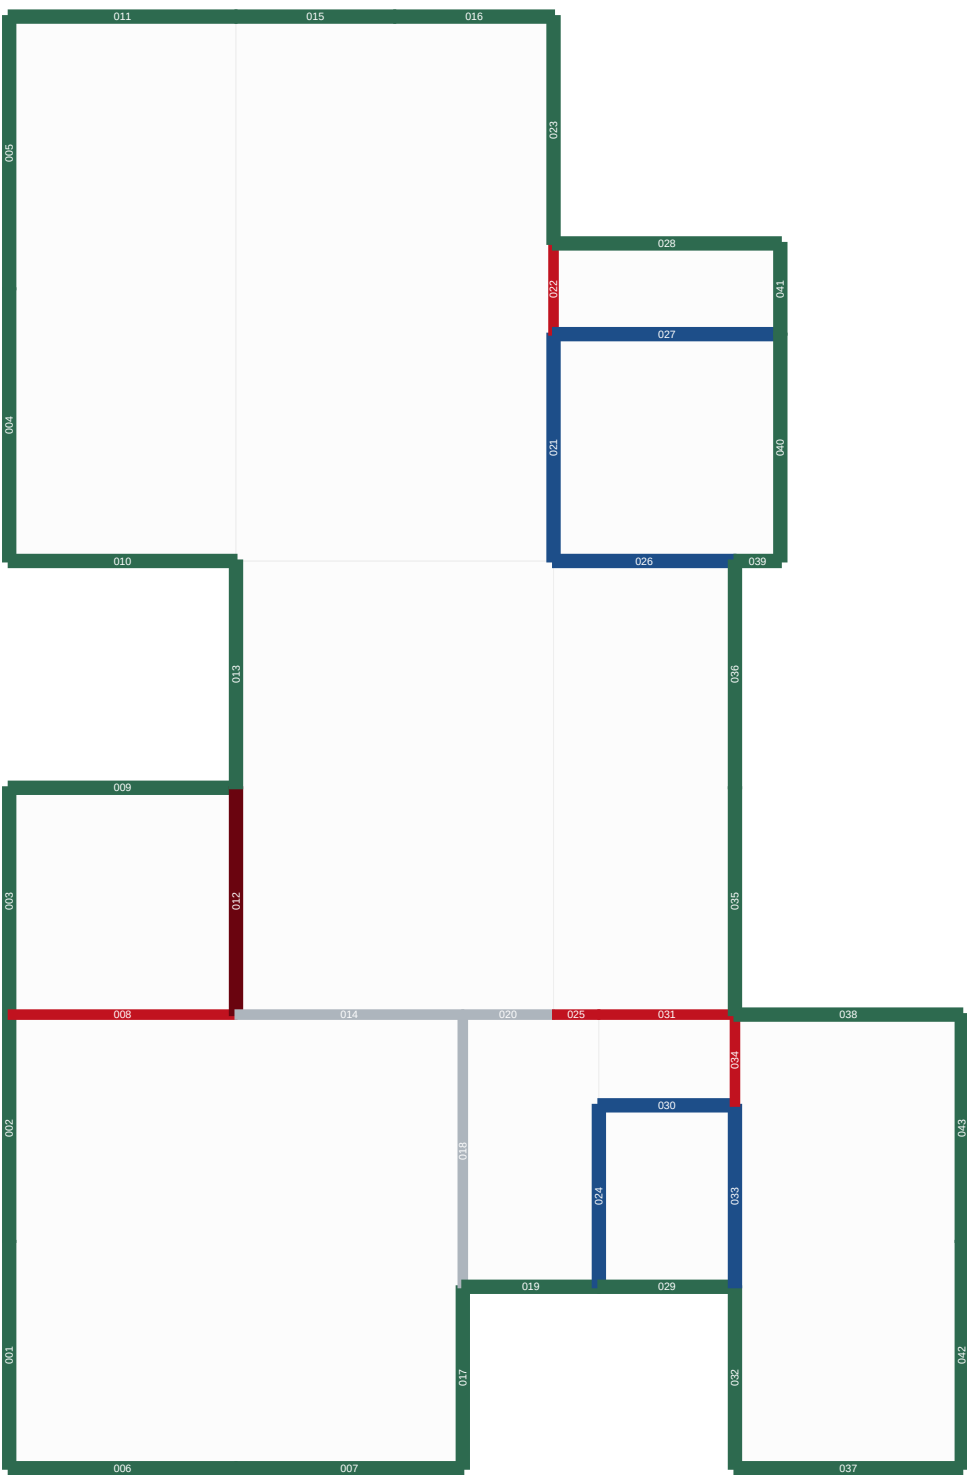

1 PAGINACAO — TERREO  
ESCALA 1:100

QUANTITATIVO DE PAINES E MONTANTES

| FAMILIA | PAINES | MONTANTES | PI de perfil | COMPOSICAO                                                      |
|---------|--------|-----------|--------------|-----------------------------------------------------------------|
| PA-1    | 12     | 45        | 127,4        | dupla chapa 12,5 + montante 45 x 14 x 60 + dupla chapa 12,5     |
| PA-2    | 1      | 6         | 15,6         | dupla chapa 12,5 + perfil oculto + montante 70 x 14 x 60        |
| PE-1    | 30     | 283       | 683,8        | linhas 32 x 30 x 30 (SDO eng) + montante 30 x 14 x 30 +         |
| PA-3    | 6      | 31        | 30,6         | perfil 60 x 12,5 + montante 30 x 14 x 30 + perfil 12,5 + rebato |
| PI-1    | 4      | 22        | 57,2         | perfil 12,5 + montante 70 x 14 x 30 + perfil 12,5               |
| TOTAL   | 73     | 371       | 964,6        |                                                                 |

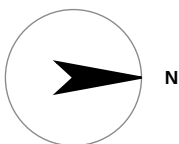

EXTRATO DA LISTA DE PAINES (26 de 73)

| CODIGO | FAMILIA | LARGO (mm) | ALT (mm) | MONT. | PROV. |
|--------|---------|------------|----------|-------|-------|
| PT-001 | PE-1    | 3000       | 2000     | 6     | T     |
| PT-002 | PE-1    | 3000       | 2000     | 6     | T     |
| PT-003 | PE-1    | 3000       | 2000     | 6     | T     |
| PT-004 | PE-1    | 3000       | 2000     | 7     | T     |
| PT-005 | PE-1    | 3000       | 2000     | 7     | T     |
| PT-006 | PE-1    | 3000       | 2000     | 6     | T     |
| PT-007 | PE-1    | 3000       | 2000     | 6     | T     |
| PT-008 | PA-1    | 3000       | 2000     | 6     | T     |
| PT-009 | PE-1    | 3000       | 2000     | 6     | T     |
| PT-010 | PE-1    | 3000       | 2000     | 6     | T     |
| PT-011 | PE-1    | 3000       | 2000     | 6     | T     |
| PT-012 | PA-2    | 3000       | 2000     | 6     | T     |
| PT-013 | PE-1    | 3000       | 2000     | 6     | T     |
| PT-014 | PI-1    | 3000       | 2000     | 6     | T     |
| PT-015 | PE-1    | 2100       | 2000     | 4     | T     |
| PT-016 | PE-1    | 2100       | 2000     | 4     | T     |
| PT-017 | PE-1    | 2400       | 2000     | 5     | T     |
| PT-018 | PA-1    | 3000       | 2000     | 7     | T     |
| PT-019 | PE-1    | 1800       | 2000     | 4     | T     |
| PT-020 | PA-1    | 1200       | 2000     | 3     | T     |
| PT-021 | PA-1    | 3000       | 2000     | 6     | T     |
| PT-022 | PA-1    | 1200       | 2000     | 3     | T     |
| PT-023 | PE-1    | 3000       | 2000     | 6     | T     |
| PT-024 | PA-1    | 3000       | 2000     | 6     | T     |
| PT-025 | PA-1    | 600        | 2000     | 3     | T     |
| PT-026 | PA-1    | 2400       | 2000     | 6     | T     |

- NOTAS
- \* Painéis limitados a 3000 mm por manuseio e transporte.
  - \* Montantes a cada 600 mm, 400 mm onde cabido no revestimento exigido.
  - \* Não fixar a peça entre em perfil sem código, largura, altura, espessura, material e revest.
  - \* Numeração por pavimento, a família define a composição interna do painel.

PROJETO PORTO REAL

RESIDENCIA UNIFAMILIAR (MANAUS - AM) | SOUZA TATIANA-PS

PROJETO ARQUITETONICO

PAGINACAO DE PAINES — LIGHT STEEL FRAME

|                                                                                   |                                                              |                                                                              |                                        |
|-----------------------------------------------------------------------------------|--------------------------------------------------------------|------------------------------------------------------------------------------|----------------------------------------|
| BASE GEOMETRICA<br>Lista Consolidada<br>em PDF (previsão)<br>UNIDADE: METROS - MM | ESCALA<br><b>1:100</b><br>FORMATO: A1<br>MARGEM: 60/50/50/50 | EMISSAO<br>ESTUDO PRELIMINAR R05<br>TUDO LIBERADO PARA OBRA<br>SEM ART / RNT | PROJETO<br><b>18</b><br>DE 25 REVIZOES |
|-----------------------------------------------------------------------------------|--------------------------------------------------------------|------------------------------------------------------------------------------|----------------------------------------|