




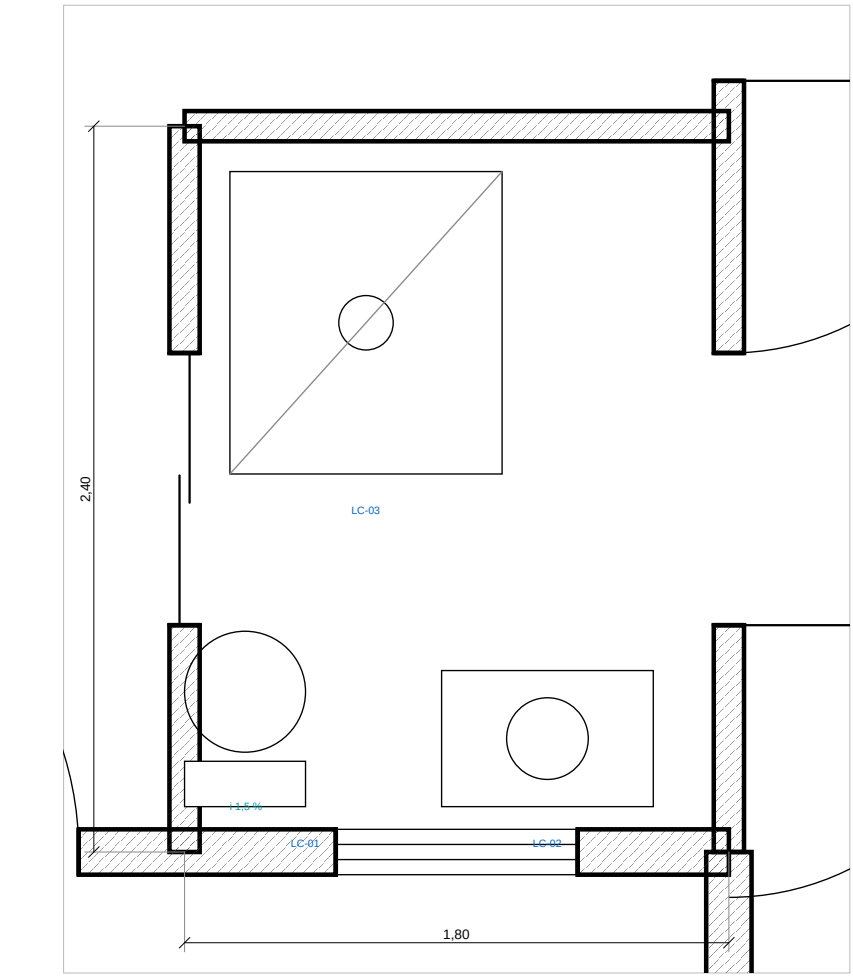


1 BANHO SOCIAL
ESCALA 1:25

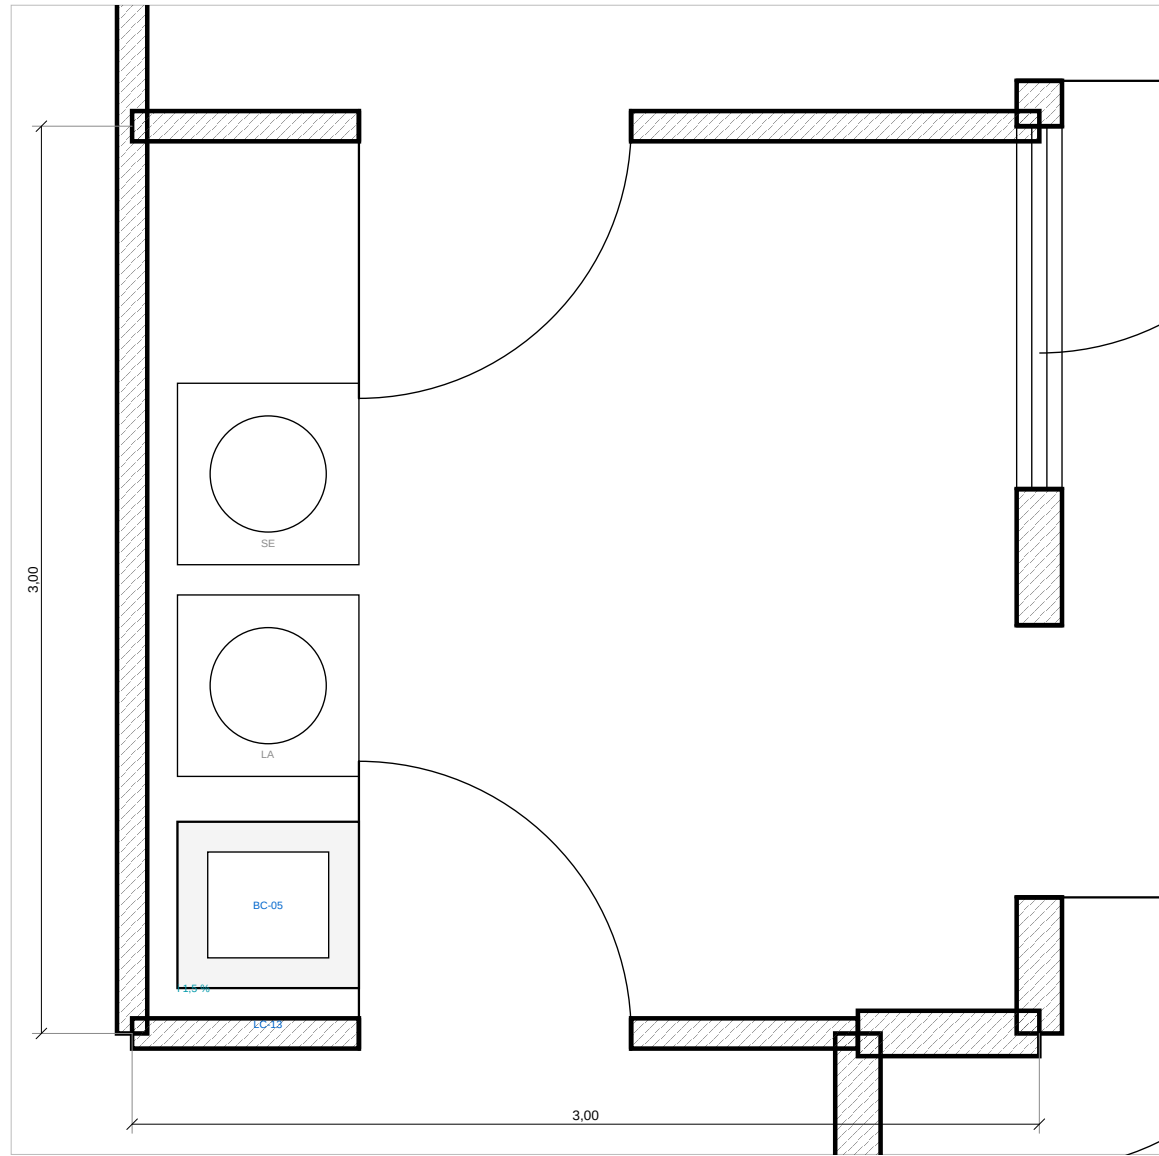

2 LAVANDERIA
ESCALA 1:25

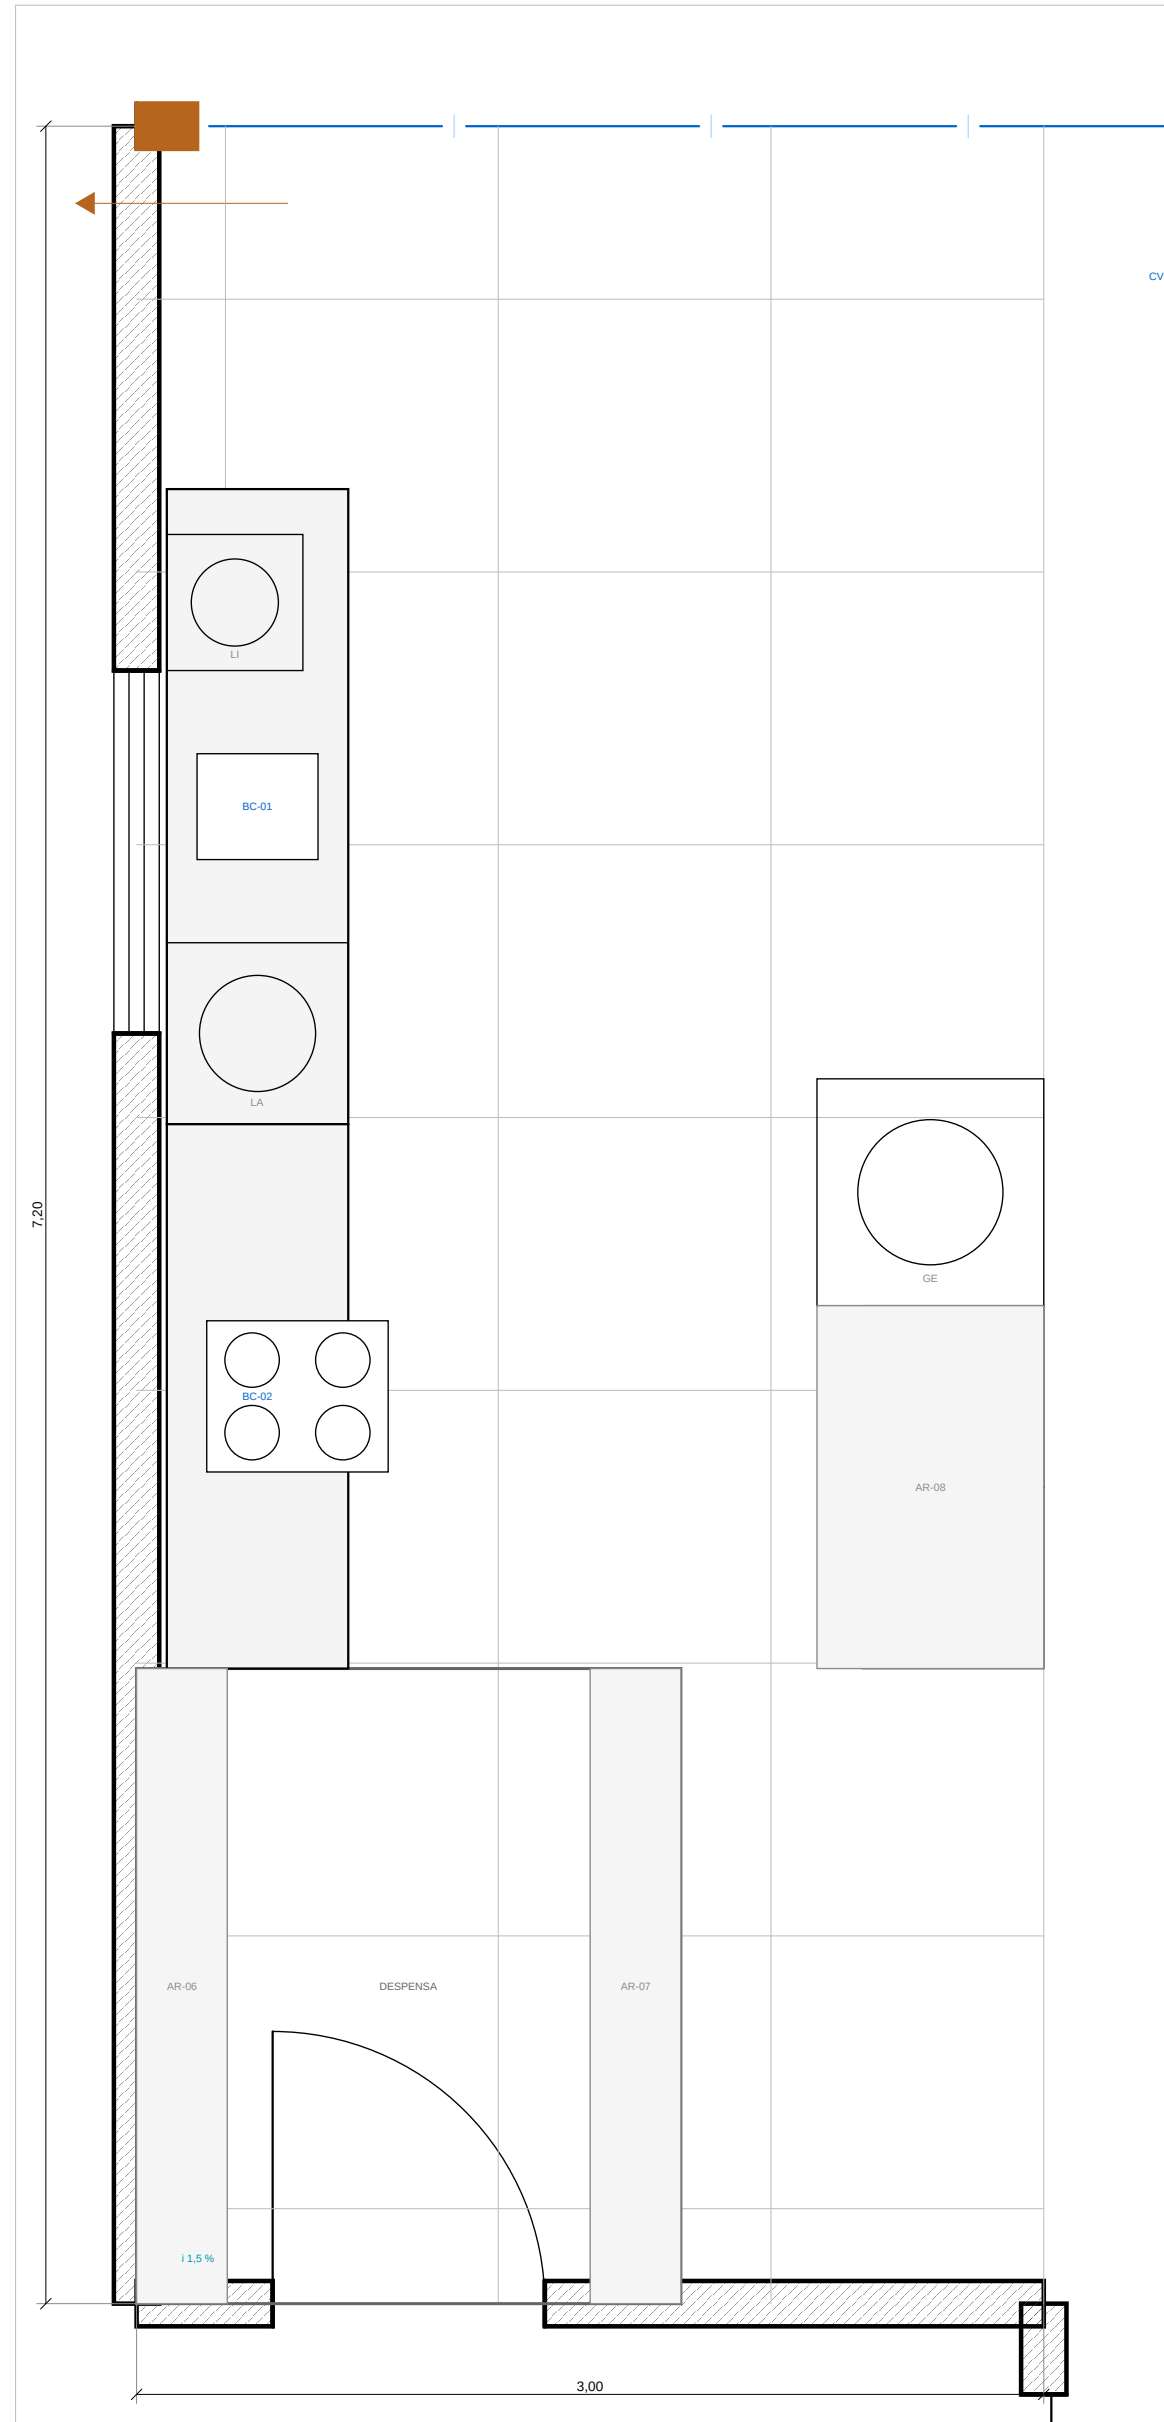

3 COZINHA
ESCALA 1:25

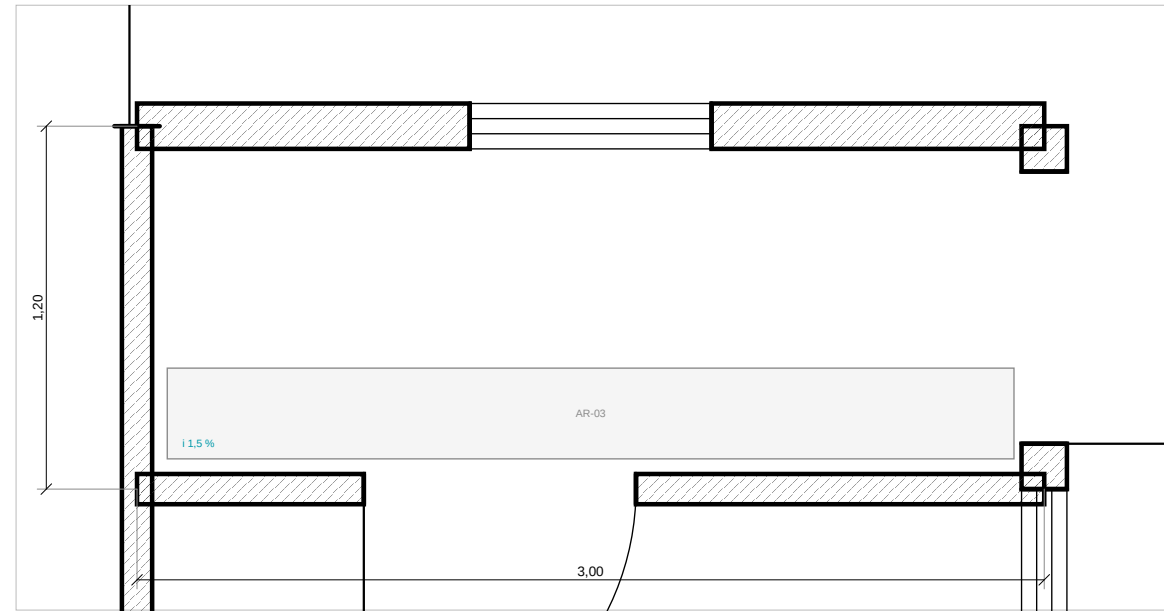

4 DEPOSITO / DML
ESCALA 1:25

PAGINACAO VERIFICADA — PECAS INTEIRAS + RECORTE EM CADA PONTA

AMB	AMBIENTE	ZONA	PEÇA	EXO X	EXO Y	ALTURA (mm)
T-BWC	BANHO SOCIAL	ZP-4	paredo	0 + 0200	0 + 0000	2400 (2 Ruas + 100)
T-LAV	LAVANDERIA	ZP-5	paredo	0 + 0200	4 + 0500	1800 (2 Ruas + 100)
T-COC	COZINHA	ZP-1	pis	0 + 0200	7 + 11000	—
T-DMP	DEPOSITO / DML	ZP-5	paredo	0 + 0200	1 + 0500	1800 (2 Ruas + 100)

- NOTAS
- * Pignecas de piso em linha fina, a malha vem da ZONA de pignecas, não do canto do ambiente.
 - * Peca de piso porcelanado retificado 300 x 300, parede ceramico retificado 300 x 600, jato 2 mm.
 - * Camerito de 1.5 % para o piso em toda area molhada, solteira elevada 15 mm nos bicos.
 - * Representacao: manta liquida em 2 demoes, subido 300 mm na parede e 1.800 mm nos bicos.

PROJETO PORTO REAL

RESIDENCIA UNIFAMILIAR (MARIAUS - AM) | SOUZA TATIANA-PS

PROJETO ARQUITETONICO

AMPLIACOES DE AREA MOLHADA — TERREO

BASE GEOMETRICA Linha Consolidada ISO A1/2 (previsão) UNIDADE MESTRE: mm	ESCALA 1:25 FORMATO A1 MILHA 600/500/300	EMISSAO ESTUDIO PRELIMINAR R05 NAO LIBERADO PARA OBRA SEM ART / RNT	PROJECIA 22 06-25 REV-05
---	---	--	--------------------------------