




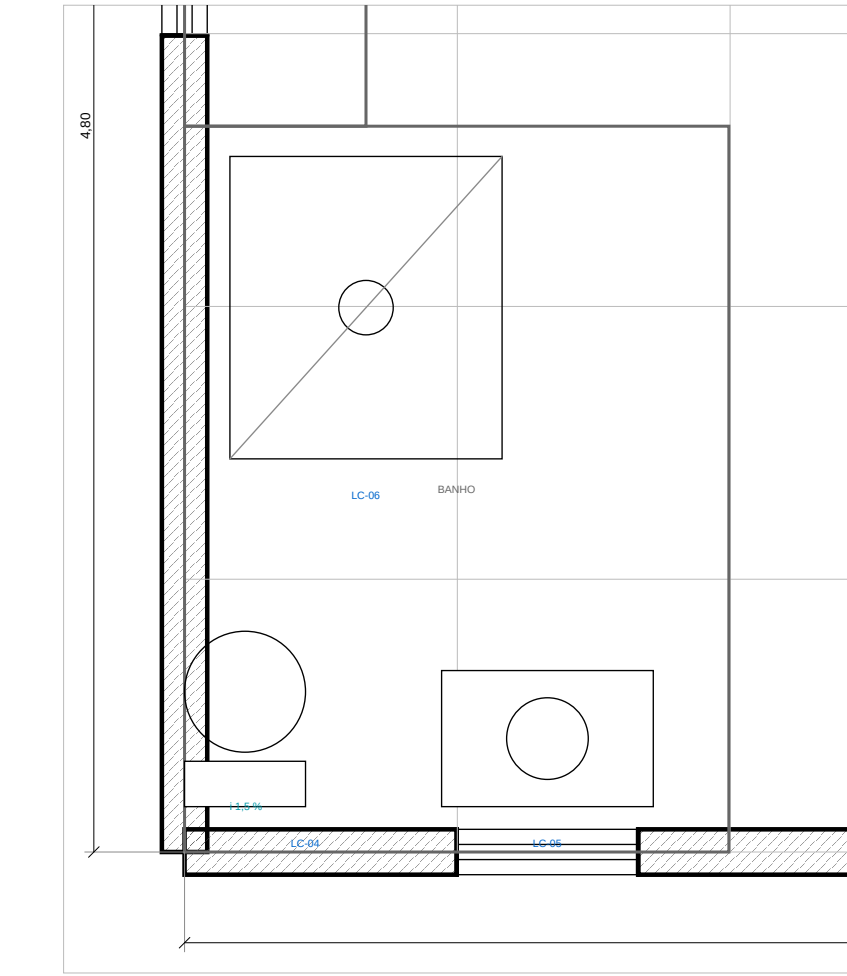


1 SUITE 02 — BANHO  
ESCALA 1:25

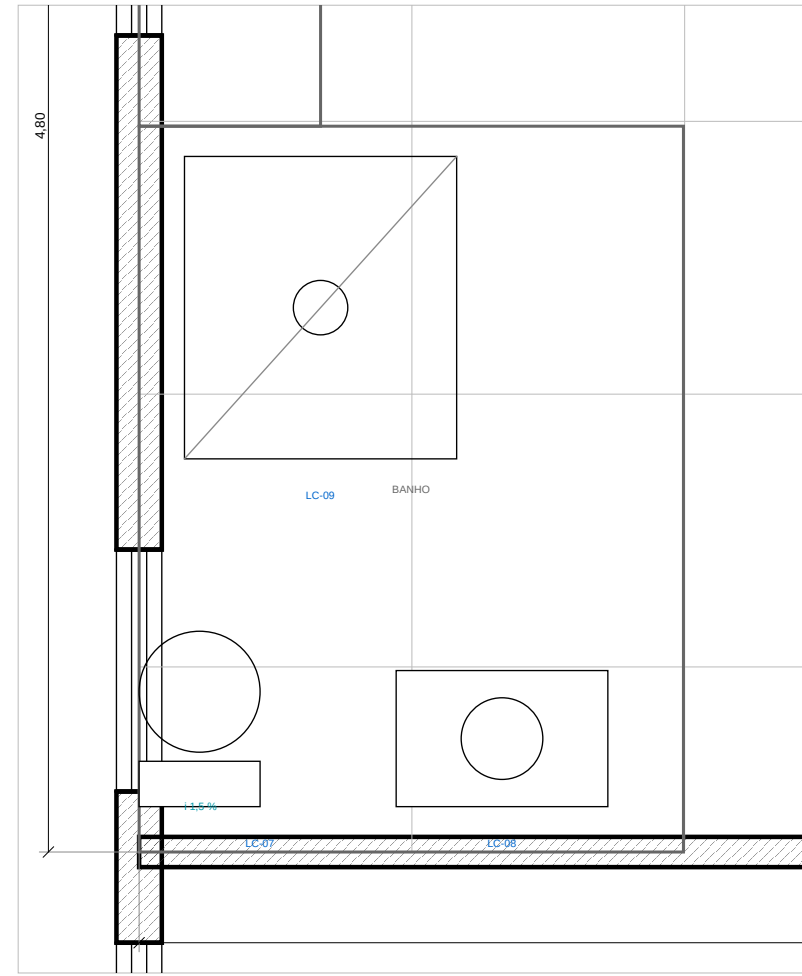

2 SUITE 03 — BANHO  
ESCALA 1:25

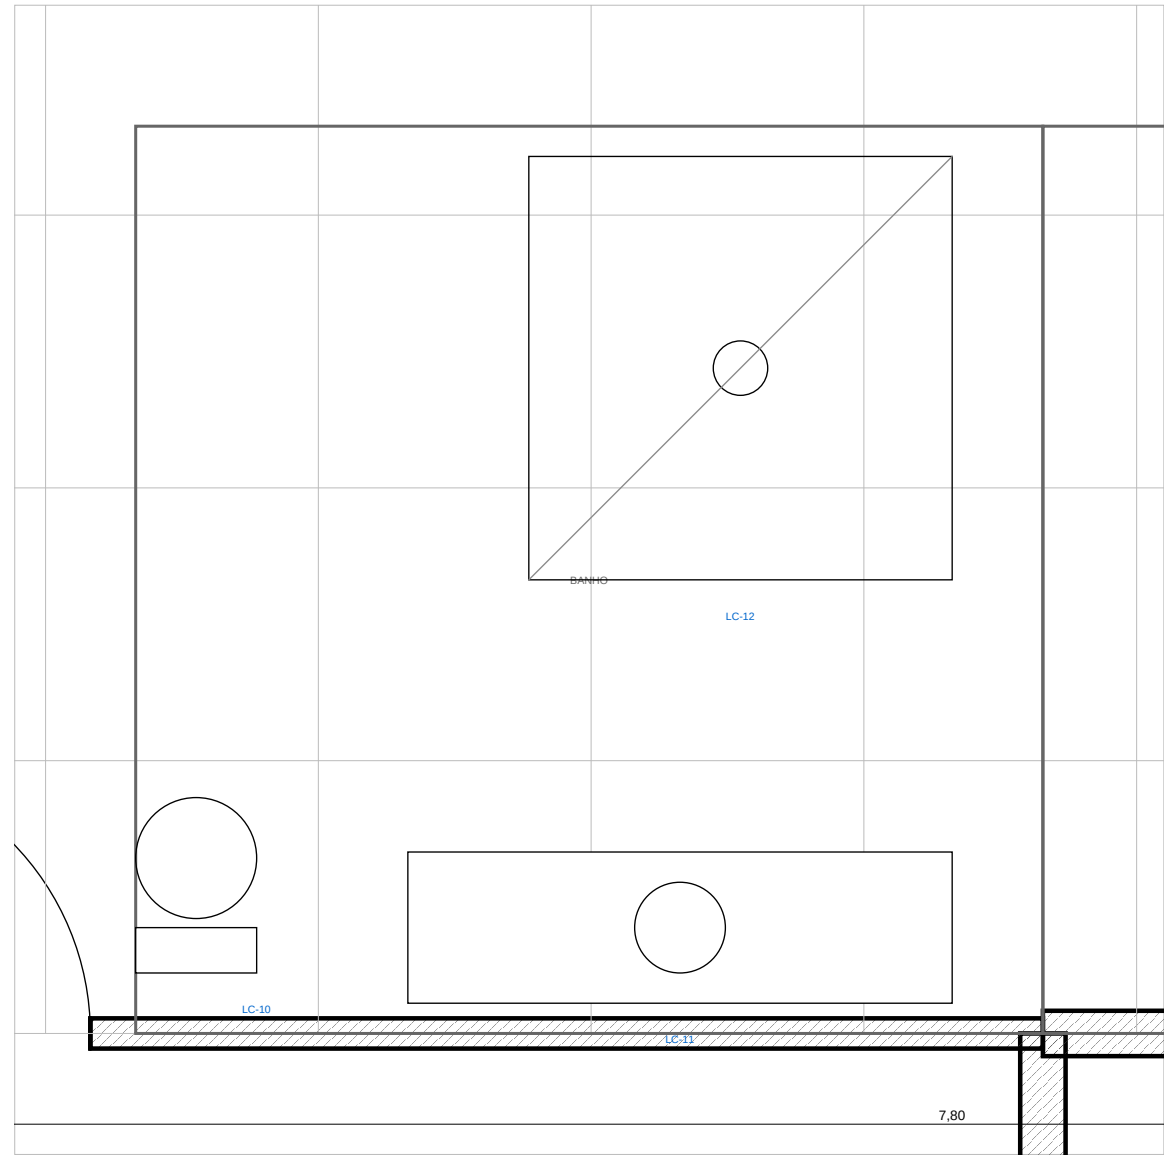

3 MASTER — BANHO  
ESCALA 1:25

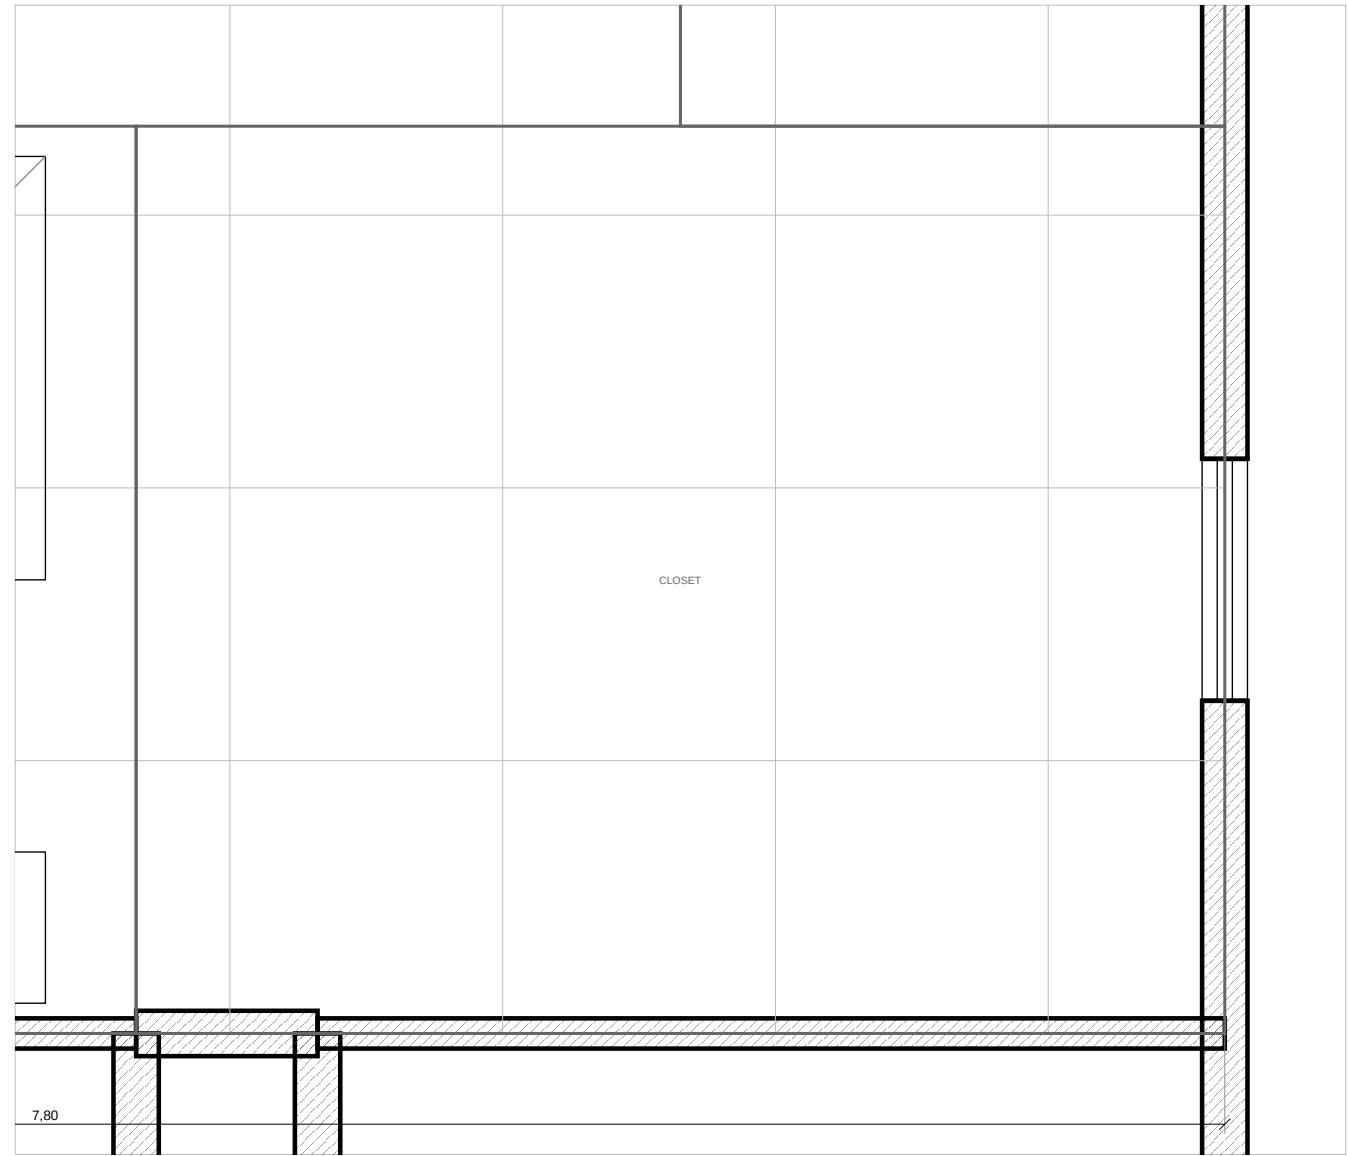

4 MASTER — CLOSET  
ESCALA 1:25

PAGINACAO VERIFICADA — PECAS INTEIRAS + RECORTE EM CADA PONTA

| AMB   | AMBIENTE         | ZONA | PEÇA | EXO X  | EXO Y     | ALTURA (mm) |
|-------|------------------|------|------|--------|-----------|-------------|
| S-002 | SUITE 02 — BANHO | ZP-3 | GRU  | S-002B | S-002B    | ---         |
| S-003 | SUITE 03 — BANHO | ZP-3 | GRU  | S-003B | A-003D07B | ---         |
| S-005 | MASTER — BANHO   | ZP-2 | GRU  | S-005D | S-005B    | ---         |
| S-006 | MASTER — CLOSET  | ZP-2 | GRU  | S-006D | S-006B    | ---         |

NOTAS

- \* Pignonicus de piso em linha fina, a malha vem da ZONA de pignonicus, não do canto do ambiente.
- \* Peca de piso porcelanado retificado 300 x 300, parede ceramico retificado 300 x 600, jato 2 mm.
- \* Cimento de 1:3 para o piso em toda area molhada, soltura elevada 15 mm nos bicos.
- \* Representação: porta ligada em 2 dimensao, altura 200 mm na parede e 1.800 mm nos bicos.

PROJETO PORTO REAL

RESIDENCIA UNIFAMILIAR (MANAUS - AM) | SUITE TATIANA-PS

PROJETO ARQUITETONICO

AMPLIACOES DE AREA MOLHADA — SUPERIOR

|                                                                                    |                                                 |                                                                               |                               |
|------------------------------------------------------------------------------------|-------------------------------------------------|-------------------------------------------------------------------------------|-------------------------------|
| BASE GEOMETRICA<br>Linha Consolidada<br>Projeto (previsão)<br>UNIDADE: METROS - MM | ESCALA<br>1:25<br>FORMATO A1<br>MILIMETROS (MM) | EMISSAO<br>ESTUDO PRELIMINAR R05<br>Linha LIBERADO PARA OBRA<br>SEM ART / RNT | PROJETA<br>23<br>06-25 REV-05 |
|------------------------------------------------------------------------------------|-------------------------------------------------|-------------------------------------------------------------------------------|-------------------------------|