


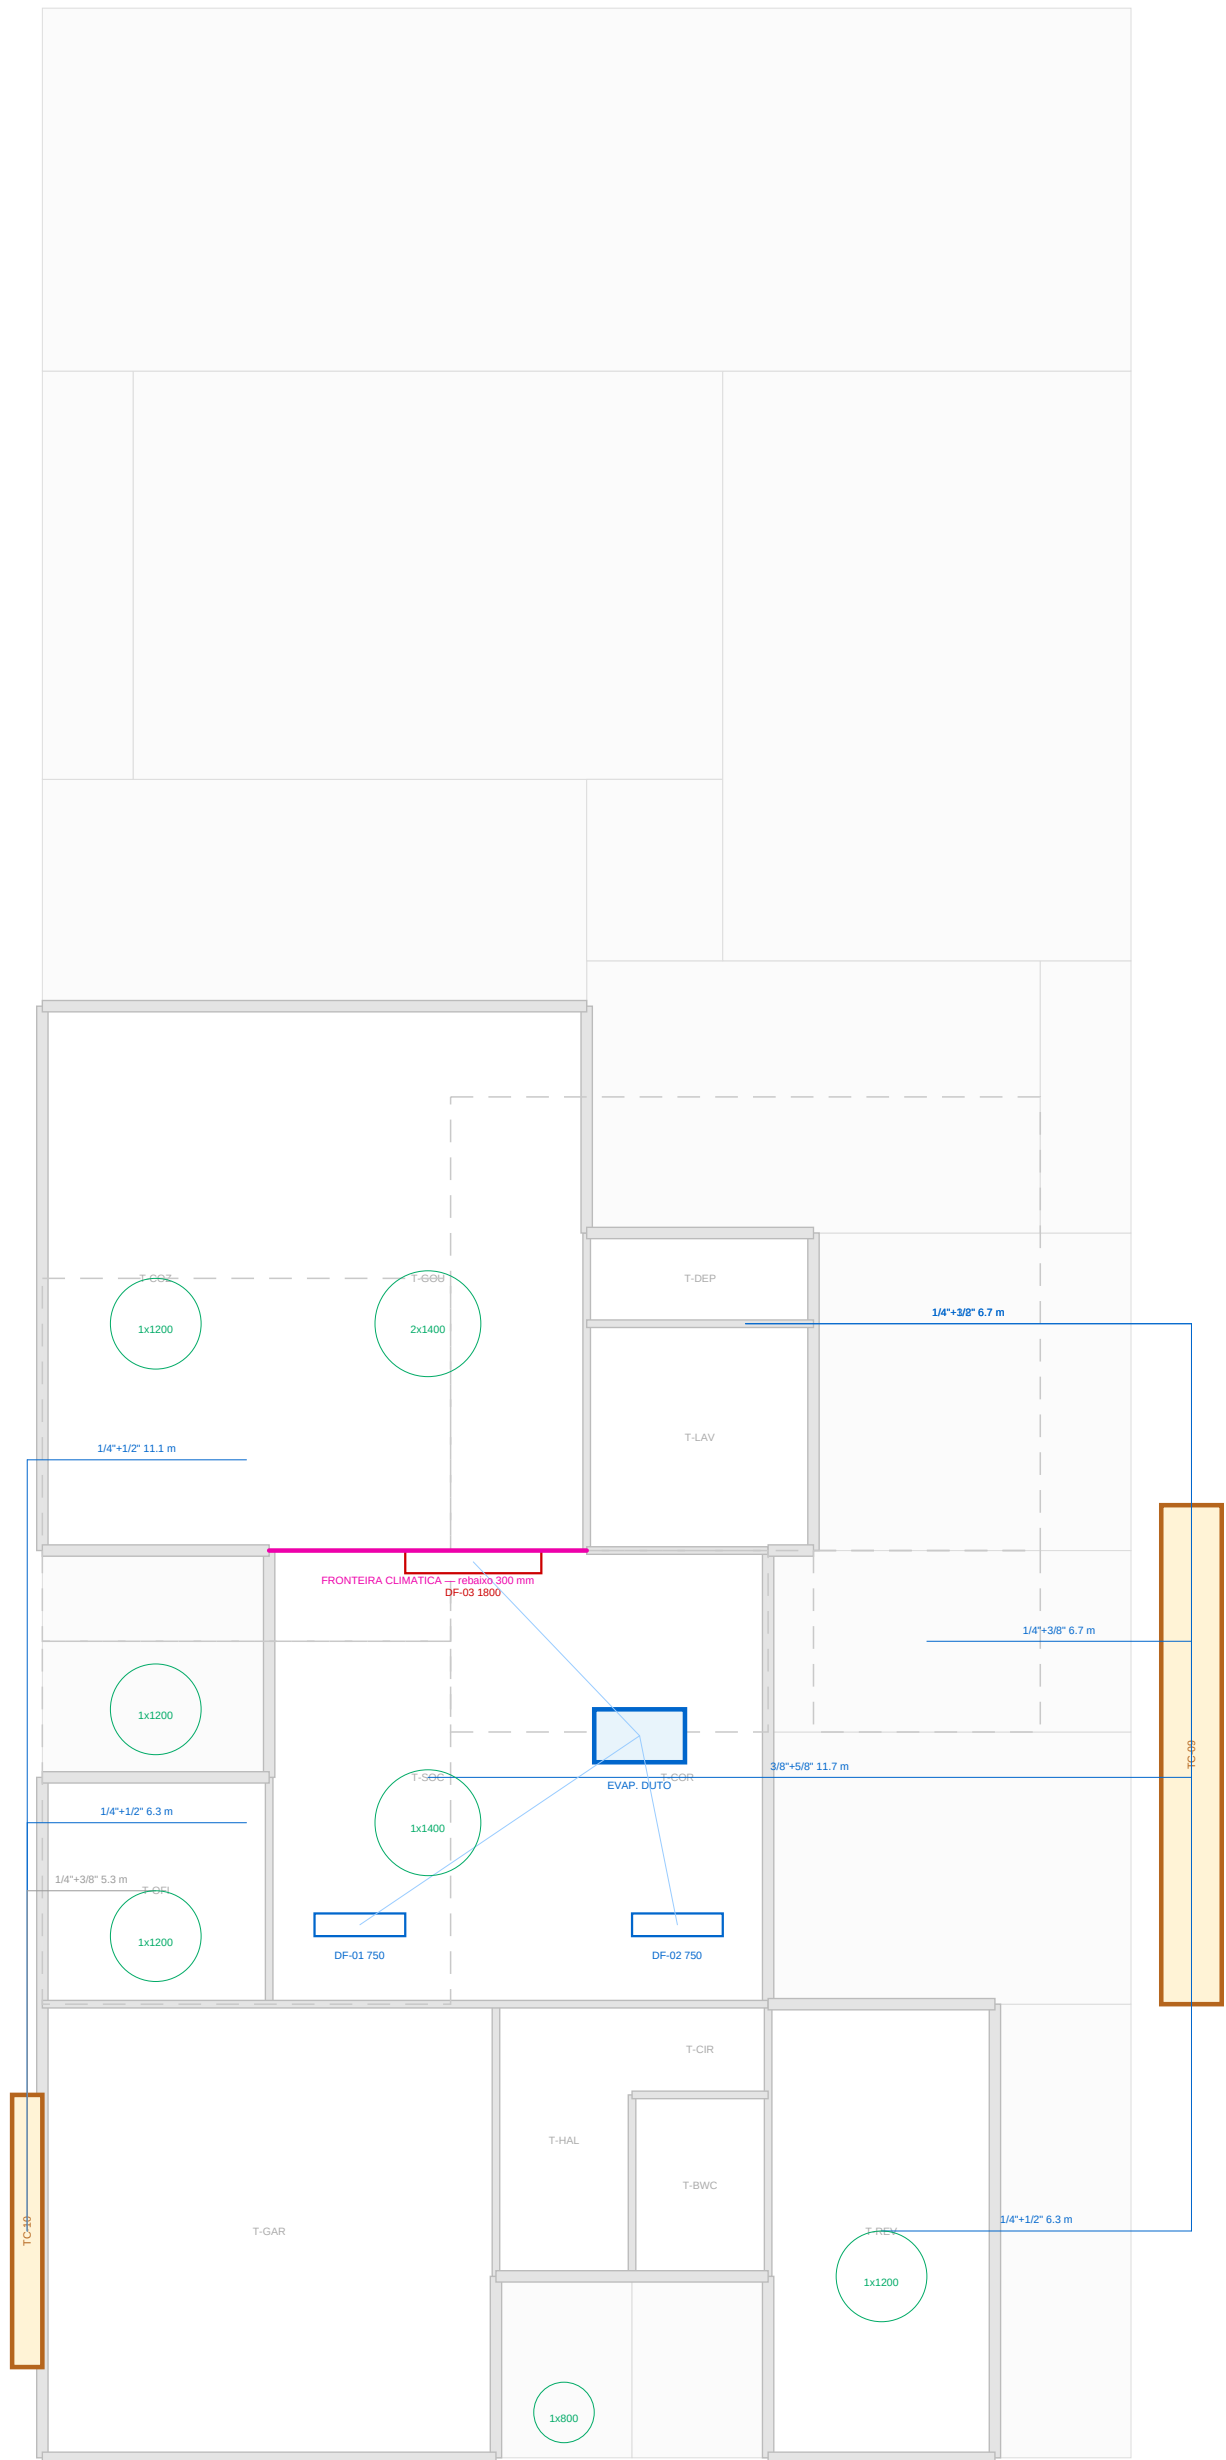

1 PERCURSO DAS LINHAS E DUTOS  
ESCALA 1:100

LINHAS FRIGORÍGENAS — PERCURSO E BITOLA

| Linha | AMB   | INCHO | BTU/h  | HORIZ (m) | VERT (m) | TOTAL (m) | SUCCASÃO (m) | DRENO | CARGA EXTRA | FASE |
|-------|-------|-------|--------|-----------|----------|-----------|--------------|-------|-------------|------|
| S-001 | S-001 | TC-01 | 18.000 | 1,6       | 3,8      | 5,4       | 14'7" 132"   | DN25  | —           | ABR  |
| T-REV | T-REV | TC-01 | 18.000 | 2,2       | 2,6      | 4,8       | 14'7" 132"   | DN25  | —           | ABR  |
| S-002 | S-002 | TC-10 | 18.000 | 1,2       | 3,8      | 5,0       | 14'7" 132"   | DN25  | —           | ABR  |
| S-003 | S-003 | TC-10 | 18.000 | 6,0       | 3,6      | 9,6       | 14'7" 132"   | DN25  | 80 g        | ABR  |
| S-004 | S-004 | TC-08 | 20.000 | 1,6       | 2,8      | 4,4       | 38'7" 381"   | DN25  | 80 g        | ABR  |
| S-005 | S-005 | TC-09 | 9.000  | 1,6       | 3,8      | 5,4       | 14'7" 381"   | DN25  | —           | ABR  |
| PFCE  | S-005 | TC-09 | 9.000  | 1,6       | 3,8      | 5,4       | 14'7" 381"   | DN25  | —           | ABR  |
| T-01  | T-01  | TC-10 | 9.000  | 1,2       | 2,8      | 4,0       | 14'7" 381"   | DN25  | —           | ABR  |

DUTOS, DIFUSORES E EXAUSTÃO

| ELEMENTO          | VIAJADA (mm) | DNOM  | OBSERVAÇÃO                |
|-------------------|--------------|-------|---------------------------|
| DP-01 — insulflex | 750          | T-00C | para parede acima do teto |
| DP-02 — insulflex | 750          | T-00R | com tubo e pino de fix    |

(continuação)

| ELEMENTO           | VIAJADA (mm) | DNOM  | OBSERVAÇÃO |
|--------------------|--------------|-------|------------|
| EX-01 — BENTO 5000 | 85           | T-00C | DN25       |
| EX-02 — BENTO 5000 | 105          | T-00R | DN25       |
| EX-03 — BENTO 5000 | 125          | S-005 | DN25       |
| EX-04 — BENTO 5000 | 85           | S-005 | DN25       |

- NOTAS
- Dots richos de condensação. Linha mais longa 11,7 m, contra o limite de contorno de 15 m.
  - Drenos DN25 com comprimento mínimo de 2m e altura antes da descida, nunca ligado a engate sem alça.
  - Duto de insulflex no comprimento de 400 m — nunca abreviar montado.
  - Isolamento contínuo na travessa de parede, com bucha de passagem, caso de isolamento na parede condensa dentro do montado.

PROJETO PORTO REAL

RESIDENCIA UNIFAMILIAR (MANUS - AM) (SOLUÇÕES - PS)

PROJETO ARQUITETÓNICO

CLIMATIZAÇÃO — LINHAS FRIGORÍGENAS, DUTOS E DRENOS

|                                                            |                                                   |                                                                               |                              |
|------------------------------------------------------------|---------------------------------------------------|-------------------------------------------------------------------------------|------------------------------|
| BASE GEOMÉTRICA<br>Linha Consolidada<br>REV. 02 (previsto) | ESCALA<br>1:100<br>FORMATO A1<br>MILHA 65/500/500 | EXATIDÃO<br>ESTUDO PRELIMINAR R15<br>LIM. LIBERADO PARA OBRA<br>SEM ART / INT | PROVA<br>28<br>IN 25 REV. 02 |
|------------------------------------------------------------|---------------------------------------------------|-------------------------------------------------------------------------------|------------------------------|