




- luminária embuída, 3.000 K, IRC 90
- afcapso técnico 600 x 600 mm
- forro absorvente (alfa 0,70)

FORROS POR AMBIENTE

AMBIENTE	SOLUÇÃO	ÁREA	FOR QUE
T.CC1	forro absorvente (a mineral exposto ao gar	36,34	único ponto que demanda a instalação de 3,20 x gar
T.BOC	gesso fio + cantoneira e lapelas	25,20	abertura entre os módulos, forro técnico aqui for
T.CC2	gesso fio + cantoneira	13,00	superfície de fácil limpeza sem necessidade de for
S.S02	gesso fio + la mineral sobre o forro	25,80	la sobre o forro técnica tudo de chaves no paraf P
S.S03	gesso fio + la mineral sobre o forro	25,80	idem
S.S05	gesso fio + la mineral sobre o forro	25,80	idem
T.GAR	sem forro (estrutura exposta)	36,00	ambiente semi-escuro, acústica não técnica
T.OP1	sem forro (estrutura exposta)	9,00	idem
T.CCP	sem forro (estrutura exposta)	3,00	idem

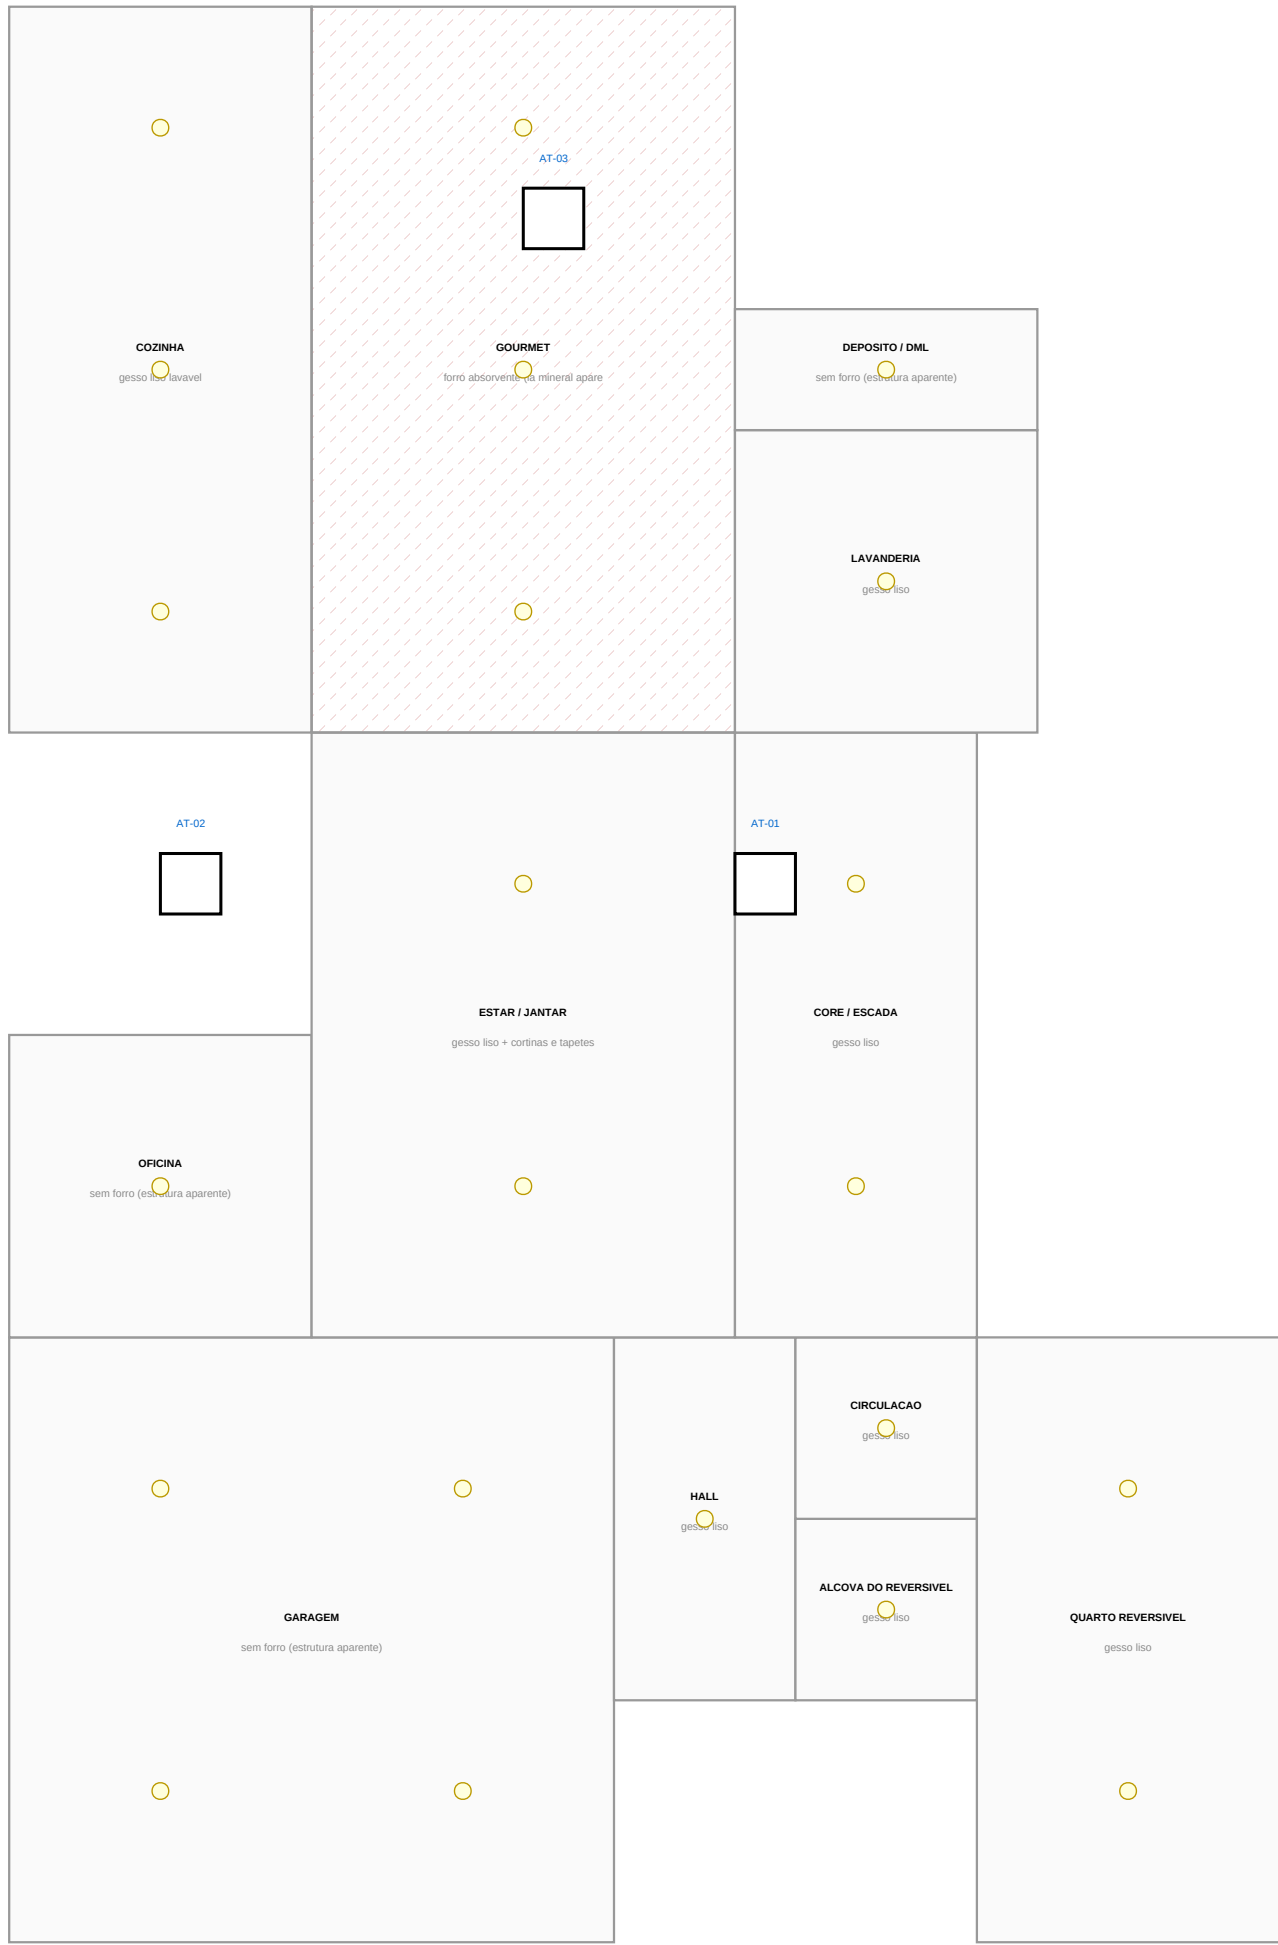

1 FORRO REFLETIDO — TERREO
ESCALA 1:75

- NOTAS
- * Planta refletida: vista do forro projetada no plano horizontal.
 - * Forro absorvente apenas no gourmet — único ponto com necessidade crítica.
 - * Alcapos técnicos de 600 x 600 mm, passando de cobertura de 600 mm.
 - * Luminárias para 3.000 K, IRC máximo 90.

PROJETO PORTO REAL

RESIDENCIA UNIFAMILIAR (MANAUS - AM) | SOUZA TATIANA-PS

PROJETO ARQUITETONICO

PLANTA DE FORRO E ILUMINACAO

BASE GEOMETRICA Linha Consolidada ISO A1/2 (previsível) UNIDADE: METROS - MM	ESCALA 1:75 FORMATO A1 MILHA 405/000000	EMISSAO ESTUDO PRELIMINAR R05 LIMITE LIBERADO PARA OBRAS SEM ART / RNT	PROVA 16 06-48 REV 005
---	--	---	------------------------------