


VERIFICACAO NBR 9050

ITEM	EXISTENTE	PROJETO	
Visão livre de porta	800 mm	940 mm (altura de 900)	OK
Circuito de giro 360 graus	1.500 mm	hall, banheiro e quarto	OK
Desnível sem rampas	até 5 mm	soluções niveladas	OK
Largura de circulação	900 mm	1.800 mm no hall	OK
Barras de apoio	relívato previsto	ambiguidade na PTE 1 e PTE 2	OK
Barras de acessibilidade	altura livre 750 mm	sem problemas sob a calha	OK
Contraste e interruptor	600 a 1.000 mm	a definir no detalhe	pendente



FLUXOS — SEPARACAO DE CIRCUITOS

CIRCUITO	PERCURSO	CRUZAR O SOCIAL?
Serviço	garagem -> oficina -> lavanderia -> cozinha -> despensa	NÃO
Social	entrada -> hall -> estar -> gourmet -> alameda -> piscina	—
Área íntima	hall -> circulação -> banheiro social (quarto reservado) (se não for projeto)	NÃO
Área íntima superior	hall -> core -> hall superior -> suíte	NÃO
Área de carga	cozinha -> despensa -> reservado	NÃO

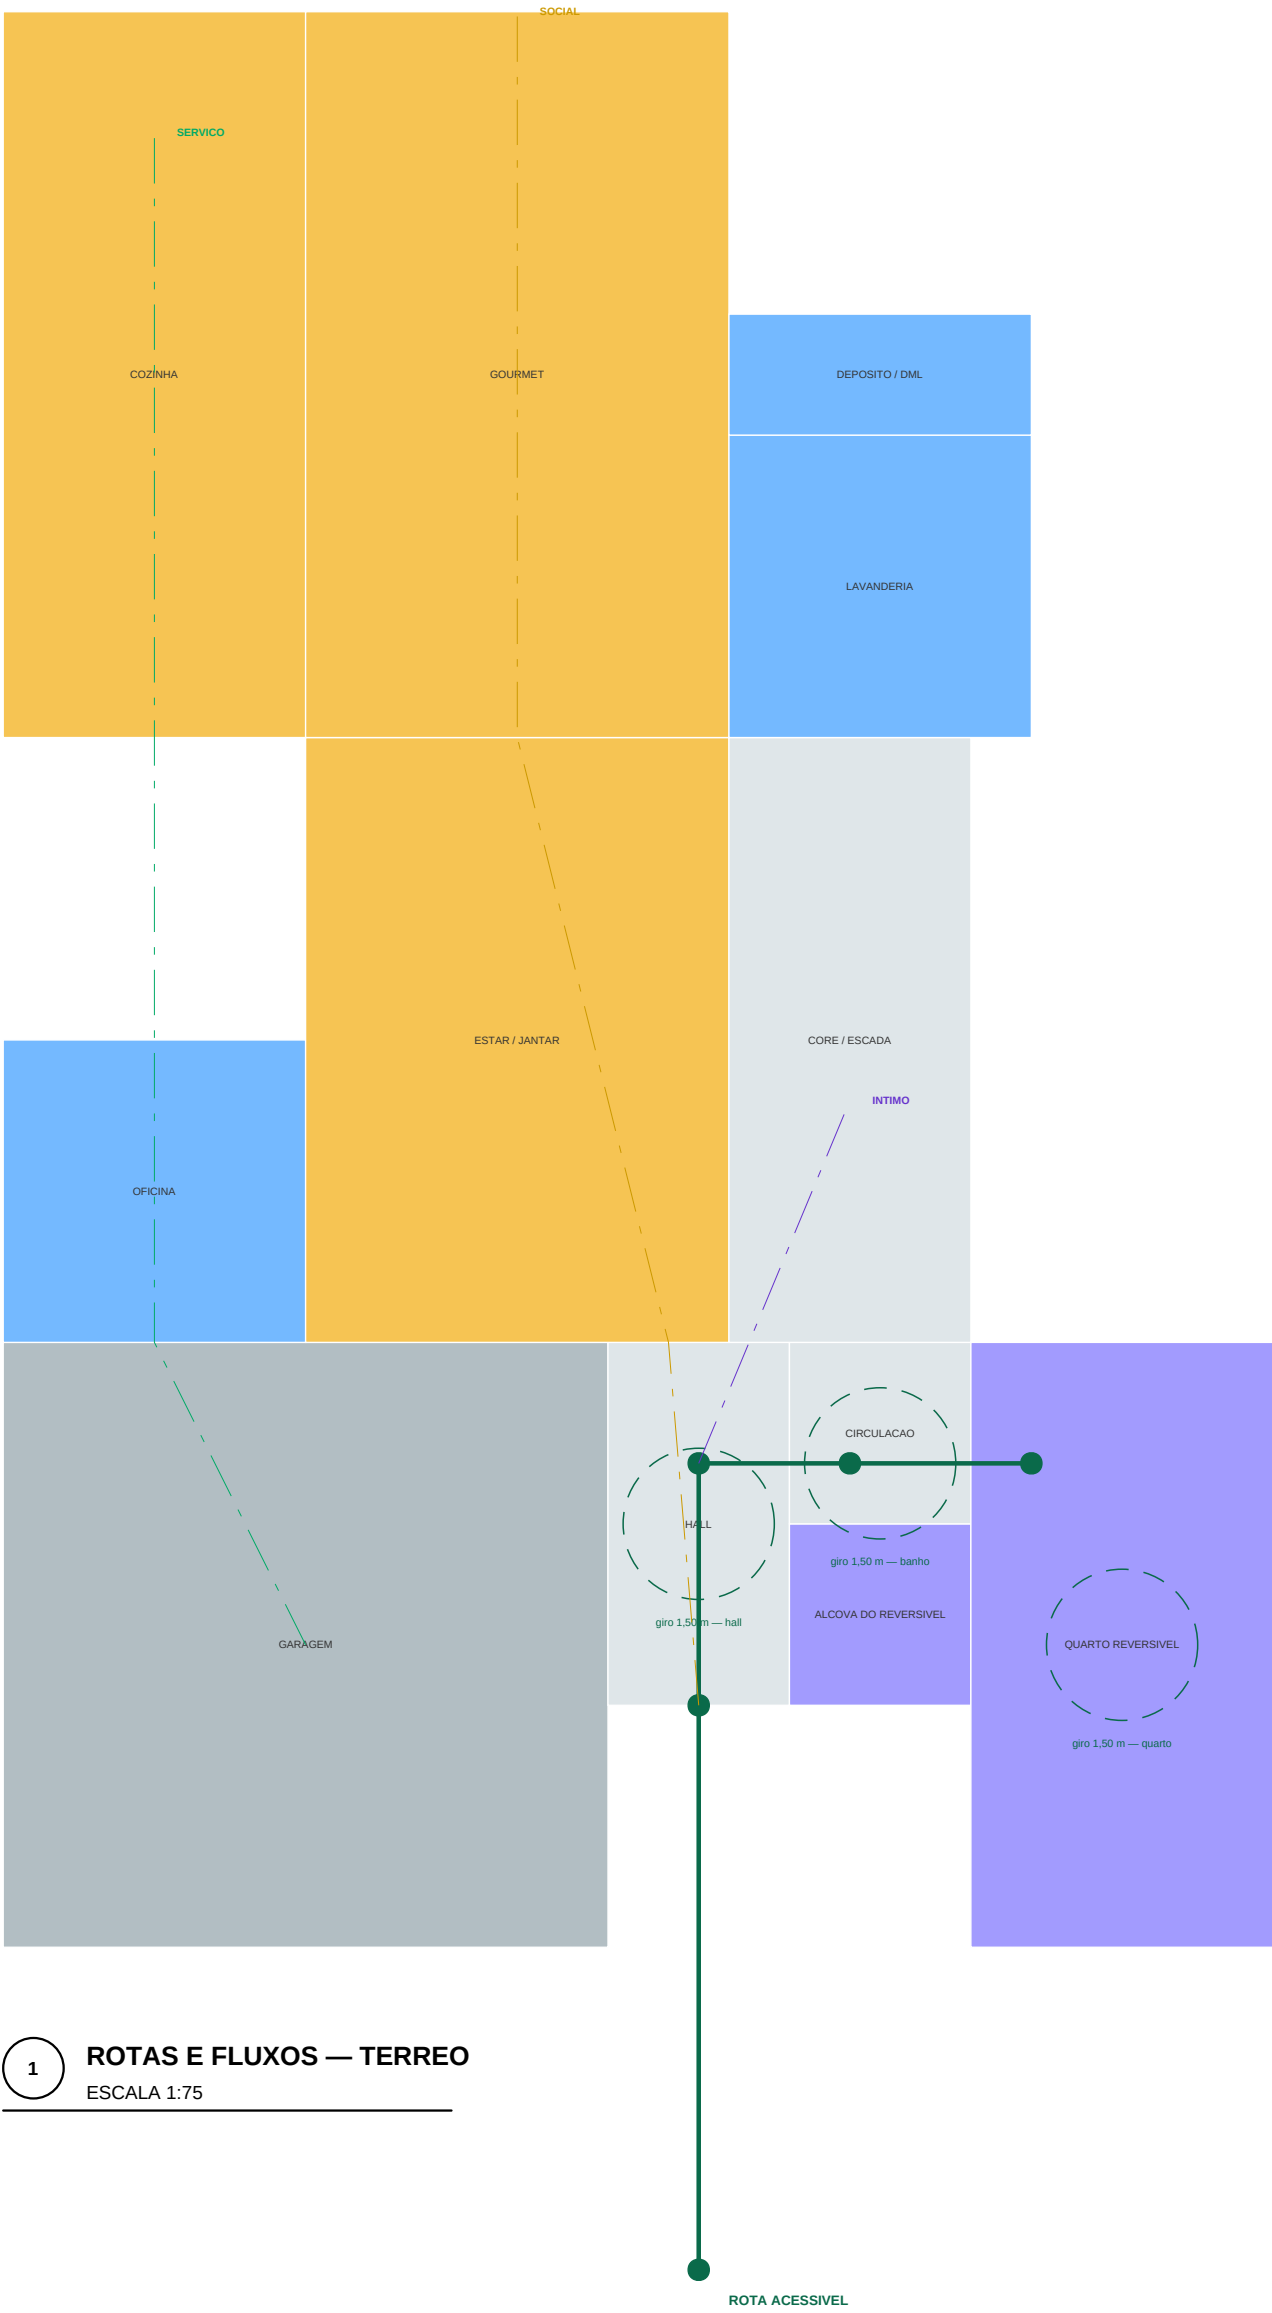

1 ROTAS E FLUXOS — TERREO
ESCALA 1:75

- NOTAS
- * Rota acessível do passeio ao quarto reservado e ao banheiro social.
 - * Circuito de giro de 1.500 mm verificado nos pontos de manobra.
 - * Porta de correr de 900 mm no banheiro social e área de manobra.
 - * Reforço para barras de apoio ambiguidade antes do fechamento das placas.

PROJETO PORTO REAL

RESIDENCIA UNIFAMILIAR (MANSÃO - AM) | SOBR TATIANA-PS

PROJETO ARQUITETONICO

ACESSIBILIDADE E FLUXOS

BASE GEOMETRICA	ESCALA	EMISSAO	PROJECION
União Consolidada	1:75	ESTUDO PRELIMINAR RDS	17
ISO-RDS (previsão)	FORMATO A1	NÃO LIBERADO PARA OBRA	SEM ART / RNT
UNIDADE MESTRE: AM	MALHA 600/600/300	SEM ART / RNT	DE 40 REVIEWS