


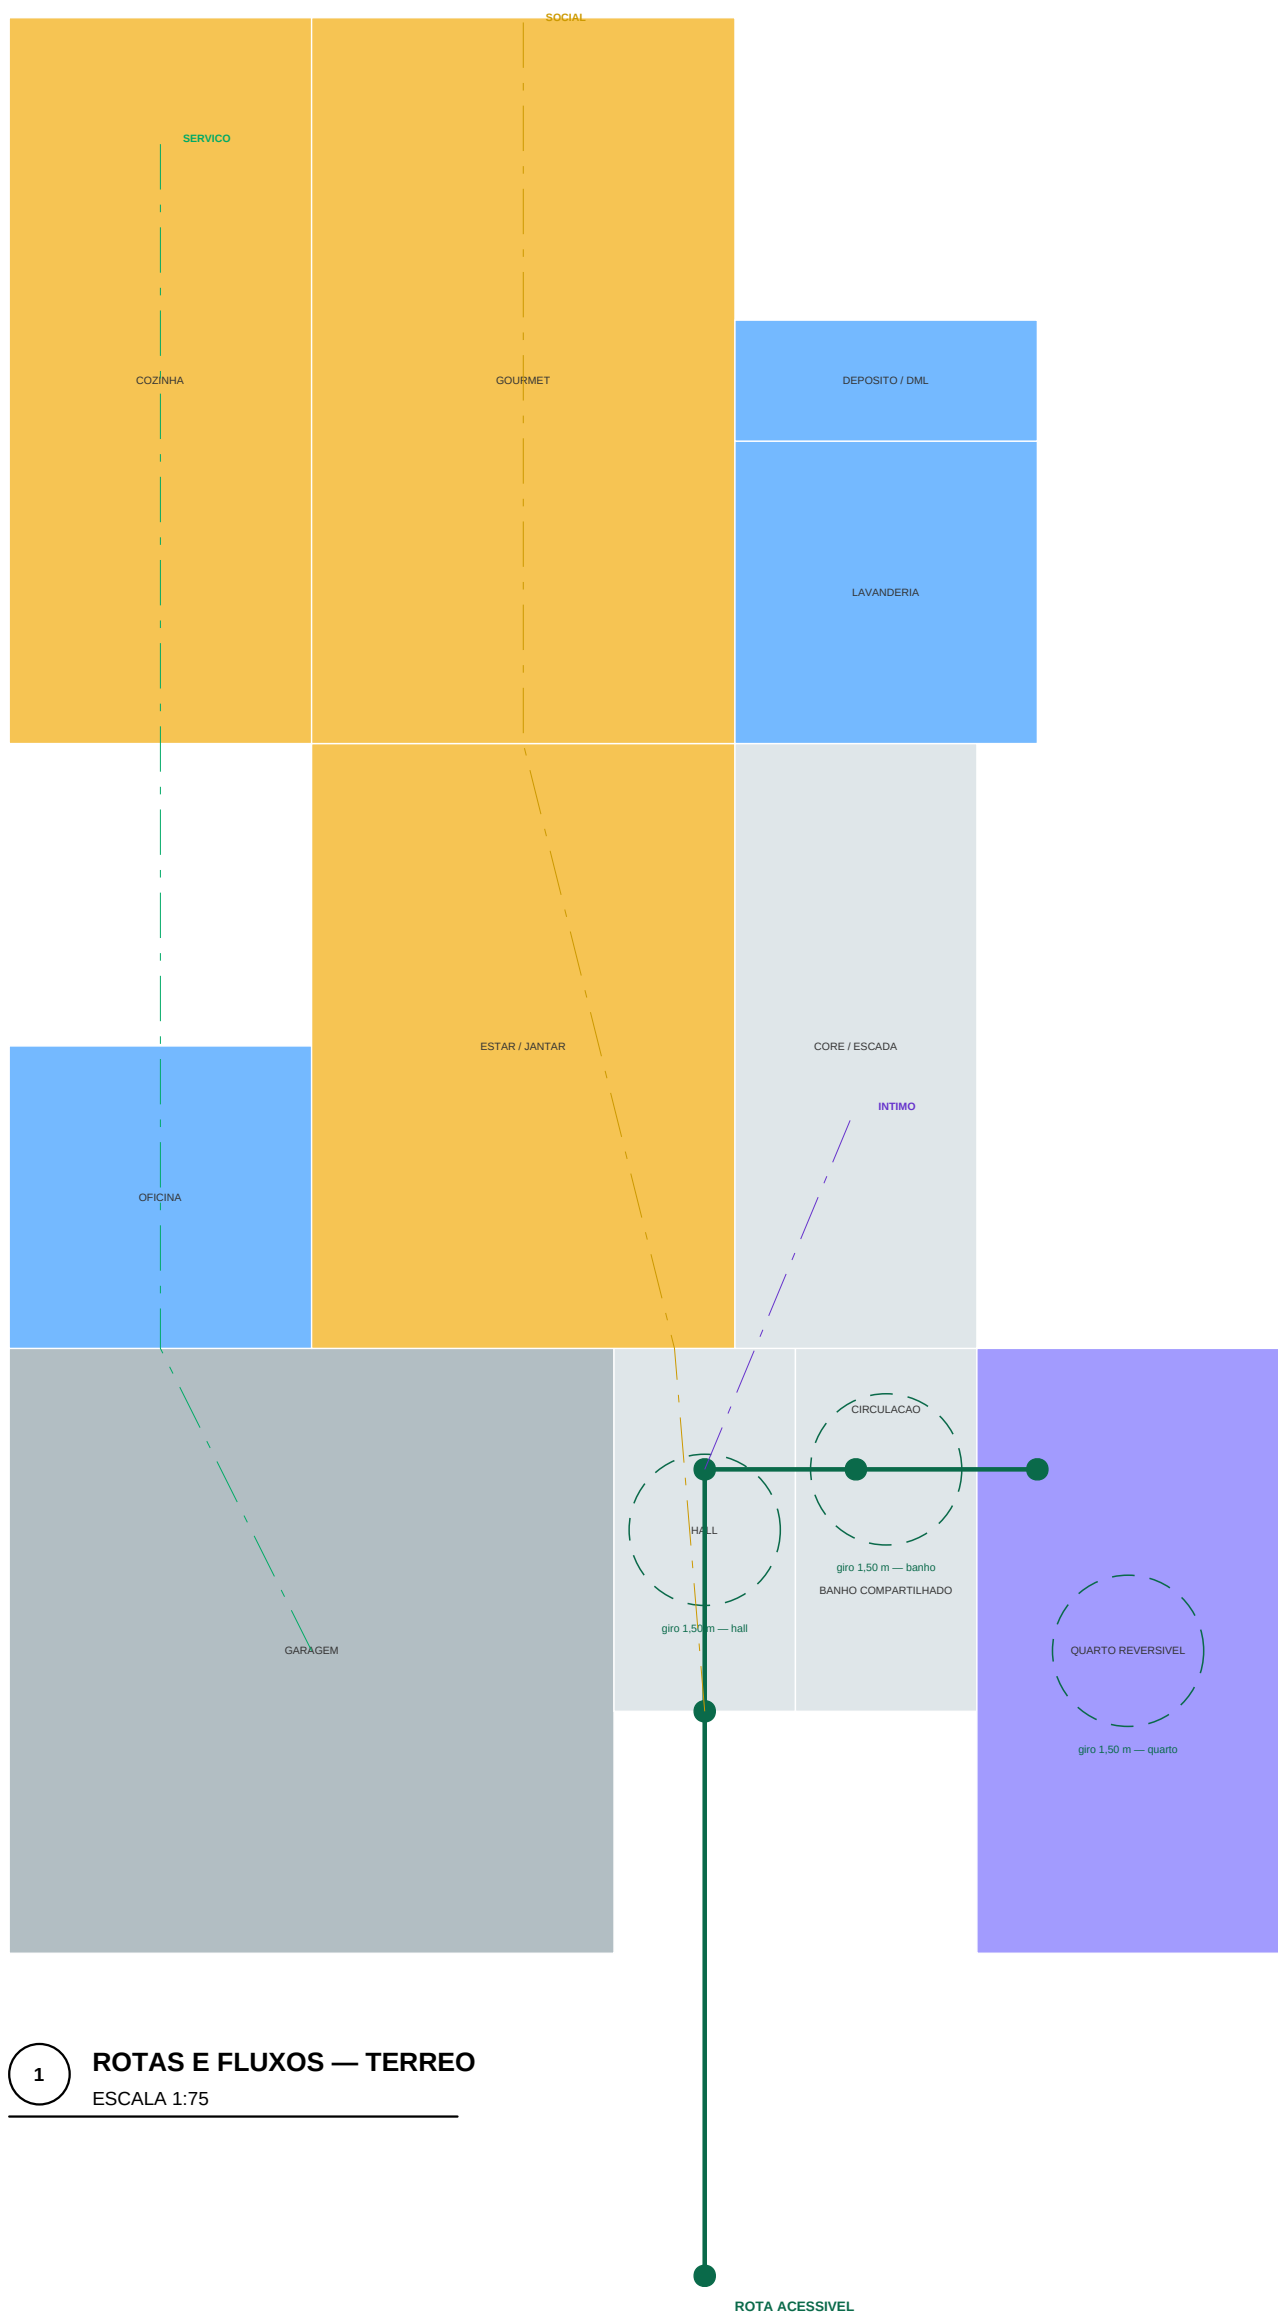


1 ROTAS E FLUXOS — TERREO
ESCALA 1:75

VERIFICACAO NBR 9050

ITEM	EXISTENTE	PROPOSTO	
Vara livre de porta	800 mm	940 mm (altura de 900)	OK
Circulo de giro 360 graus	1.500 mm	hall, banheiro e quarto	OK
Desnivel sem rampas	até 5 mm	terraceira nivelada	OK
Largura de circulação	900 mm	1.800 mm no hall	OK
Barras de apoio	relívio previsto	ambuido no P1 e P10.1	OK
Barras de acesso	altura livre 750 mm	sem barreiras até a calha	OK
Corrimão e interruptor	600 a 1.000 mm	a definir no detalhe	pendente

FLUXOS — SEPARACAO DE CIRCUITOS

CIRCUITO	PERCURSO	CRUZA O SOCIAL?
Servico	garagem -> estufa -> lavanderia -> cozinha -> despensa	NÃO
Social	entrada -> hall -> estar -> gourmet -> alameda -> piscina	—
Área de serviço	hall -> banheiro compartilhado -> quarto reservável	NÃO
Área superior	hall -> cora -> hall superior -> suíte	NÃO
Área de carga	cozinha -> despensa -> reserv. hall	NÃO

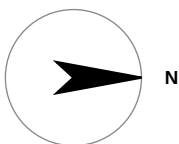

- NOTAS
- * Rota acessível do passeio ao quarto reservável e ao banheiro compartilhado.
 - * Circulo de giro de 1.500 mm verificado nos pontos de manobra.
 - * Porta de correr de 900 mm no banheiro libera a área de manobra.
 - * Reforço para barras de apoio ambuido antes do fechamento das placas.

PROJETO PORTO REAL

RESIDENCIA UNIFAMILIAR (MANAUS - AM) | SUELE TATIANA PI

PROJETO ARQUITETONICO

ACESSIBILIDADE E FLUXOS

BASE GEOMETRICA	ESCALA	EMISSAO	PROJECION
União Consolidada	1:75	ESTUDO PRELIMINAR R33	17
ISO R33 (previsão)	FORMATO A1	NÃO LIBERADO PARA OBRA	SEM ART / RNT
UNIDADE MESTRE: mm	MILIMETROS (ISO 5000/200)		06-25 REV R33